



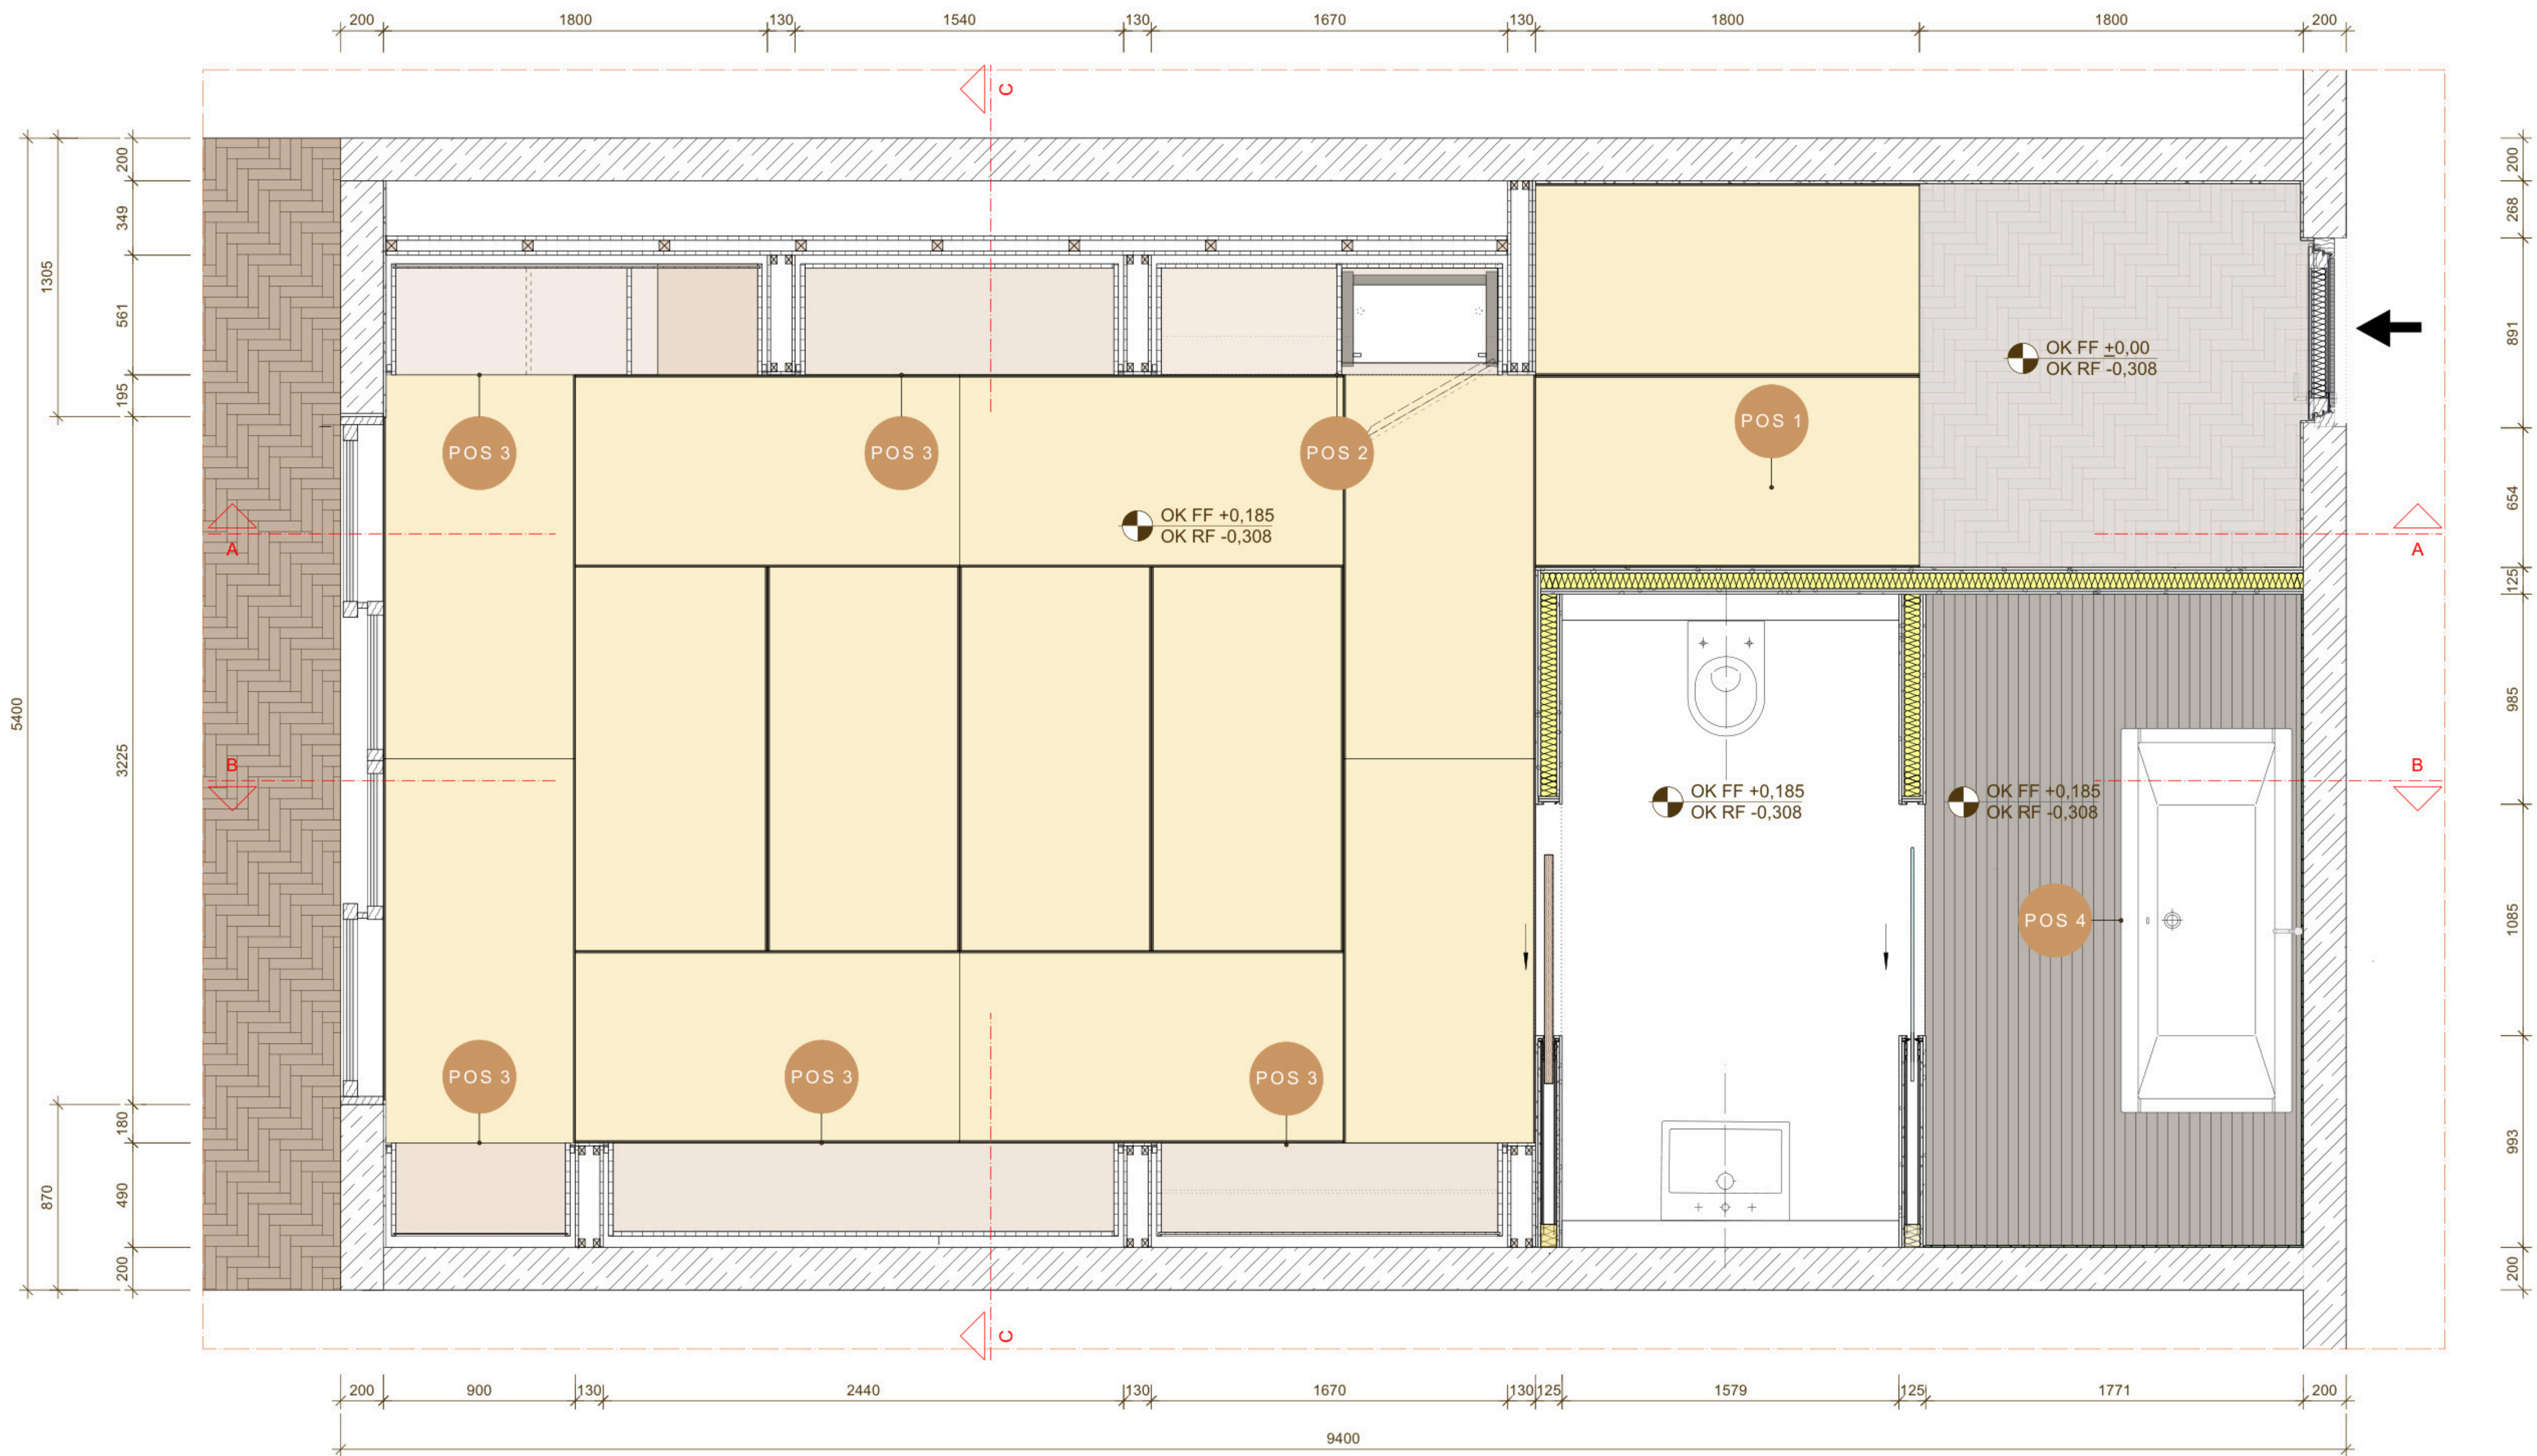

Grundriss M 1:20

Ebene 1	± 0,00 m	
Ebene 2	+ 0,185 m	
Ebene 3	+ 0,185 m	
Ebene 4	+ 0,185 m	

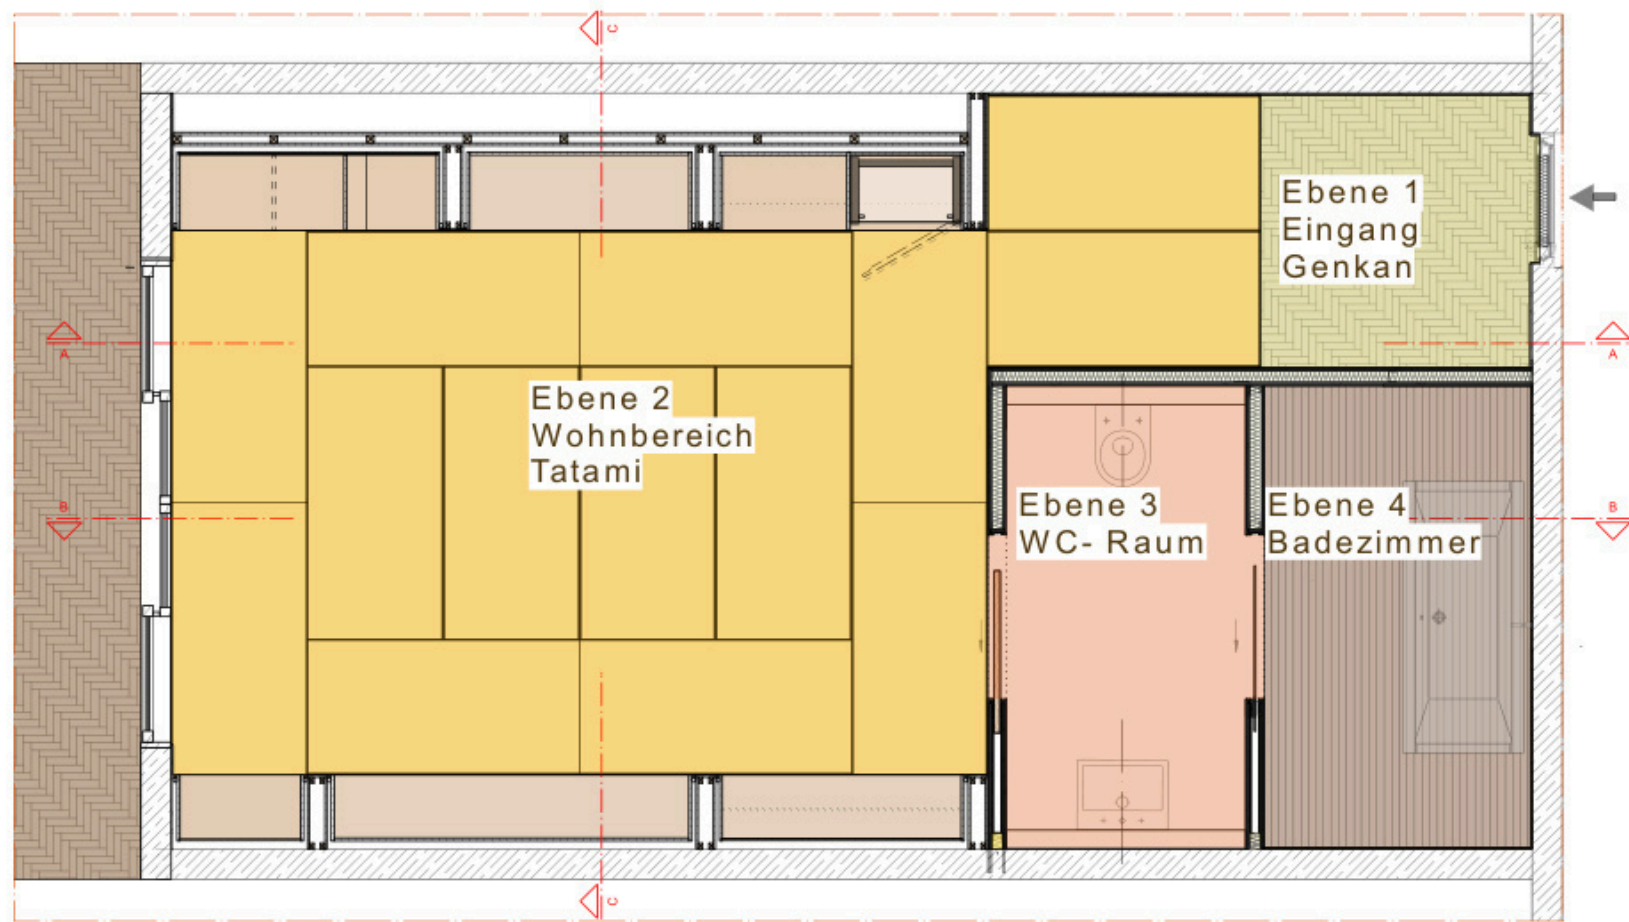

Bodenbelag Schema M 1:50

LEGENDE

BODENAUFBAU

Ohne Erhöhung

Parkett, Eiche geölt	
Heizestrich	12 mm
Trennlage PE-Folie	65 mm
Trittschalldämmung	5 mm
Stahlbeton Bodenplatte	40 mm
Bitumen Andichtung	200 mm
Perimeterdämmung XPS	5 mm
Sauberkeitsschicht	250 mm
Erdreich	50 mm

Mit Erhöhung

Tatami Matten	
Parkett, Eiche geölt	
Heizestrich	
Trennlage PE-Folie	
Trittschalldämmung	40 mm
fermacell Hartschaum	12 mm
fermacell gebundene Schüttung	65 mm
Stahlbeton Bodenplatte	5 mm
Bitumenabdichtung	40 mm
Perimeterdämmung XPS	30 mm
Sauberkeitsschicht	159 mm
Erdreich	200 mm
	5 mm
	250 mm
	50 mm

WANDAUFBAU

Tragende Wände

Stahlbeton
Innenputz Gipsputz

Trockenbauwand

Gipskarton	
Dämmung	
CW-Profil	
Gipskarton	20 mm
Schiebetürsystem von Knauf Pocket Kit Standard	13 mm

Zwischenwände zwischen den Einbauschränken

Holzbaukonstruktion 50x50 mit OSB-Platten	2 x 12,5 mm
	75 mm
	2 x 12,5 mm

DECKENAUFBAU

Stahlbetondecke
Nonius-Abhänger von Knauf
CD-Profile
2 x Gipskarton

POS 1 TATAMIMATTEN

Konstruktion

Kern aus Reisstroh, mit darauf liegender
Binsenmatte mit seitlich angenähten
Baumwollbändern

POS 2 TEEKÜCHE

Konstruktion	200 mm
Multiplex, Eiche furniert, Messerdeckfurnier Eiche geölt	
Beschläge	2 x 12,5 mm

Beschläge

Blum Blumotion Clip Top

Häfele Schleppschanier

Kühlschrank

Kühlschrank Minibar Eco 32 Hartmann

POS 3 EINBAUSCHRÄNKE

Konstruktion	900x1800 mm
Multiplex, Eiche furniert, Messerdeckfurnier Eiche geölt	
Schubkästen MPX Eiche furniert, Messerdeckfurnier Eiche geölt	
Beschläge	
Schubladien im Kleiderschrank Unterflurführung Blum Tandem NL 480	
Frontschubladien Unterflurführung Blum Movento	
Blum Blumotion Clip top	

POS 4 BADEWANNE

Konstruktion	
Eingelassene Badewanne im Wagenträger von Reuter	

AUS 2 Innenausbau 2

Projekt	Hotelzimmer
---------	-------------

Planverfasser	Schabnam Shor - 883436
---------------	------------------------


Prüfer	Prof. Dipl. Ing. W. Glas
--------	--------------------------

Assistent	M. A. Jonas Wilhelm
-----------	---------------------

Semester	Sommersemester 2024
----------	---------------------

Inhalt	Grundriss	Maßstab
	Bodenbelag Schema	1:20
		1:50

Plannummer	01 // 08	Präsentation
		17.07.2024

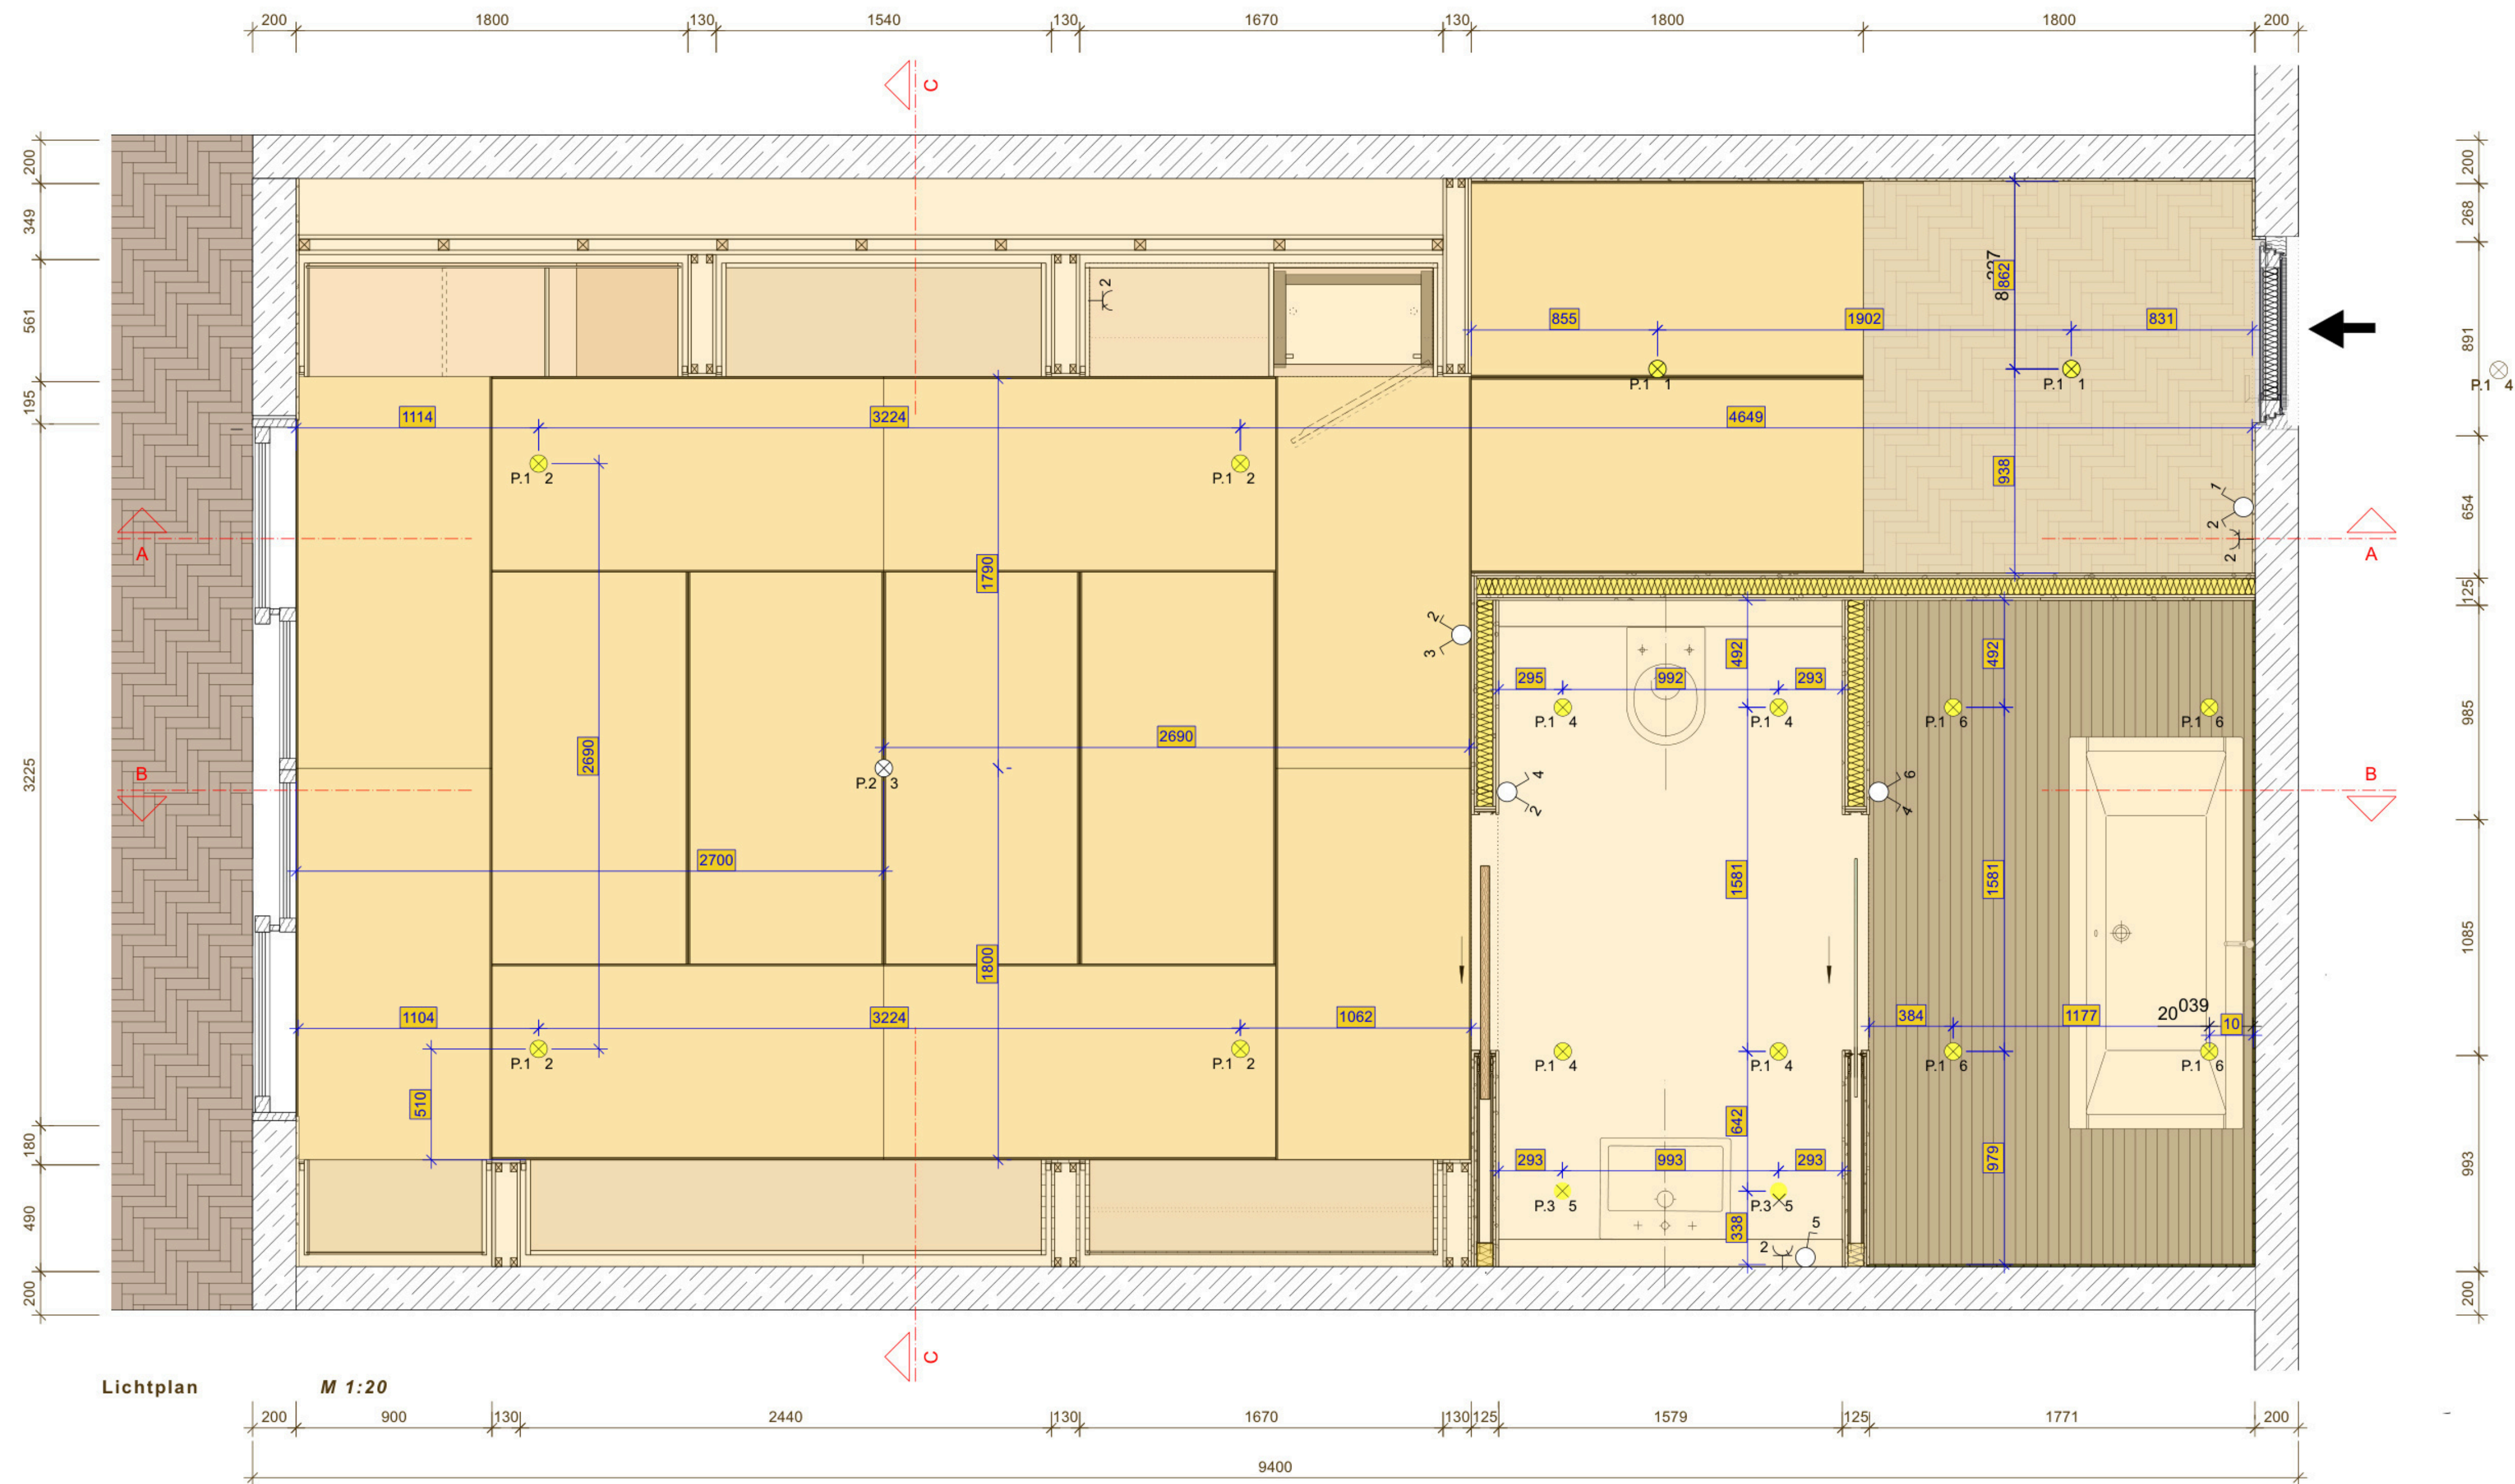


P.1 Deckeneinbauleuchte,
iGuzzini Blade R Minimal, ø80 mm, 2700 K




P.2 Deckenleuchte
Meyda Tiffany Santa Fe 4 Light 18"



P.3 Pendelleuchte aus Travertin und Holz (Ø6,5 cm)
Davise von SKLUM

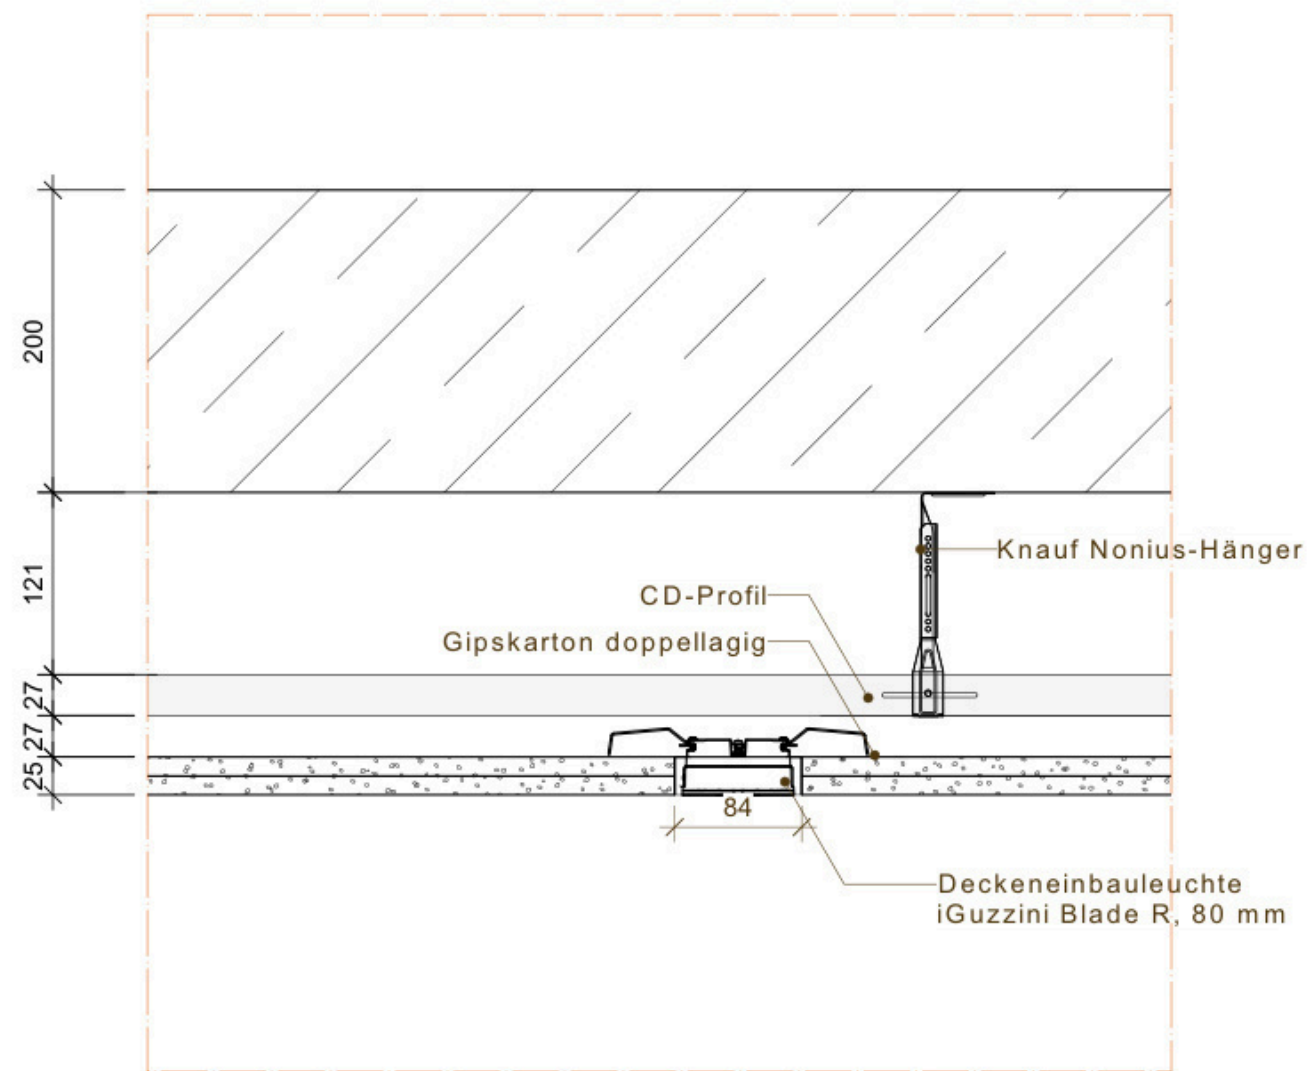

Deckeneinbauleuchte Detail M 1:5

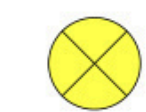

Downlight



Pendelleuchte



Deckenleuchte



Schalter / 1fach



Schalter / 2fach



Steckdose Schutzkontakt
2fach

LEGENDE

BODENAUFBAU

Ohne Erhöhung	
Parkett, Eiche geölt	12 mm
Heizestrich	65 mm
Trennlage PE-Folie	5 mm
Trittschalldämmung	40 mm
Stahlbeton Bodenplatte	200 mm
Bitumen Andichtung	5 mm
Perimeterdämmung XPS	250 mm
Sauberkeitsschicht	50 mm
Erdreich	

Mit Erhöhung	
Tatami Matten	40 mm
Parkett, Eiche geölt	12 mm
Heizestrich	65 mm
Trennlage PE-Folie	5 mm
Trittschalldämmung	40 mm
fermacell Hartschaum	30 mm
fermacell gebundene Schüttung	159 mm
Stahlbeton Bodenplatte	200 mm
Bitumenabdichtung	5 mm
Perimeterdämmung XPS	250 mm
Sauberkeitsschicht	50 mm
Erdreich	

WANDAUFBAU

Tragende Wände	
Stahlbeton	20 mm
Innenputz Gipsputz	13 mm

Trockenbauwand	
Gipskarton	2 x 12,5 mm
Dämmung	75 mm
CW-Profil	
Gipskarton	2 x 12,5 mm
Schiebetürsystem von Knauf Pocket Kit Standard	

Zwischenwände zwischen den Einbauschränken
Holzbaukonstruktion 50x50 mit OSB-Platten

DECKENAUFBAU	
Stahlbetondecke	200 mm
Nonius-Abhänger von Knauf	
CD-Profil	2 x 12,5 mm
2 x Gipskarton	


POS 1 TATAMIMATTEN	
Konstruktion	
Kern aus Reisstroh, mit daraufliegender Binsenmatte mit seitlich angenähten Baumwollbändern	900x1800 mm

POS 2 TEEKÜCHE	
Konstruktion	
Multiplex, Eiche funiert, Messerdeckfunier Eiche geölt	
Beschläge	
Blum Blumotion Clip Top	
Häfele Schleppschanier	
Kühlschrank	
Kühlschrank Minibar Eco 32 Hartmann	


POS 3 EINBAUSCHRÄNKE	
Konstruktion	
Multiplex, Eiche funiert, Messerdeckfunier Eiche geölt	
Schubkästen MPX Eiche funiert, Messerdeckfunier Eiche geölt	
Beschläge	
Schubladen im Kleiderschrank Unterflurführung Blum Tandem NL 480	
Frontschubladen Unterflurführung Blum Movento	
Blum Blumotion Clip top	

POS 4 BADEWANNE	
Konstruktion	
Eingelassene Badewanne im Wagenträger von Reuter	

AUS 2	Innenausbau 2	
Projekt	Hotelzimmer	
Planverfasser	Schabnam Shor - 883436	Inhalt
Prüfer	Prof. Dipl. Ing. W. Glas	Lichtplan
Assistent	M. A. Jonas Wilhelm	Maßstab
Semester	Sommersemester 2024	1:20
Plannummer	02 // 08	Präsentation
		17.07.2024

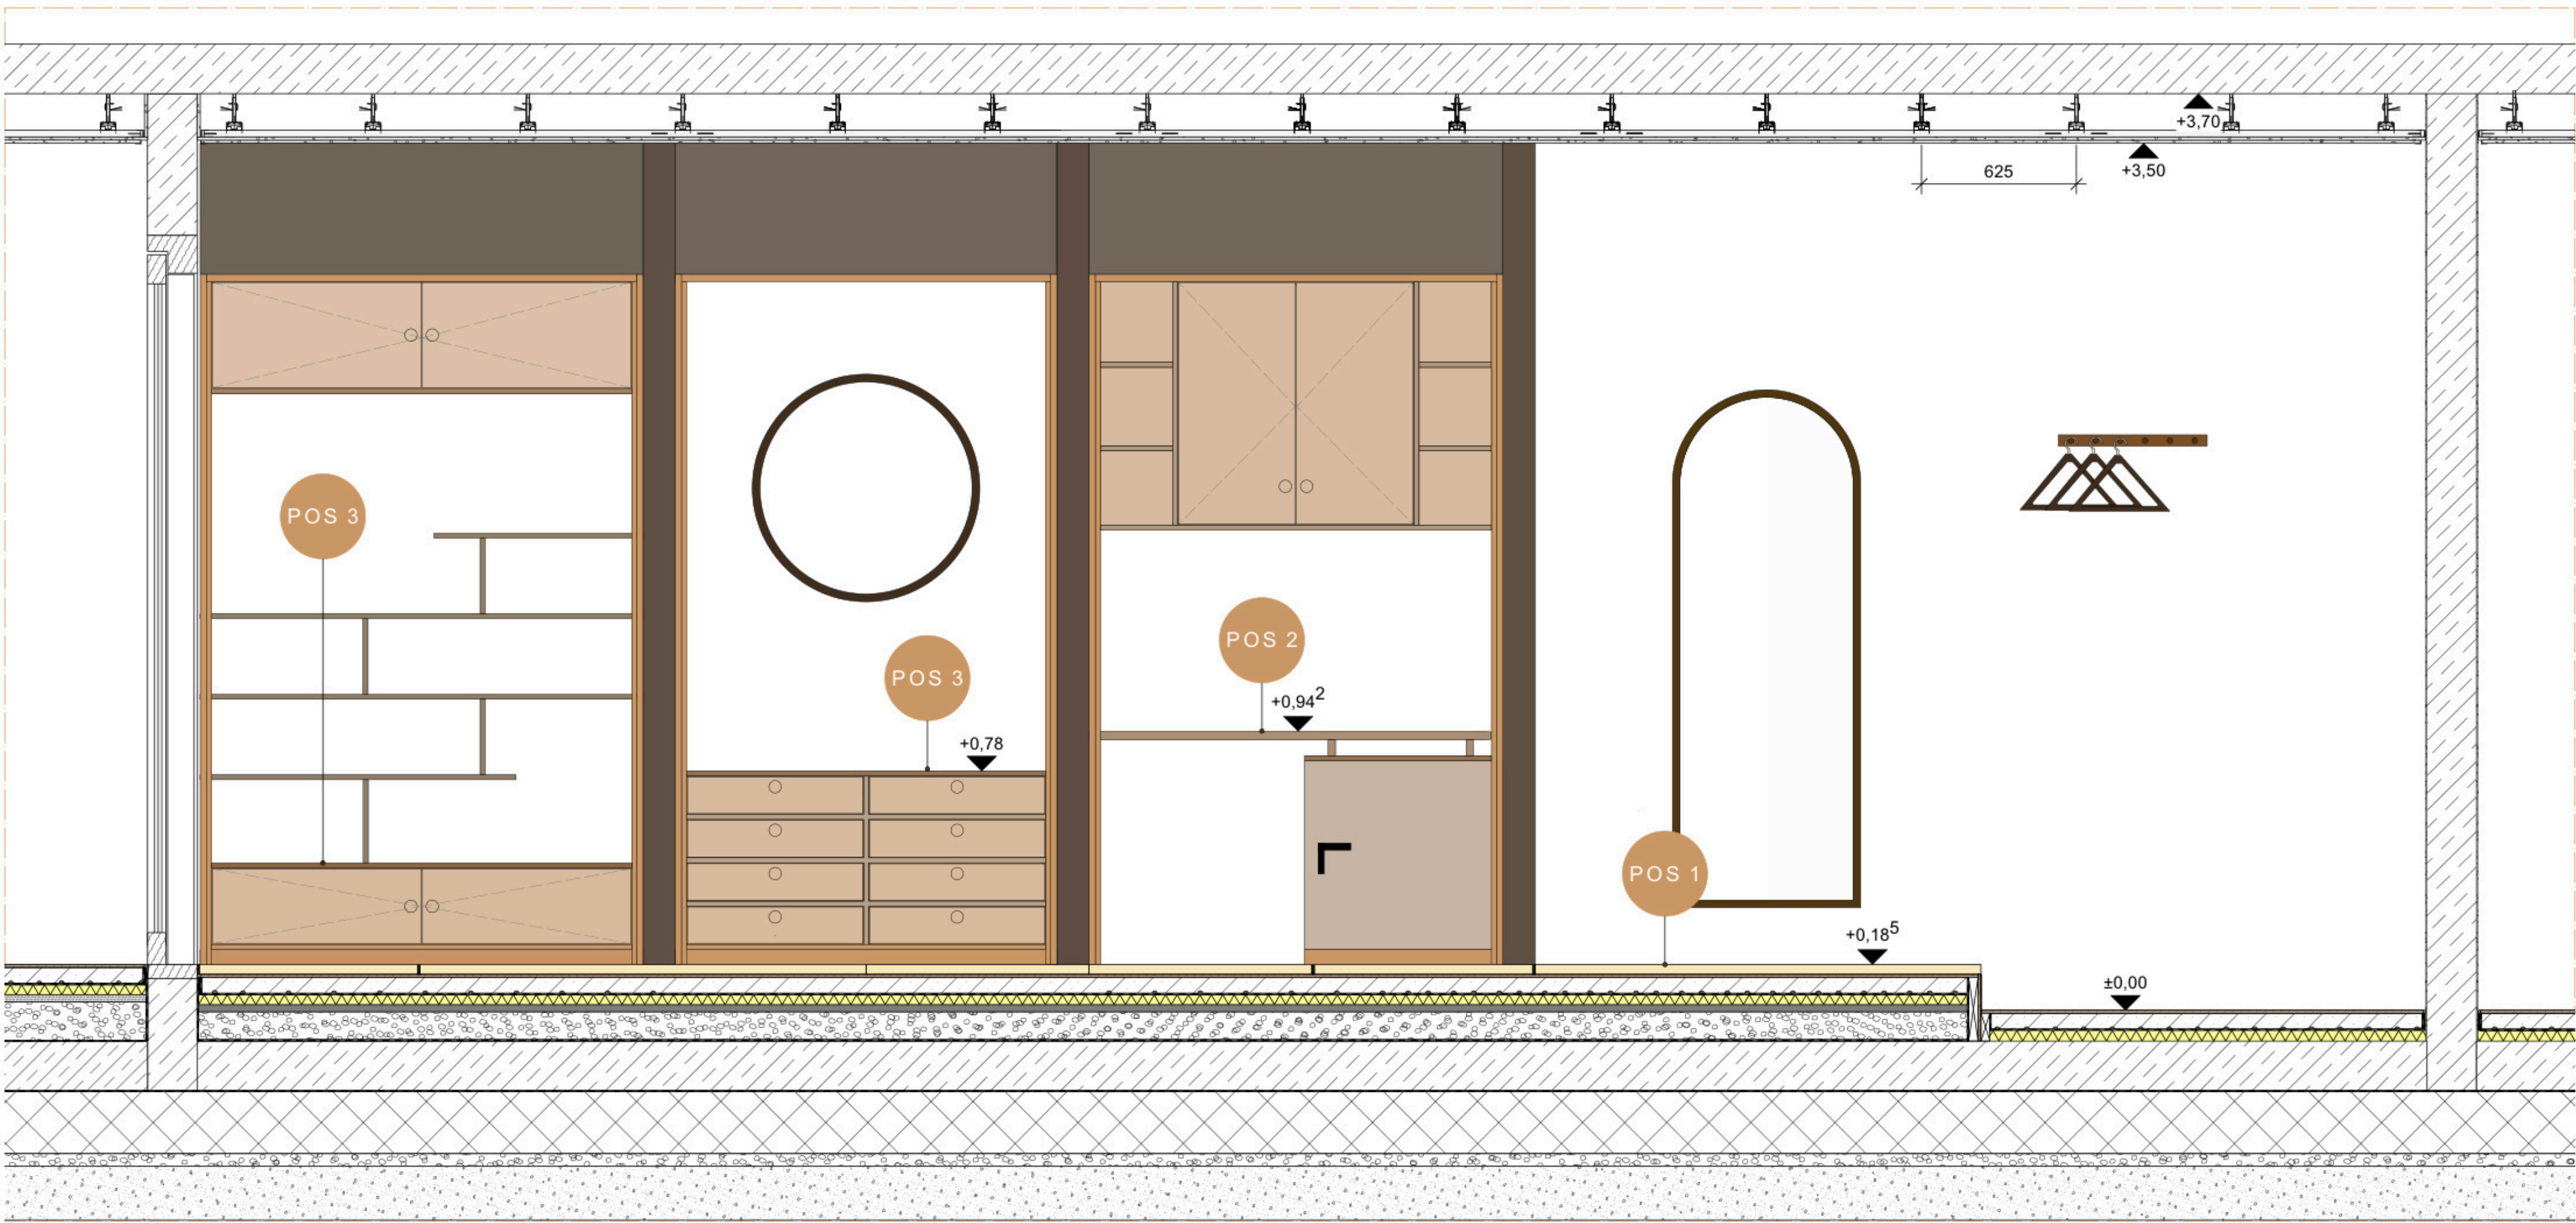

Längsschnitt A-A' M 1:20

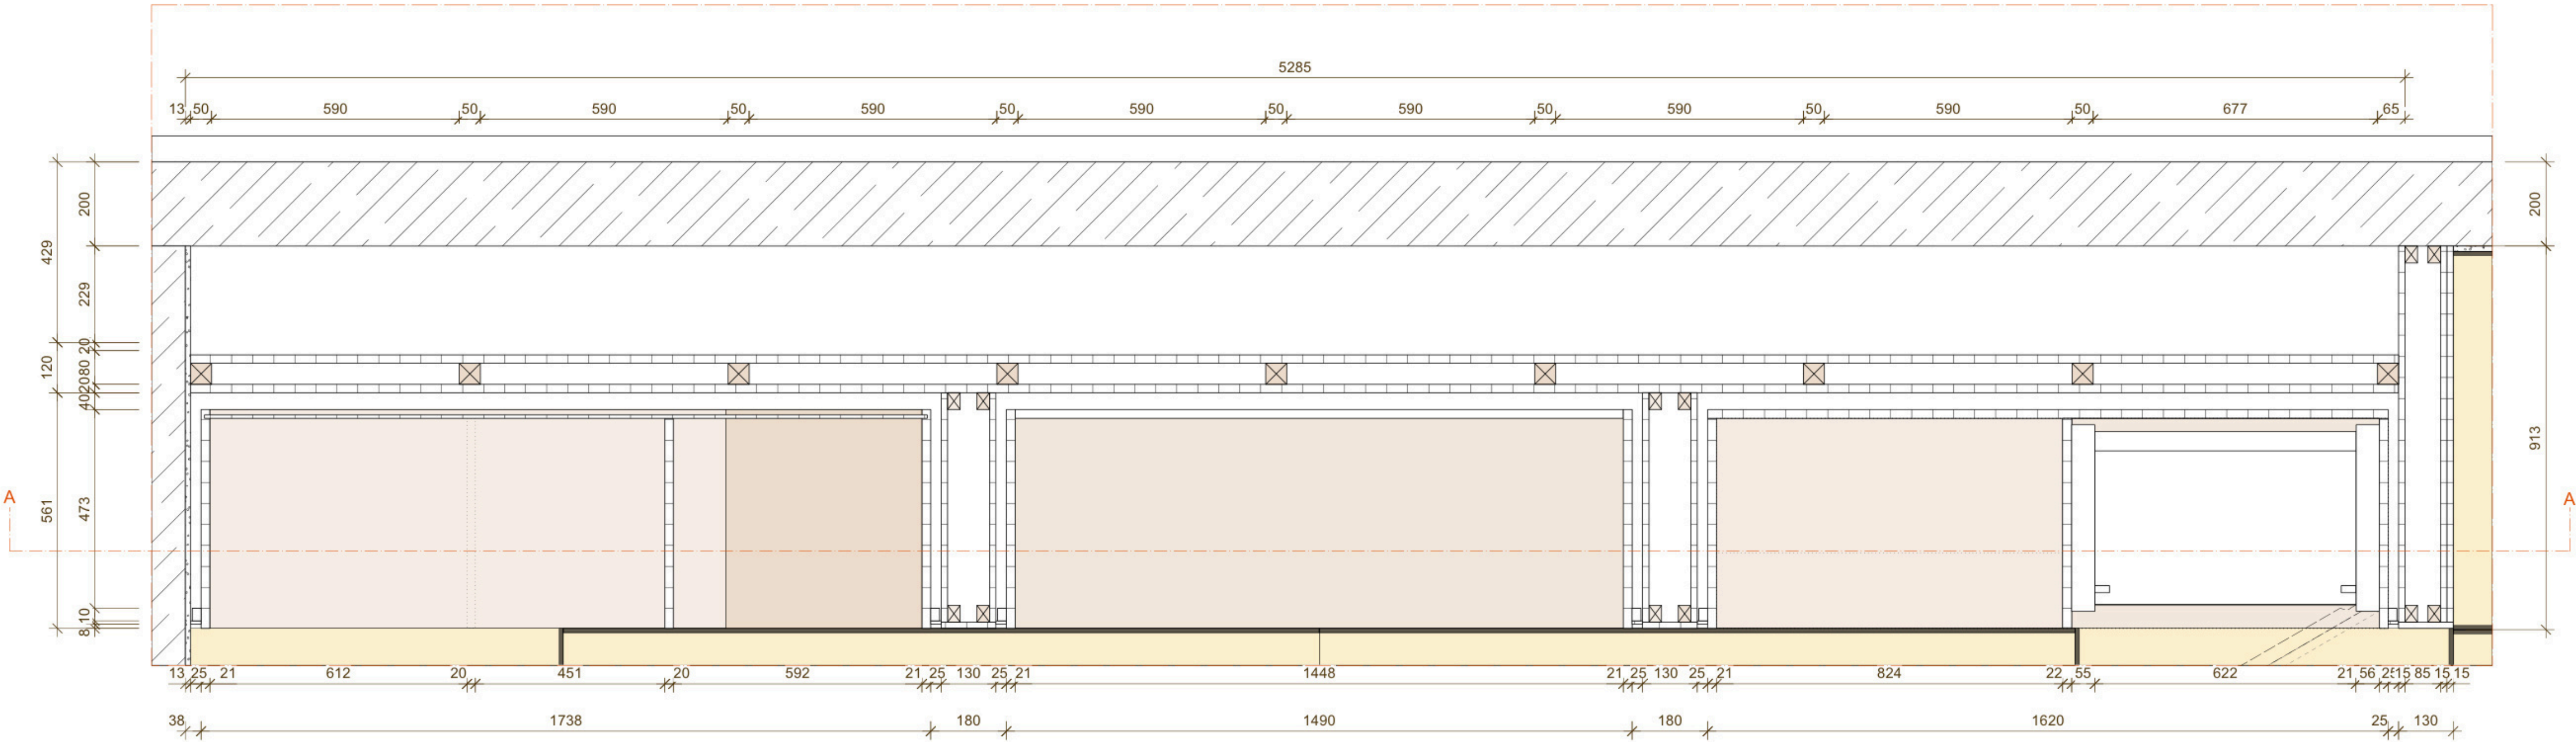

Einbauschränke Schnitt B-B' M 1:10

LEGENDE

BODENAUFBAU

Ohne Erhöhung		
Parkett, Eiche geölt	12	mm
Heizestrich	65	mm
Trennlage PE-Folie	5	mm
Trittschalldämmung	40	mm
Stahlbeton Bodenplatte	200	mm
Bitumen Andichtung	5	mm
Perimeterdämmung XPS	250	mm
Sauberkeitsschicht	50	mm
Erdreich		

Mit Erhöhung		
Tatami Matten	40	mm
Parkett, Eiche geölt	12	mm
Heizestrich	65	mm
Trennlage PE-Folie	5	mm
Trittschalldämmung	40	mm
fermacell Hartschaum	30	mm
fermacell gebundene Schüttung	159	mm
Stahlbeton Bodenplatte	200	mm
Bitumenabdichtung	5	mm
Perimeterdämmung XPS	250	mm
Sauberkeitsschicht	50	mm
Erdreich		

WANDAUFBAU

Tragende Wände	20	mm
Stahlbeton	13	mm
Innenputz Gipsputz		

Trockenbauwand		
Gipskarton	2 x 12,5	mm
Dämmung	75	mm
CW-Profil		
Gipskarton	2 x 12,5	mm
Schiebetürsystem von Knauf Pocket Kit Standard		

Zwischenwände zwischen den Einbauschränken		
Holzbaukonstruktion 50x50 mit OSB-Platten		

DECKENAUFBAU	200	mm
Stahlbetondecke		
Nonius-Abhänger von Knauf		
CD-Profil	2 x 12,5	mm
2 x Gipskarton		

POS 1 TATAMIMATTEN

Konstruktion	900x1800	mm
Kern aus Reisstroh, mit daraufliegender Binsenmatte mit seitlich angenähten Baumwollbändern		

POS 2 TEEKÜCHE

Konstruktion		
Multiplex, Eiche funiert, Messerdeckfunier Eiche geölt		
Beschläge		
Blum Blumotion Clip Top		
Häfele Schleppschanier		
Kühlschrank		
Kühlschrank Minibar Eco 32 Hartmann		


POS 3 EINBAUSCHRÄNKE

Konstruktion		
Multiplex, Eiche funiert, Messerdeckfunier Eiche geölt		
Schubkästen MPX Eiche funiert, Messerdeckfunier Eiche geölt		
Beschläge		
Schubladen im Kleiderschrank Unterflurführung Blum Tandem NL 480		
Frontschubladen Unterflurführung Blum Movento		
Blum Blumotion Clip top		


POS 4 BADEWANNE

Konstruktion		
Ein eingelassene Badewanne im Wagenträger von Reuter		


AUS 2	Innenausbau 2		
Projekt	Hotelzimmer		
Planverfasser	Schabnam Shor - 883436	Inhalt	Maßstab
Prüfer	Prof. Dipl. Ing. W. Glas	Längsschnitt A-A'	1:20
Assistent	M. A. Jonas Wilhelm	Einbauschränke Schnitt B-B'	1:50
Semester	Sommersemester 2024	Plannummer	Präsentation
		03 // 08	17.07.2024

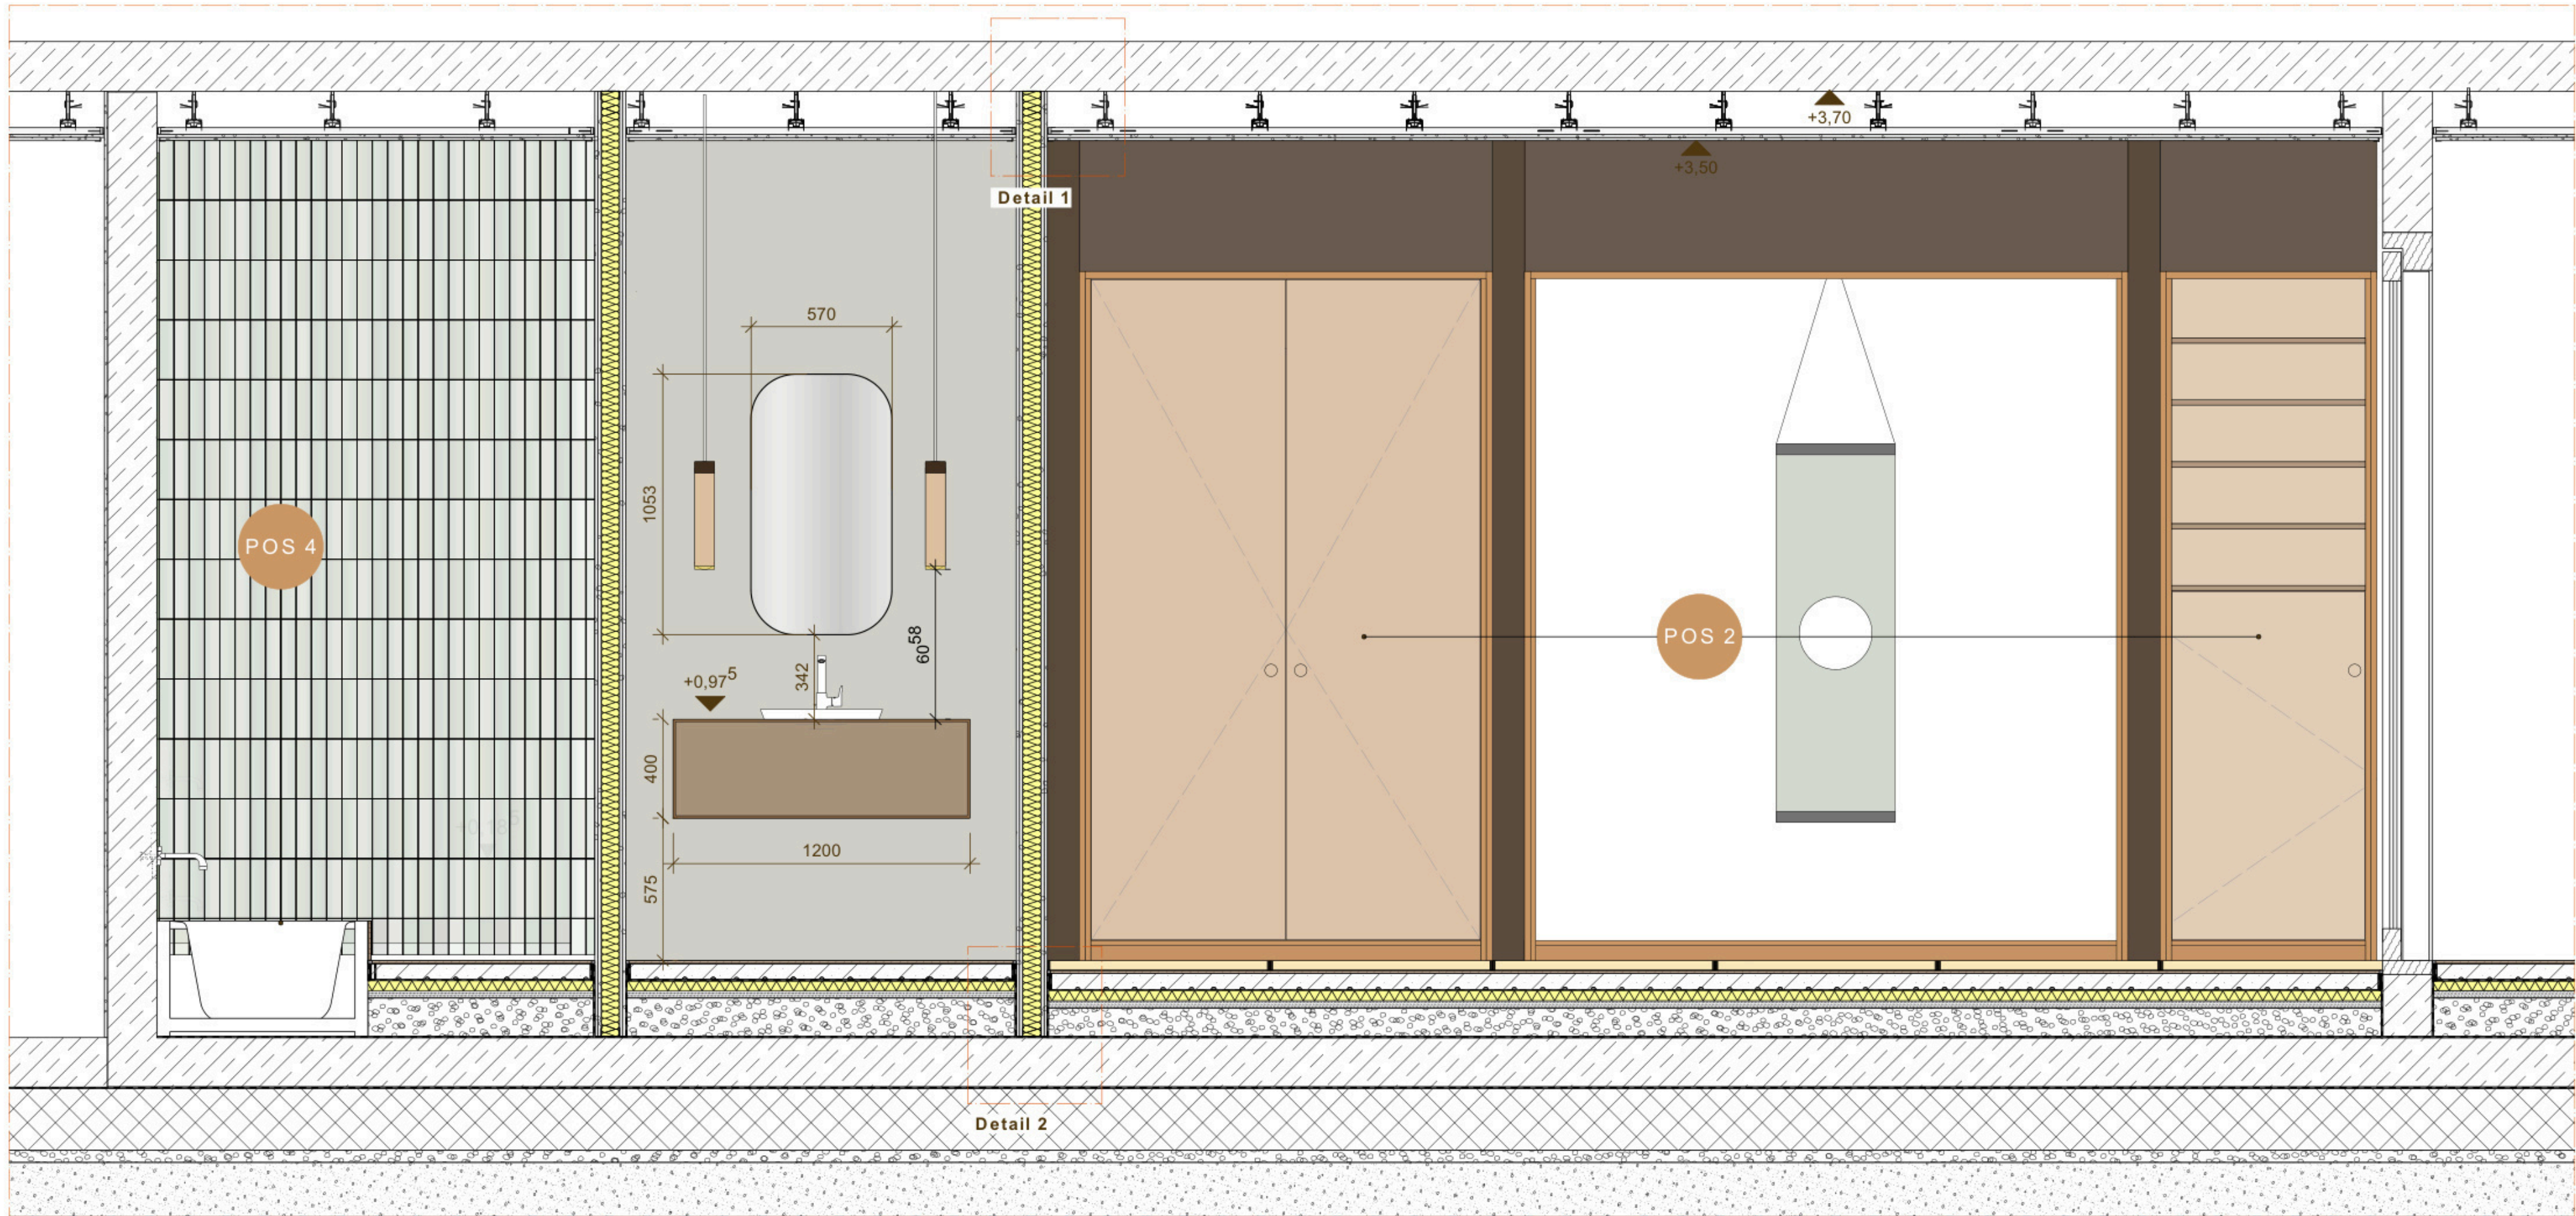

Längsschnitt B-B' M 1:20

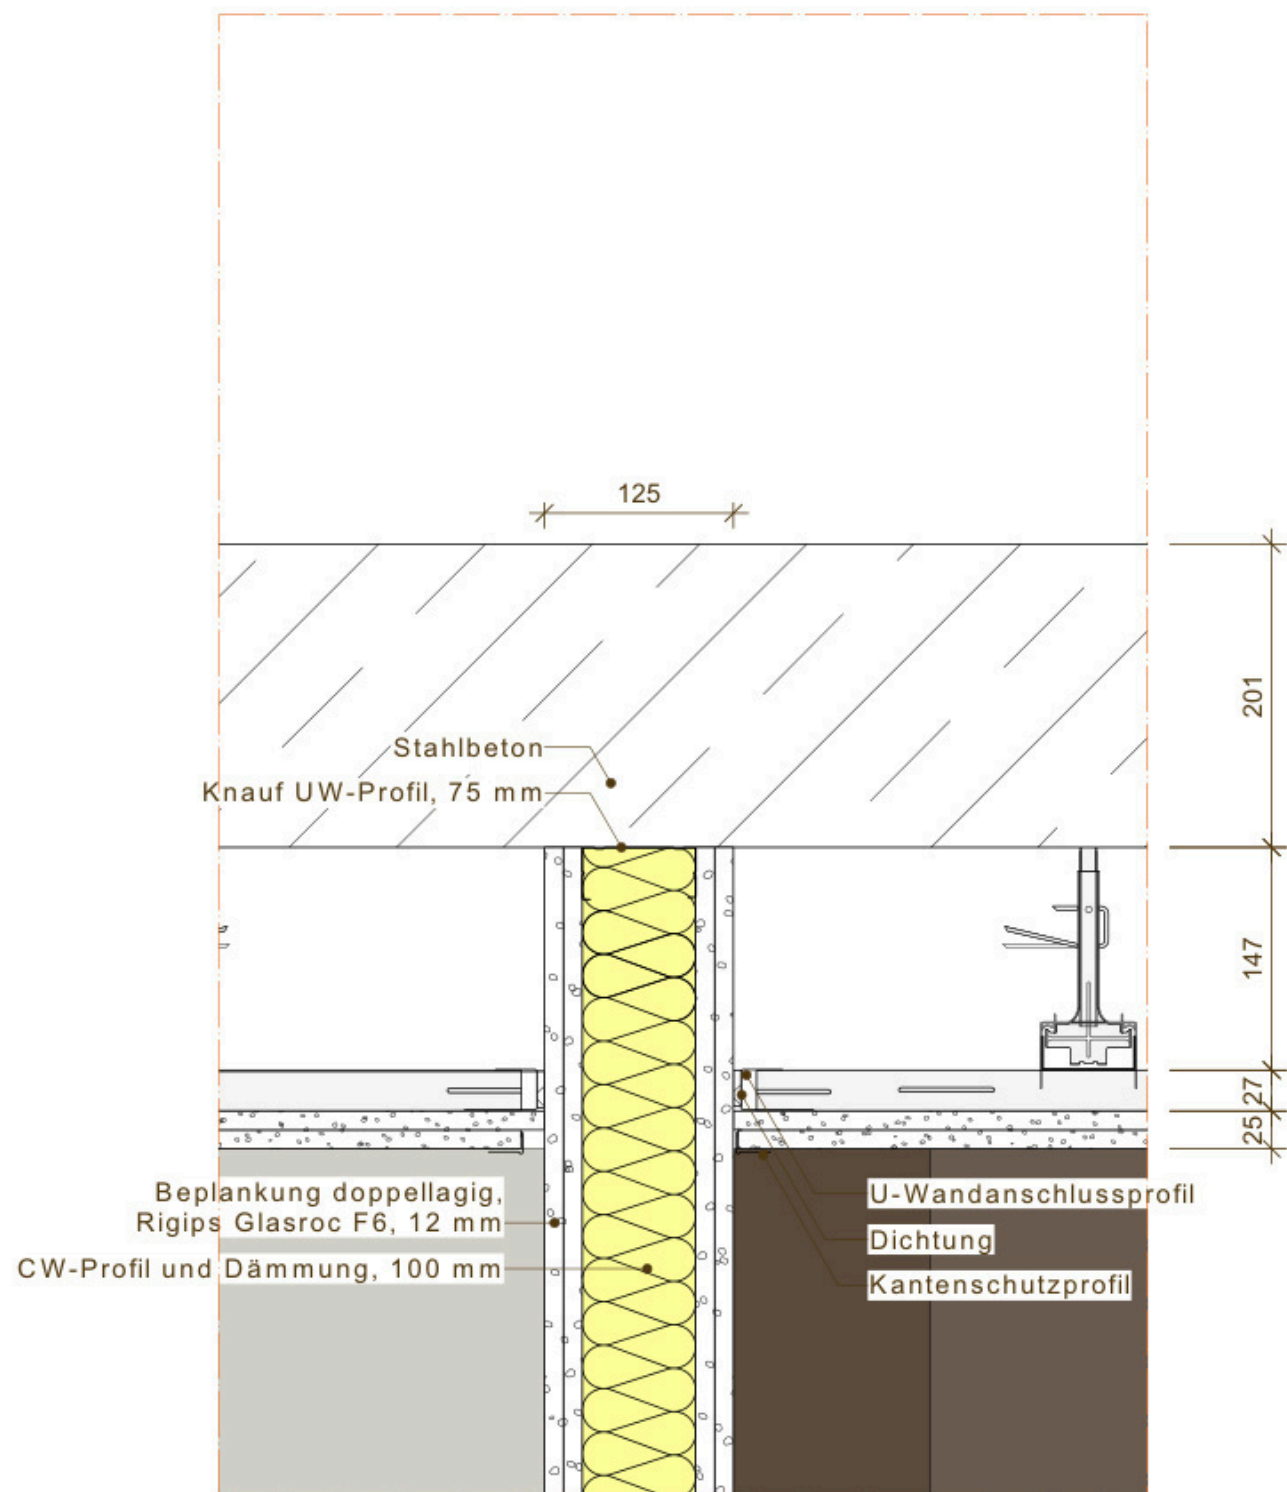

Deckenwandanschluss Detail 1 M 1:5

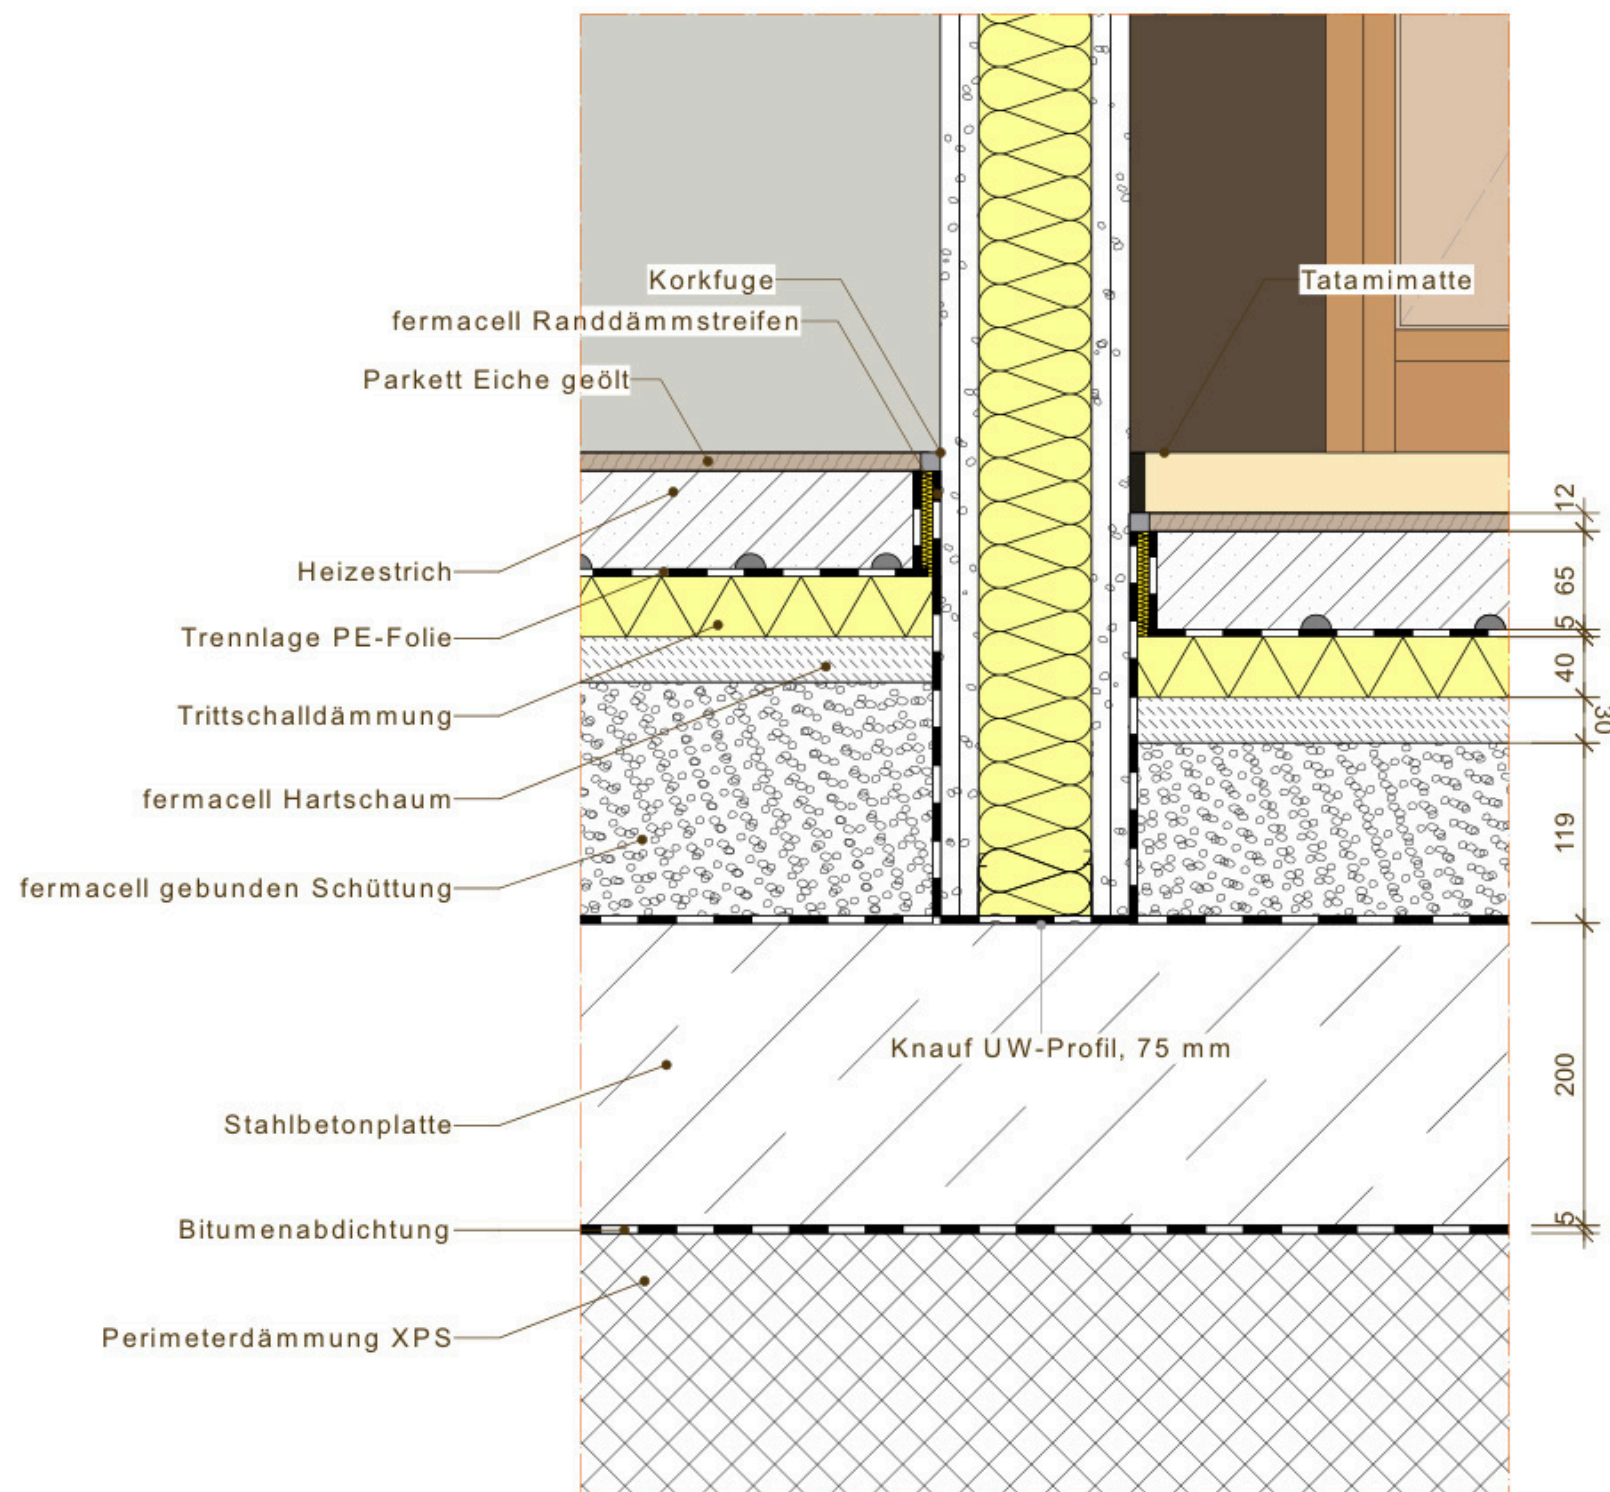

Bodenwandanschluss Detail 1 M 1:5

LEGENDE

BODENAUFBAU

Ohne Erhöhung		
Parkett, Eiche geölt	12	mm
Heizestrich	65	mm
Trennlage PE-Folie	5	mm
Trittschalldämmung	40	mm
Stahlbeton Bodenplatte	200	mm
Bitumen Andichtung	5	mm
Perimeterdämmung XPS	250	mm
Sauberkeitsschicht	50	mm
Erdreich		

Mit Erhöhung		
Tatami Matten	40	mm
Parkett, Eiche geölt	12	mm
Heizestrich	65	mm
Trennlage PE-Folie	5	mm
Trittschalldämmung	40	mm
fermacell Hartschaum	30	mm
fermacell gebundene Schüttung	159	mm
Stahlbeton Bodenplatte	200	mm
Bitumenabdichtung	5	mm
Perimeterdämmung XPS	250	mm
Sauberkeitsschicht	50	mm
Erdreich		

WANDAUFBAU

Tragende Wände	20	mm
Stahlbeton	13	mm
Innenputz Gipsputz		

Trockenbauwand		
Gipskarton	2 x 12,5	mm
Dämmung	75	mm
CW-Profil		
Gipskarton	2 x 12,5	mm
Schiebetürsystem von Knauf Pocket Kit Standard		

Zwischenwände zwischen den Einbauschränken		
Holzbaukonstruktion 50x50 mit OSB-Platten		

DECKENAUFBAU	200	mm
Stahlbetondecke		
Nonius-Abhänger von Knauf		
CD-Profile	2 x 12,5	mm
2 x Gipskarton		

POS 1 TATAMIMATTEN

Konstruktion	900x1800	mm
Kern aus Reisstroh, mit daraufliegender Binsenmatte mit seitlich angenähten Baumwollbändern		

POS 2 TEEKÜCHE

Konstruktion		
Multiplex, Eiche funiert, Messerdeckfunier Eiche geölt		
Beschläge		
Blum Blumotion Clip Top		
Häfele Schleppschanier		
Kühlschrank		
Kühlschrank Minibar Eco 32 Hartmann		


POS 3 EINBAUSCHRÄNKE

Konstruktion		
Multiplex, Eiche funiert, Messerdeckfunier Eiche geölt		
Schubkästen MPX Eiche funiert, Messerdeckfunier Eiche geölt		
Beschläge		
Schubladen im Kleiderschrank Unterflurführung Blum Tandem NL 480		
Frontschubladen Unterflurführung Blum Movento		
Blum Blumotion Clip top		


POS 4 BADEWANNE

Konstruktion		
Ein eingelassene Badewanne im Wagenträger von Reuter		


AUS 2	Innenausbau 2	
Projekt	Hotelzimmer	
Planverfasser	Schabnam Shor - 883436	Inhalt
Prüfer	Prof. Dipl. Ing. W. Glas	Maßstab
Assistent	M. A. Jonas Wilhelm	Längsschnitt B-B' 1:20
		Deckenwandanschluss Detail 1:5
		Bodenwandanschluss Detail 1:5
Semester	Sommersemester 2024	Plannummer 04 // 06
		Präsentation 17.07.2024

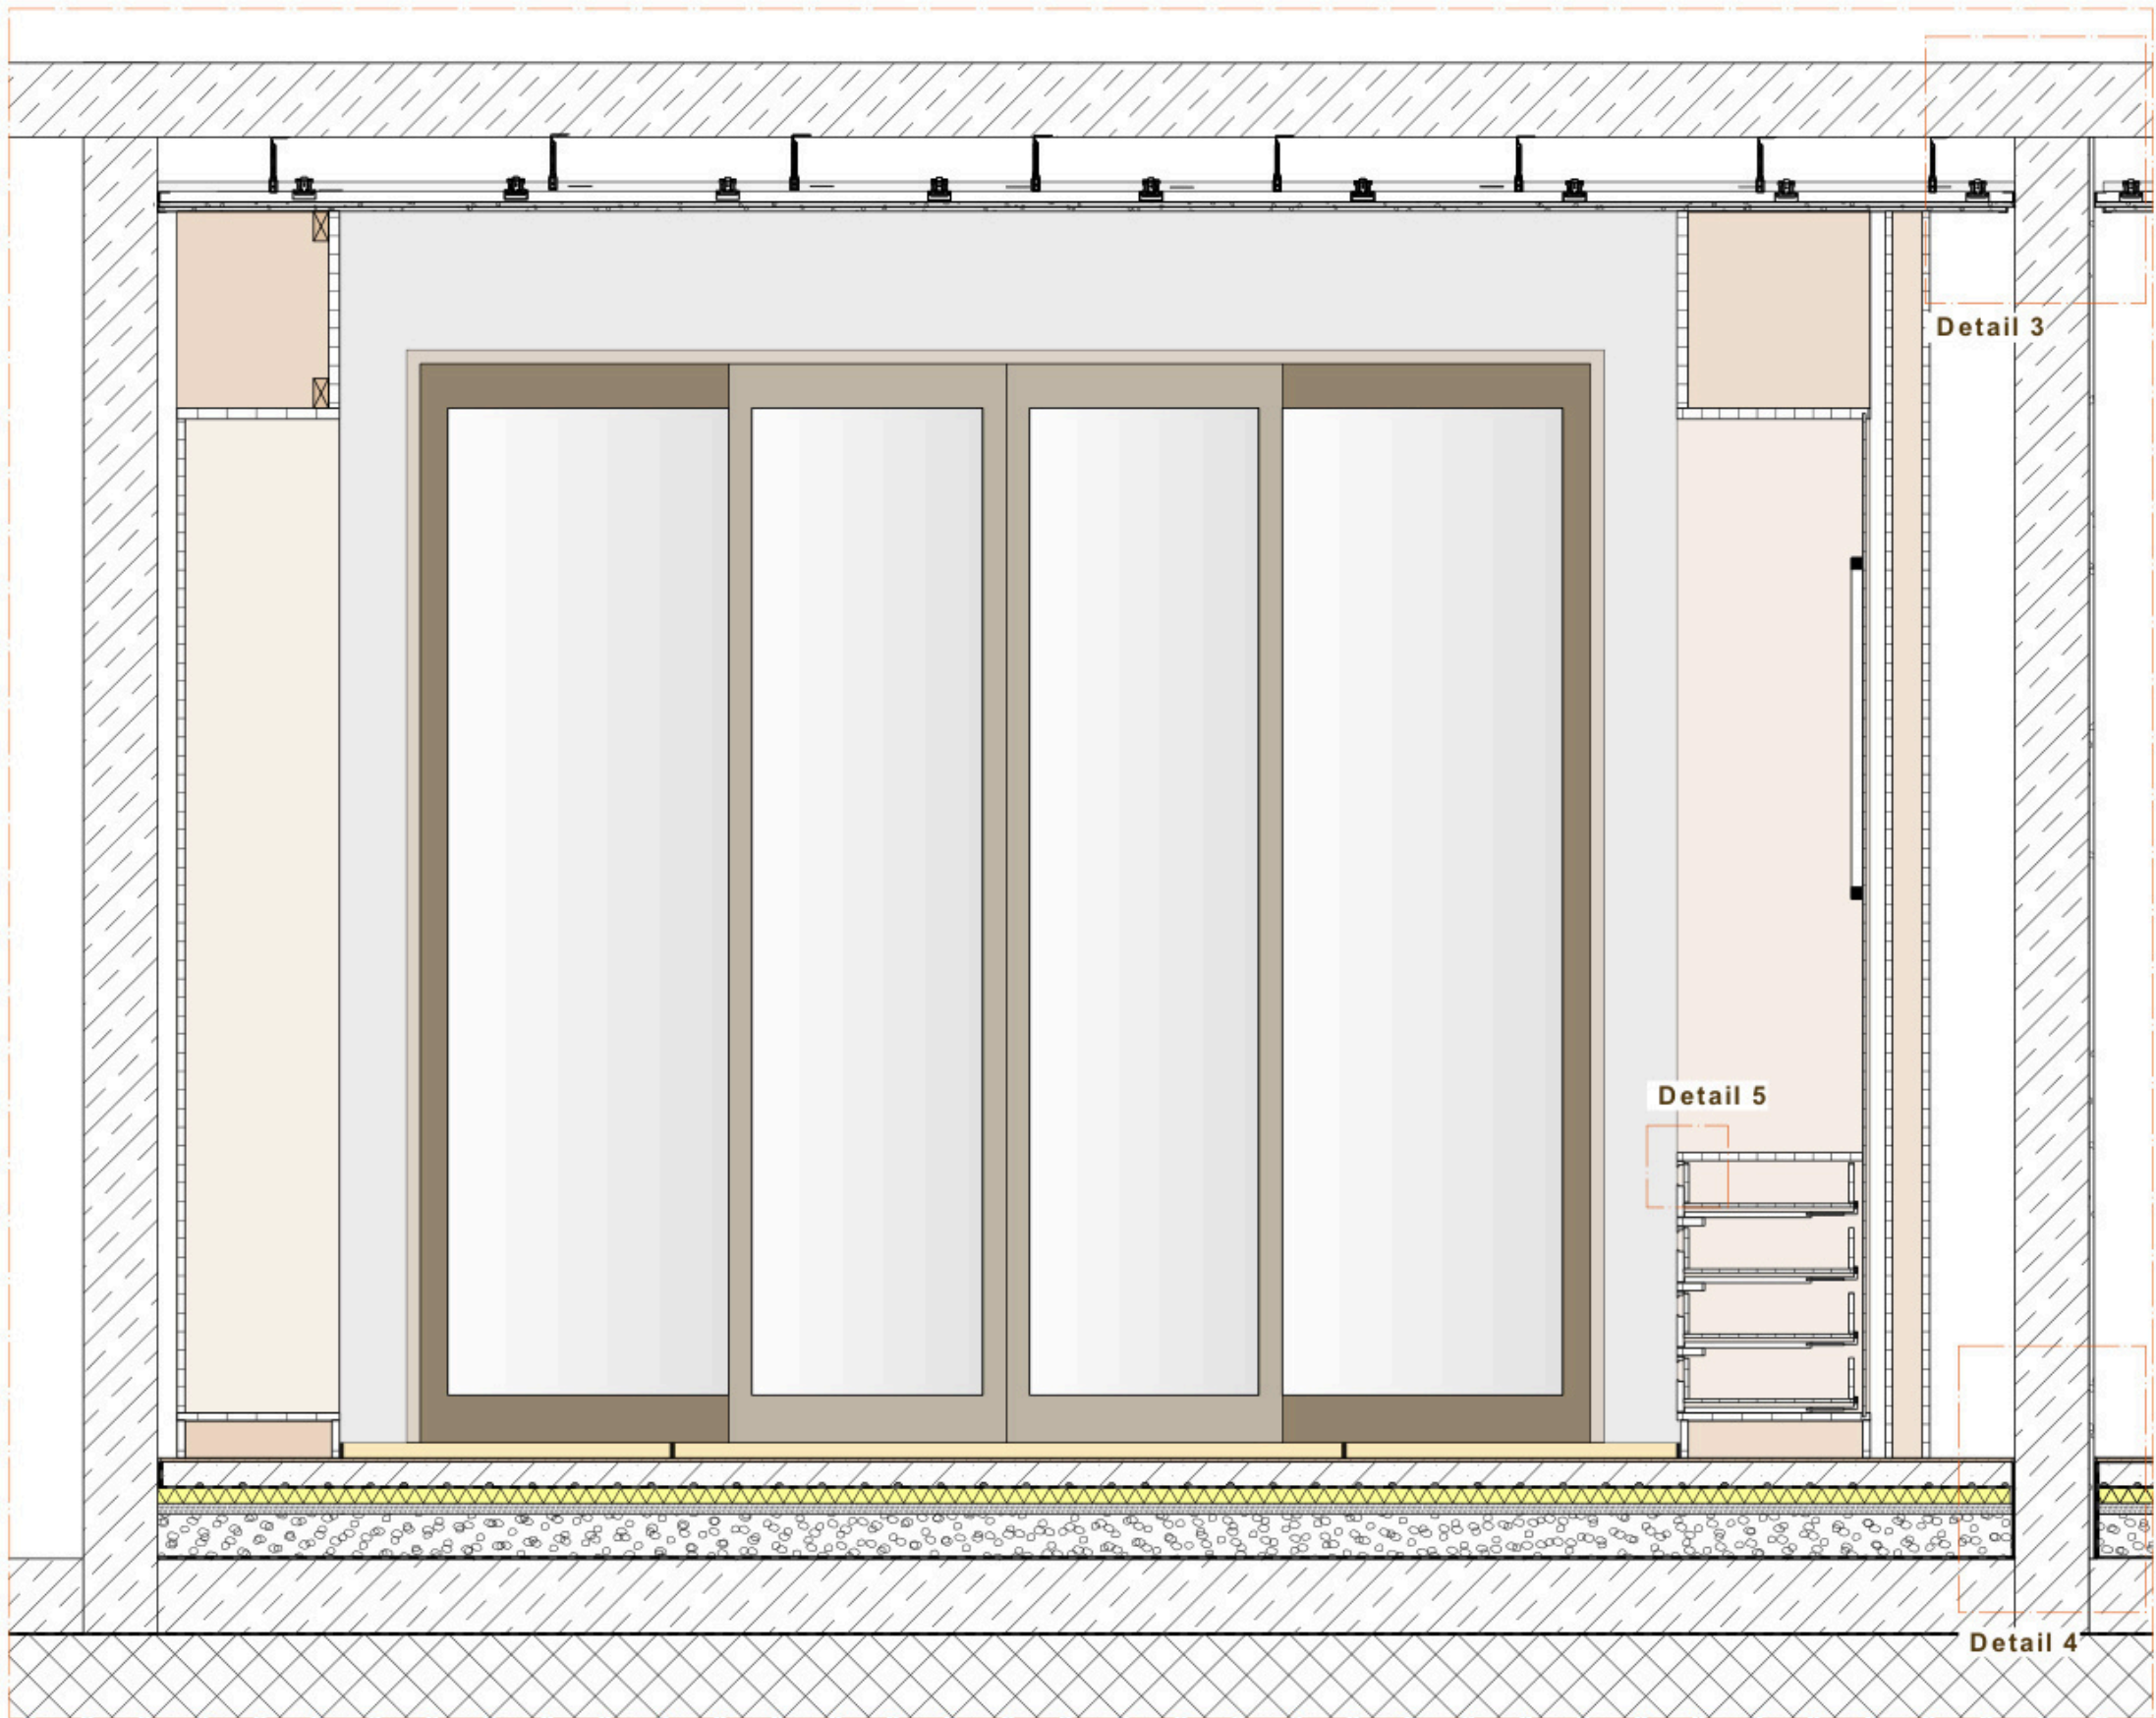


Querschnitt C-C' M 1:20

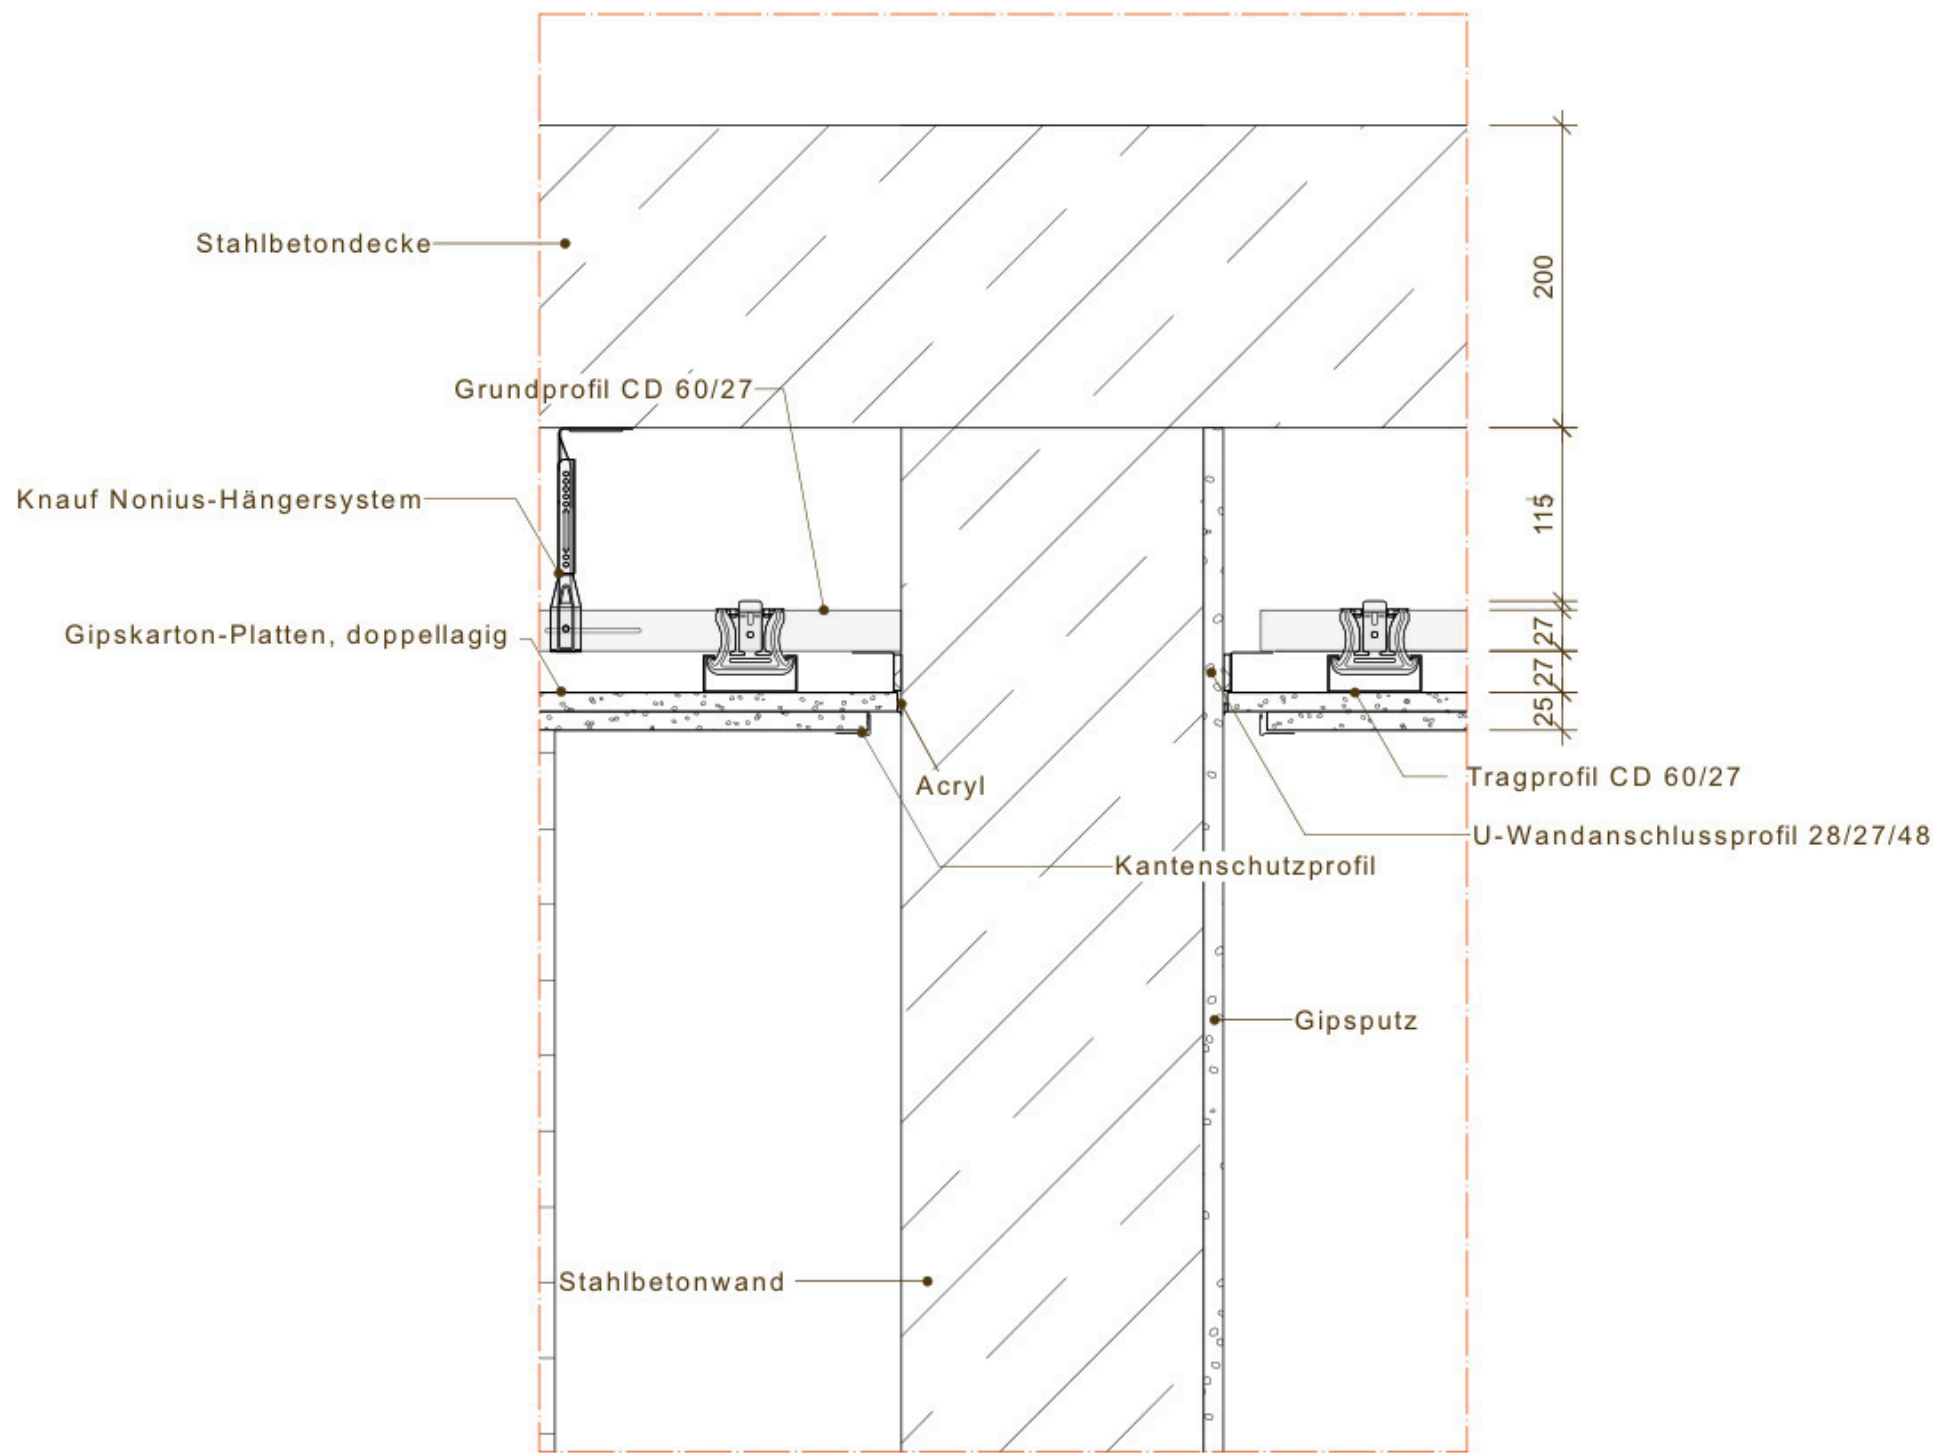


Abgehängte Decke Detail 3 M 1:5

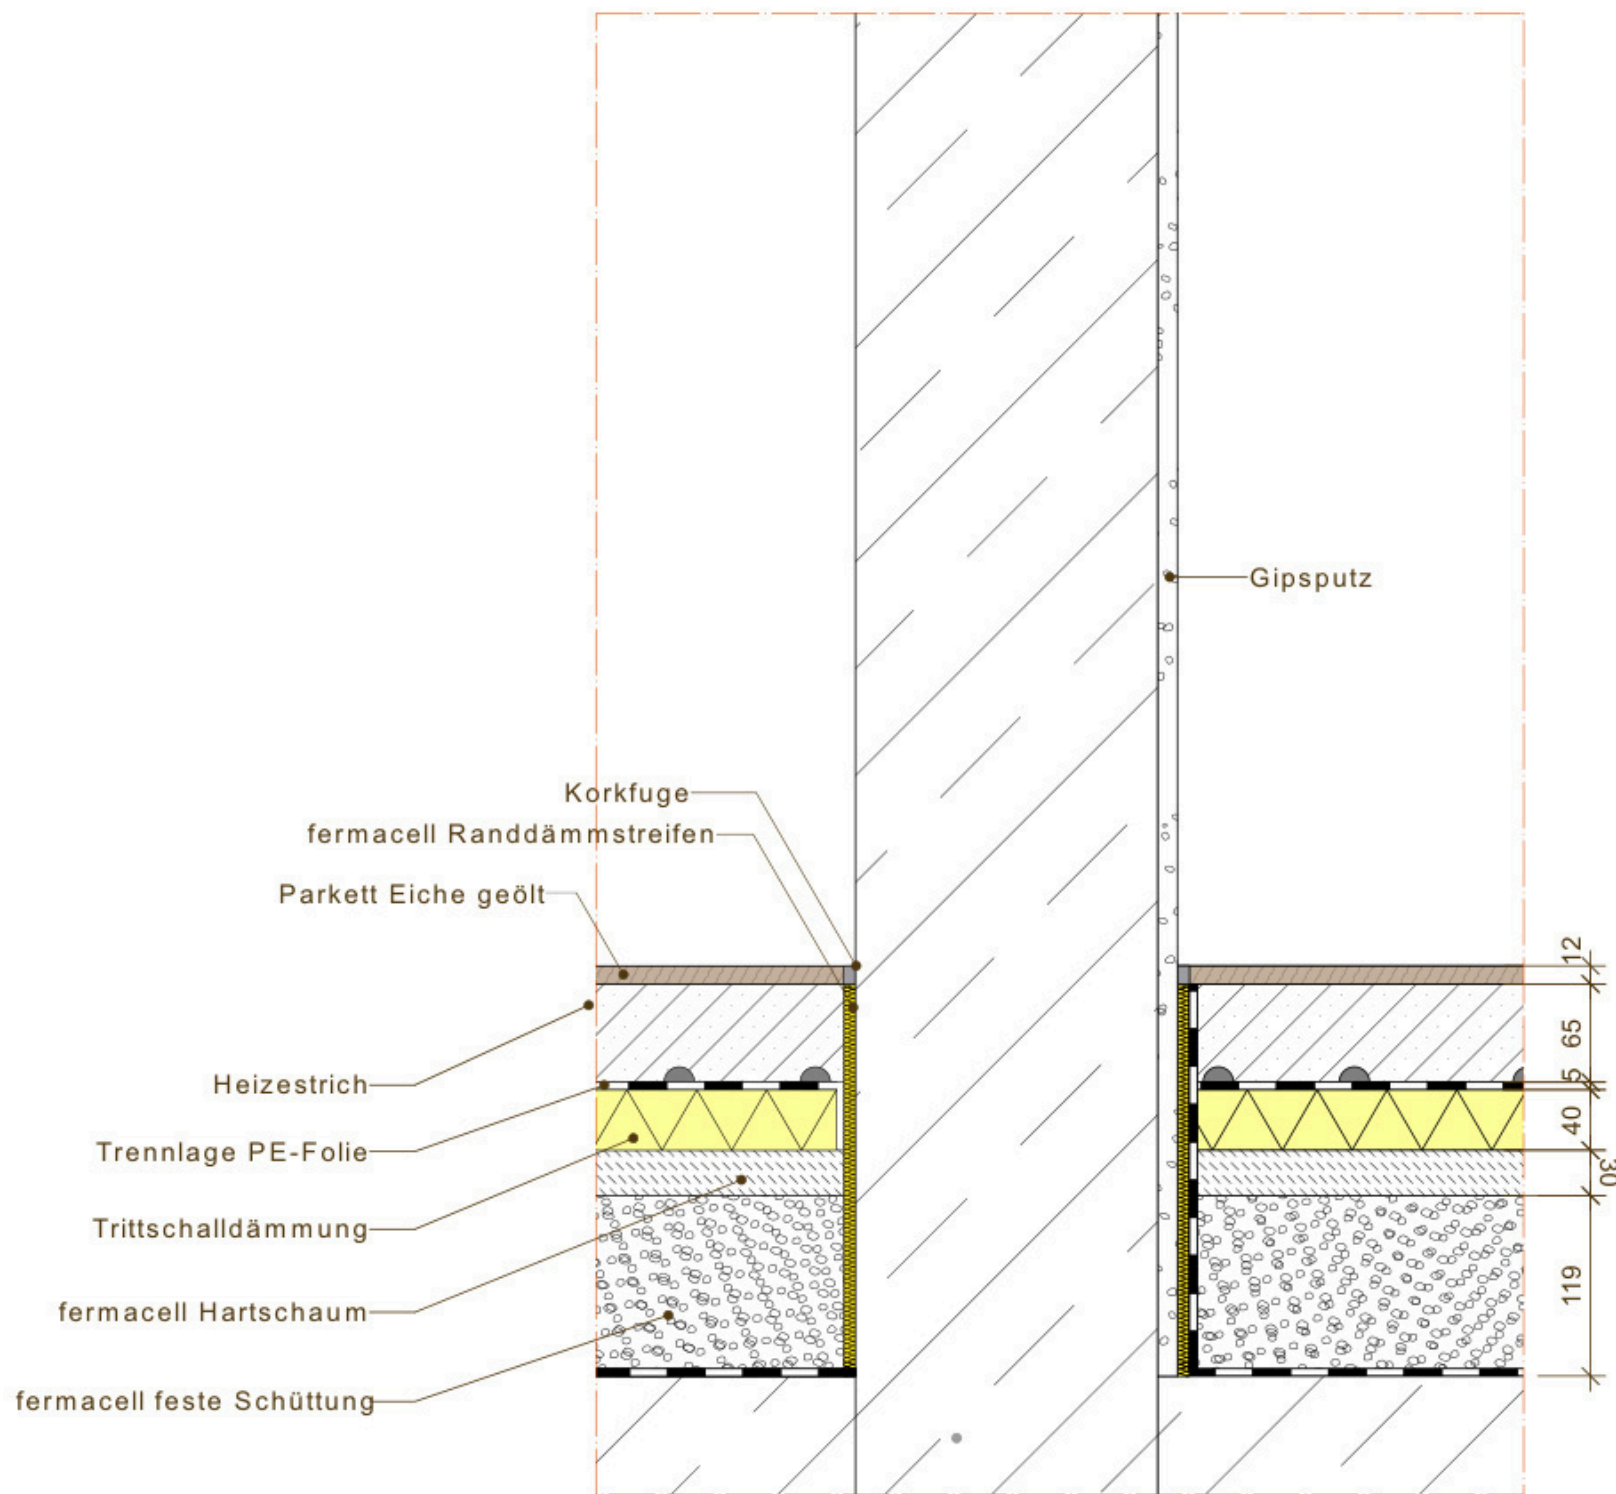

Tragende Wand- Boden Detail 4 M 1:5

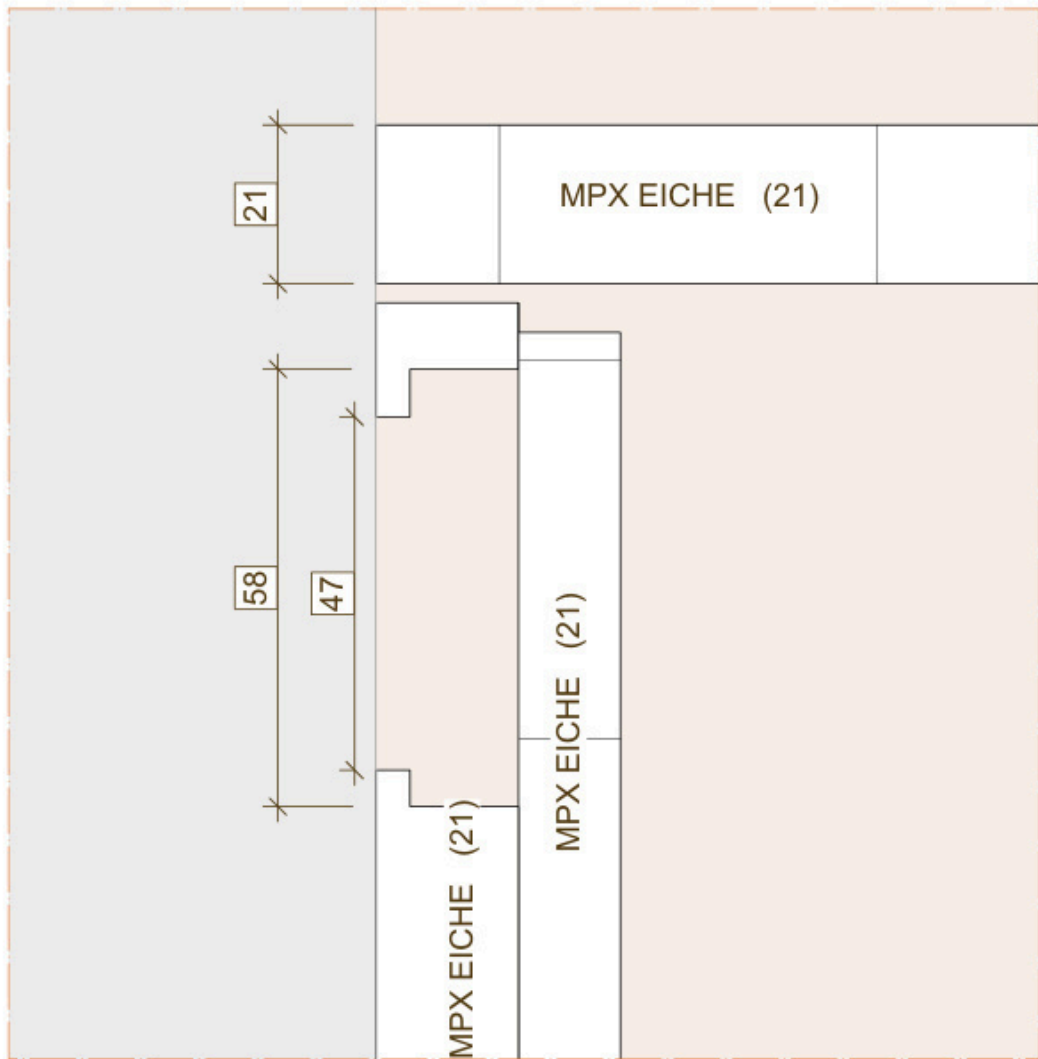

Griffmulde Detail 5 M 1:5

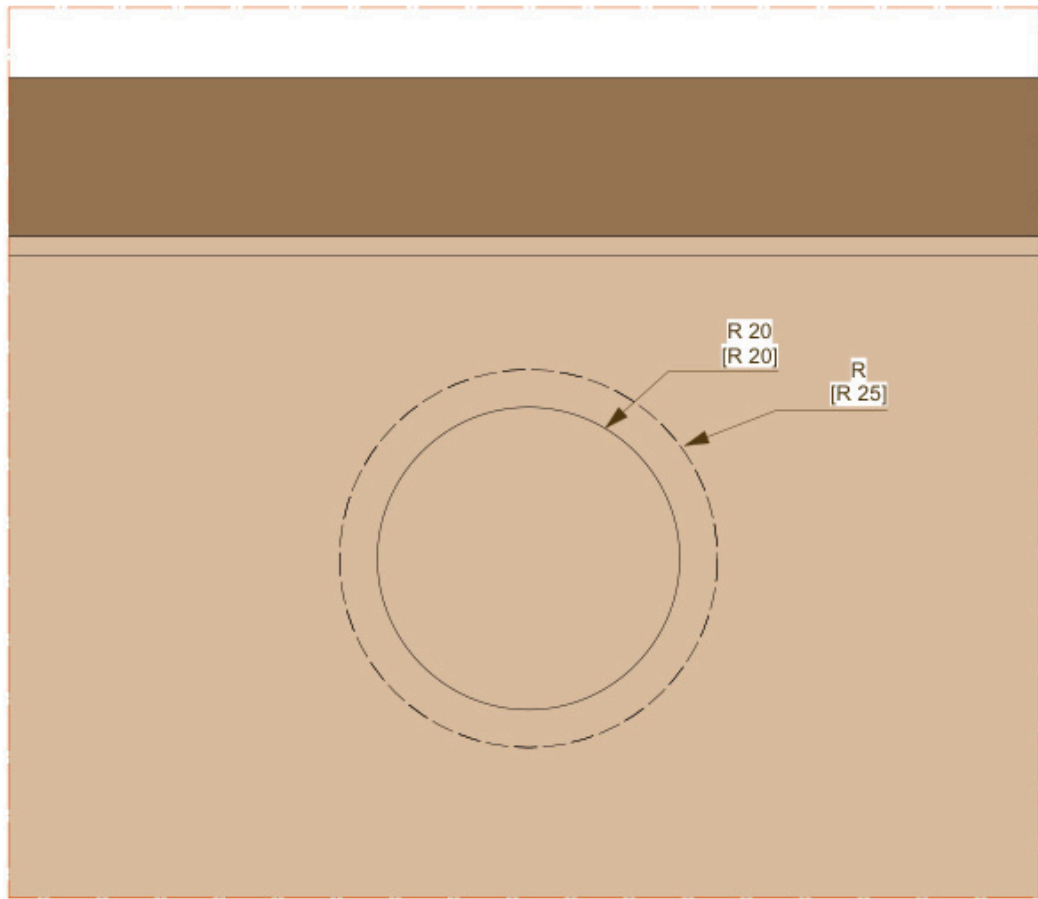

LEGENDE

BODENAUFBAU

Ohne Erhöhung		
Parkett, Eiche geölt	12	mm
Heizestrich	65	mm
Trennlage PE-Folie	5	mm
Trittschalldämmung	40	mm
Stahlbeton Bodenplatte	200	mm
Bitumen Andichtung	5	mm
Perimeterdämmung XPS	250	mm
Sauberkeitsschicht	50	mm
Erdreich		
Mit Erhöhung		
Tatami Matten	40	mm
Parkett, Eiche geölt	12	mm
Heizestrich	65	mm
Trennlage PE-Folie	5	mm
Trittschalldämmung	40	mm
fermacell Hartschaum	30	mm
fermacell gebundene Schüttung	159	mm
Stahlbeton Bodenplatte	200	mm
Bitumenabdichtung	5	mm
Perimeterdämmung XPS	250	mm
Sauberkeitsschicht	50	mm
Erdreich		

WANDAUFB AU

Tragende Wände	20	mm
Stahlbeton	13	mm
Innenputz Gipsputz		

Trockenbauwand

Gipskarton	2 x 12,5	mm
Dämmung	75	mm
CW-Profil		
Gipskarton	2 x 12,5	mm
Schiebetürsystem von Knauf Pocket Kit Standard		

Zwischenwände zwischen den Einbauschränken
Holzbaukonstruktion 50x50 mit OSB-Platten

DECKENAUFBAU

Stahlbetondecke	200	mm
Nonius-Abhänger von Knauf		
CD-Profile	2 x 12,5	mm
2 x Gipskarton		

POS 1 TATAMIMATTEN

Konstruktion	900x1800	mm
Kern aus Reisstroh, mit daraufliegender Binsenmatte mit seitlich angenähten Baumwollbändern		

POS 2 TEEKÜCHE

Konstruktion
Multiplex, Eiche funiert, Messerdeckfunier Eiche geölt
Beschläge
Blum Blumotion Clip Top
Häfele Schleppschanier
Kühlschrank
Kühlschrank Minibar Eco 32 Hartmann


POS 3 EINBAUSCHRÄNKE

Konstruktion
Multiplex, Eiche funiert, Messerdeckfunier Eiche geölt
Schubkästen MPX Eiche funiert, Messerdeckfunier Eiche geölt
Beschläge
Schubladen im Kleiderschrank Unterflurführung Blum Tandem NL 480
Frontschubladen Unterflurführung Blum Movento
Blum Blumotion Clip top

POS 4 BADEWANNE

Konstruktion
Eingelassene Badewanne im Wagenträger von Reuter

AUS 2	Innenausbau 2	
Projekt	Hotelzimmer	
Planverfasser	Schabnam Shor - 883436	Inhalt
Prüfer	Prof. Dipl. Ing. W. Glas	Maßstab
Assistent	M. A. Jonas Wilhelm	Querschnitt C-C' 1:20
		Abgehängte Decke Detail 3 1:5
		Tragende Wand Boden Detail 4 1:5
		Griffmulde Detail 5 1:5
Semester	Sommersemester 2024	Plannummer 05 // 08
		Präsentation 17.07.2024

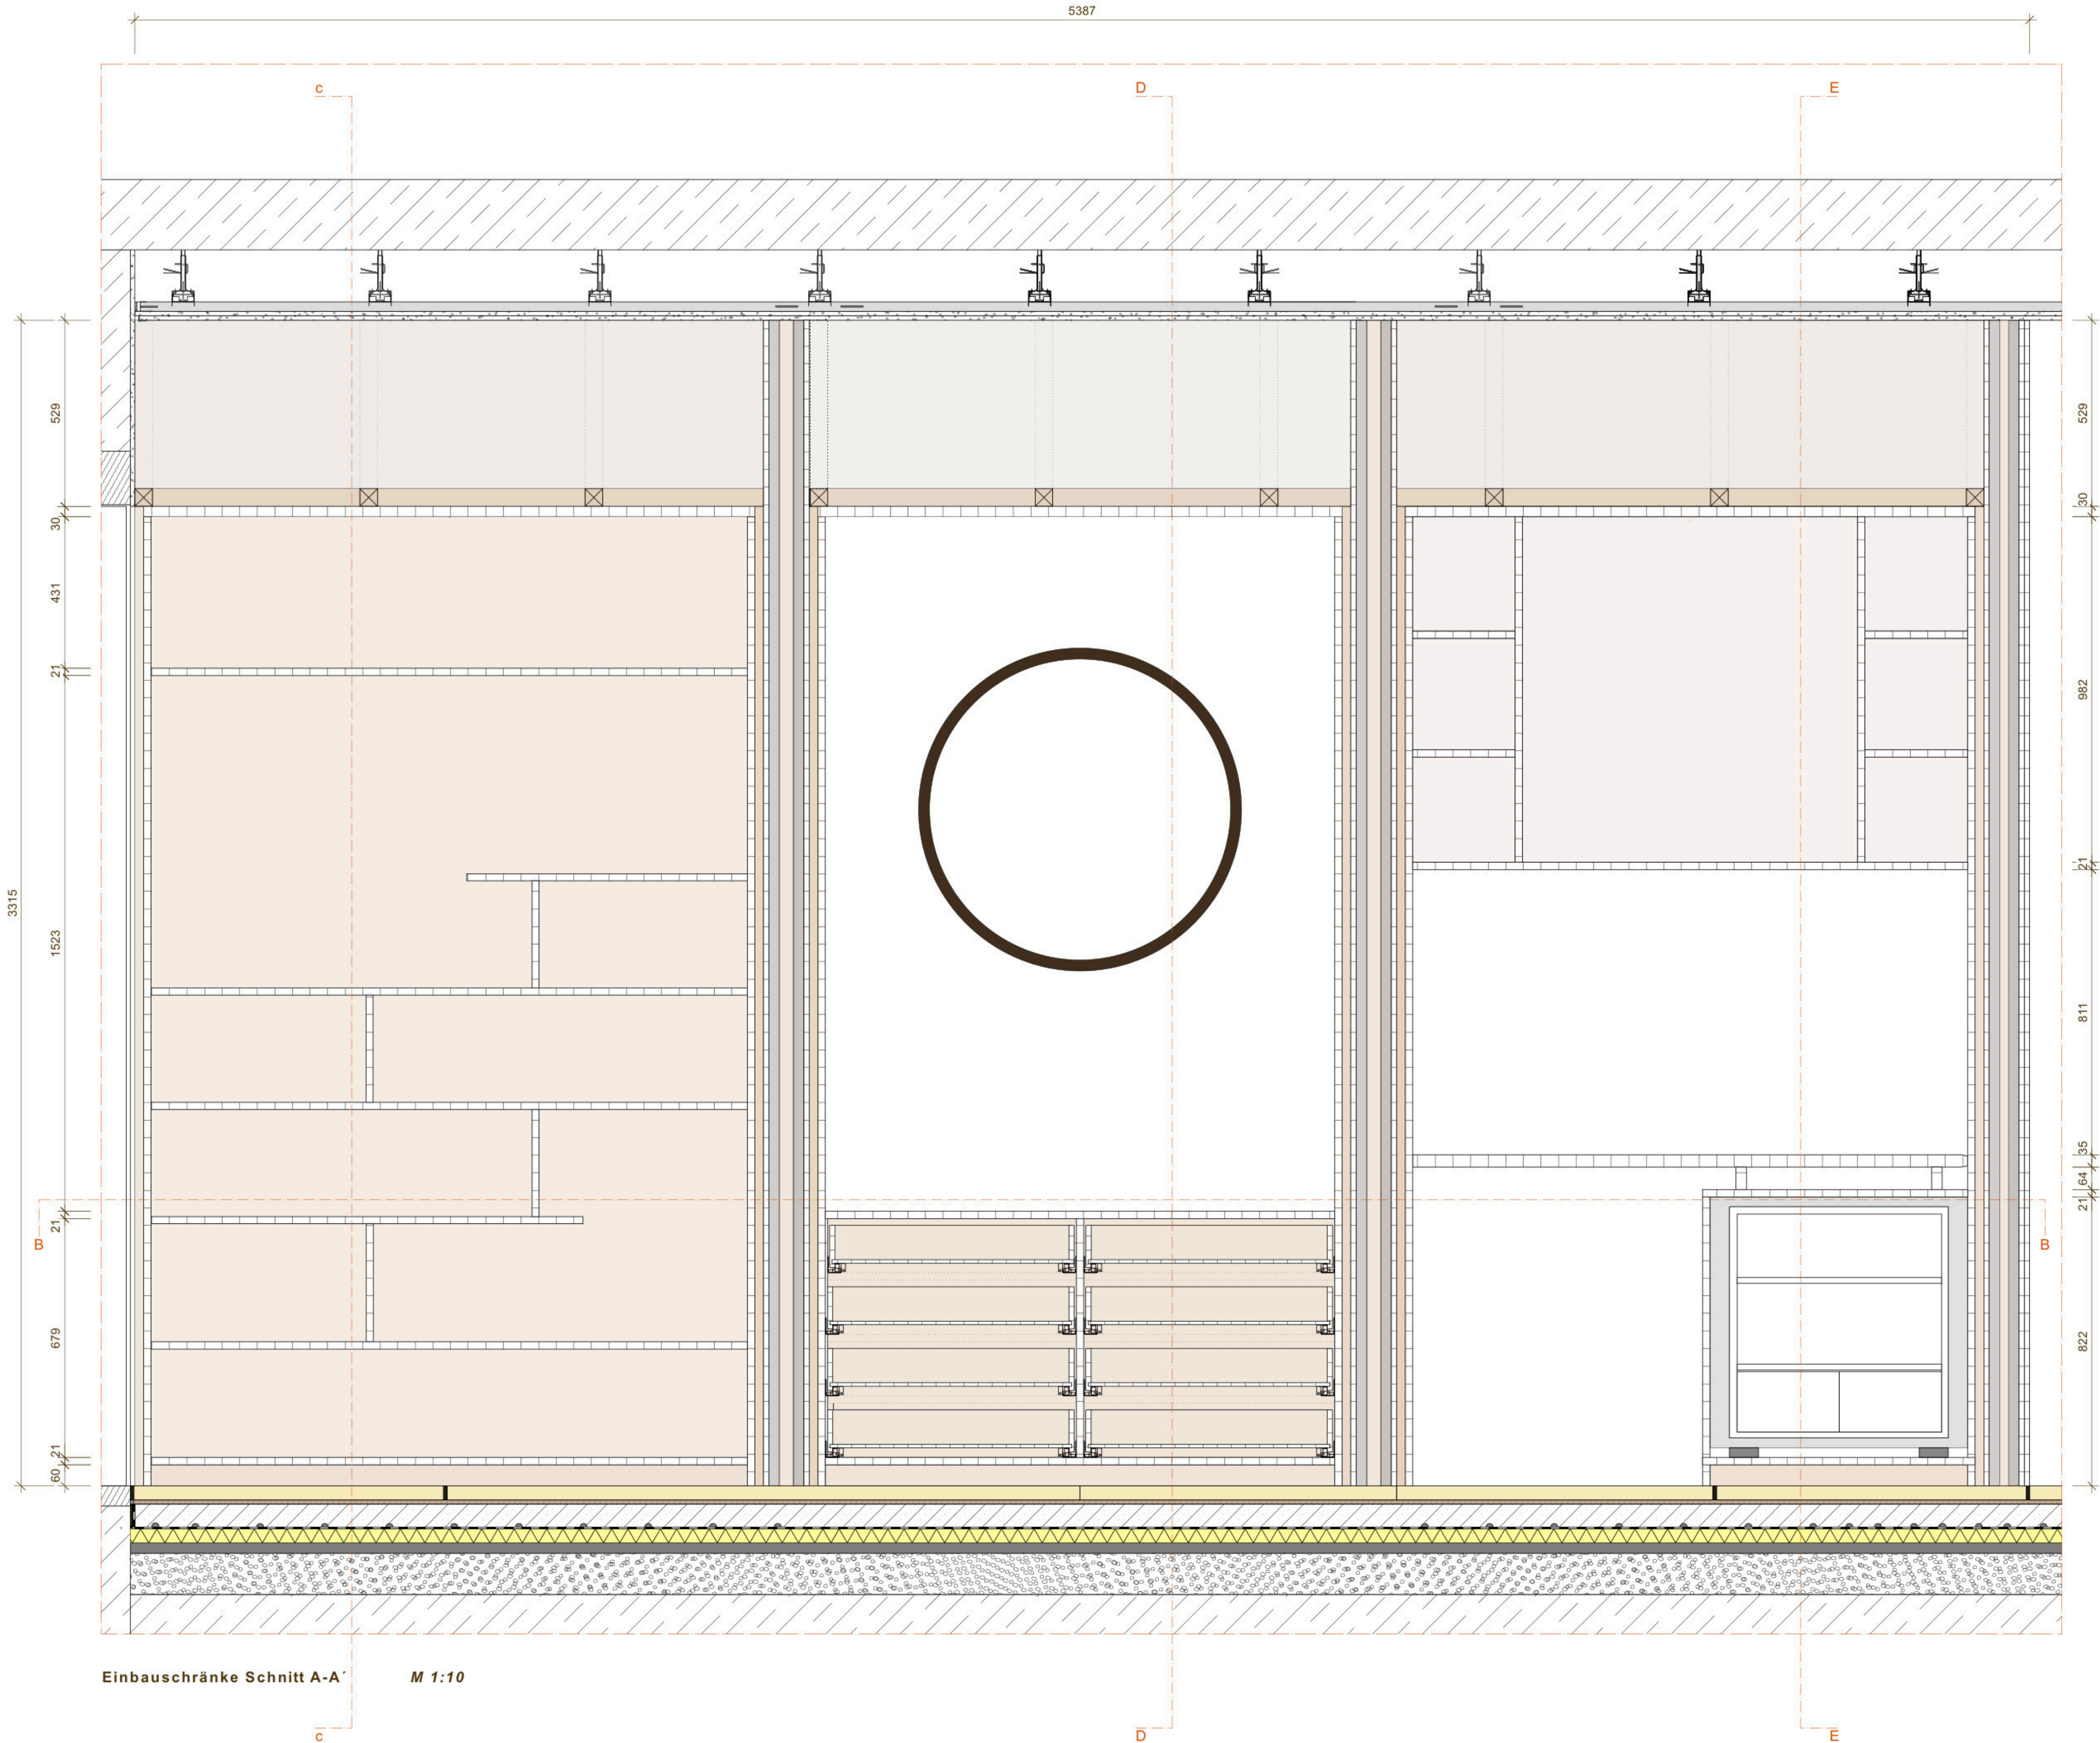

LEGENDE

BODENAUFBAU

Ohne Erhöhung		
Parkett, Eiche geölt	12	mm
Heizestrich	65	mm
Trennlage PE-Folie	5	mm
Trittschalldämmung	40	mm
Stahlbeton Bodenplatte	200	mm
Bitumen Andichtung	5	mm
Perimeterdämmung XPS	250	mm
Sauberkeitsschicht	50	mm
Erdreich		

Mit Erhöhung		
Tatami Matten	40	mm
Parkett, Eiche geölt	12	mm
Heizestrich	65	mm
Trennlage PE-Folie	5	mm
Trittschalldämmung	40	mm
fermacell Hartschaum	30	mm
fermacell gebundene Schüttung	159	mm
Stahlbeton Bodenplatte	200	mm
Bitumenabdichtung	5	mm
Perimeterdämmung XPS	250	mm
Sauberkeitsschicht	50	mm
Erdreich		

WANDAUFBAU

Tragende Wände		
Stahlbeton	20	mm
Innenputz Gipsputz	13	mm

Trockenbauwand		
Gipskarton	2 x 12,5	mm
Dämmung	75	mm
CW-Profil		
Gipskarton	2 x 12,5	mm
Schiebetürsystem von Knauf Pocket Kit Standard		

Zwischenwände zwischen den Einbauschränken		
Holzbaukonstruktion 50x50 mit OSB-Platten		

DECKENAUFBAU		200 mm
Stahlbetondecke		
Nonius-Abhänger von Knauf		
CD-Profile	2 x 12,5	mm
2 x Gipskarton		

POS 1 TATAMIMATTEN		
Konstruktion	900x1800	mm
Kern aus Reisstroh, mit daraufliegender Binsenmatte mit seitlich angenähten Baumwollbändern		

POS 2 TEEKÜCHE		
Konstruktion		
Multiplex, Eiche funiert, Messerdeckfunier Eiche geölt		
Beschläge		
Blum Blumotion Clip Top		
Häfele Schleppschanier		
Kühlschrank		
Kühlschrank Minibar Eco 32 Hartmann		

POS 3 EINBAUSCHRÄNKE		
Konstruktion		
Multiplex, Eiche funiert, Messerdeckfunier Eiche geölt		
Schubkästen MPX Eiche funiert, Messerdeckfunier Eiche geölt		
Beschläge		
Schubladen im Kleiderschrank Unterflurführung Blum Tandem NL 480		
Frontschubladen Unterflurführung Blum Movento		
Blum Blumotion Clip top		


POS 4 BADEWANNE		
Konstruktion		
Eingelassene Badewanne im Wagenträger von Reuter		

AUS 2	Innenausbau 2		
Projekt	Hotelzimmer		
Planverfasser	Schabnam Shor - 883436	Inhalt	Maßstab
		Einbauschränk Schnitt A-A'	1:10
Prüfer	Prof. Dipl. Ing. W. Glas		
Assistent	M. A. Jonas Wilhelm		
Semester	Sommersemester 2024	Plannummer	Präsentation
		06 // 08	17.07.2024




POS 4 BADEWANNE
Konstruktion
 Eingelassene Badewanne im Wagenträger von Reuter


AUS 2 Innenausbau 2	
Projekt Hotelzimmer	
Planverfasser Schabnam Shor - 883436	Inhalt Einbauschränke Schnitt C-C´ Einbauschränke Schnitt D-D´ Einbauschränke Schnitt E-E´
Prüfer Prof. Dipl. Ing. W. Glas	1:1 1:1 1:1
Assistent M. A. Jonas Wilhelm	
Semester Sommersemester 2024	Plannummer 07 // 08
	Präsentation 17.07.2024

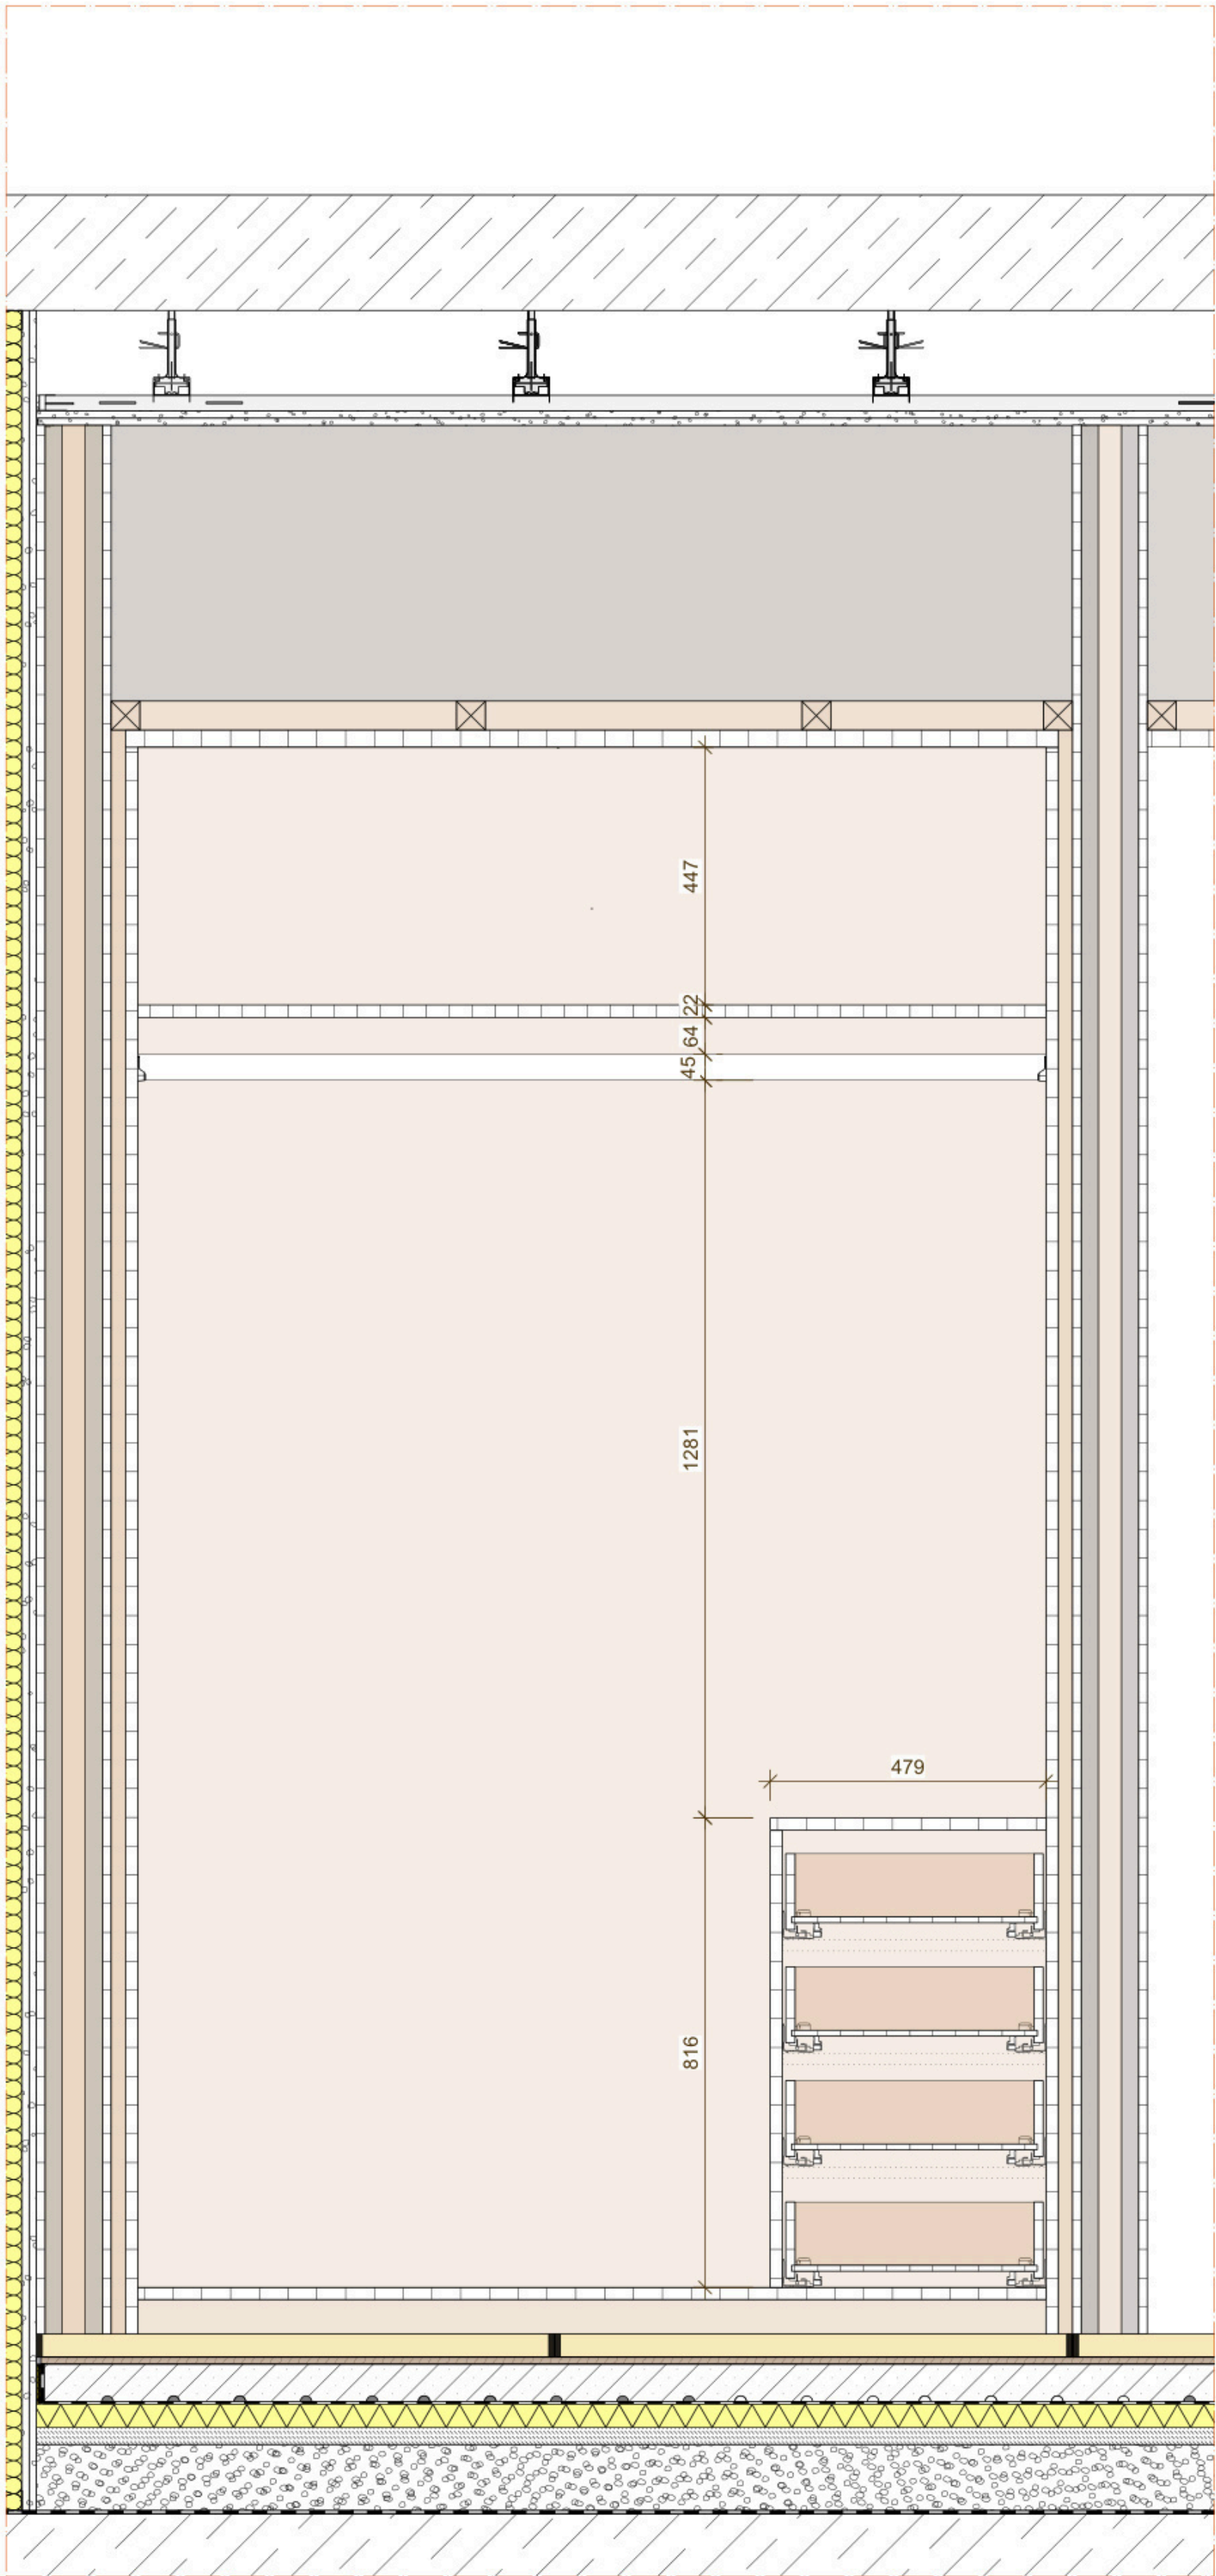


Einbauschränke Schnitt F-F' M 1:10

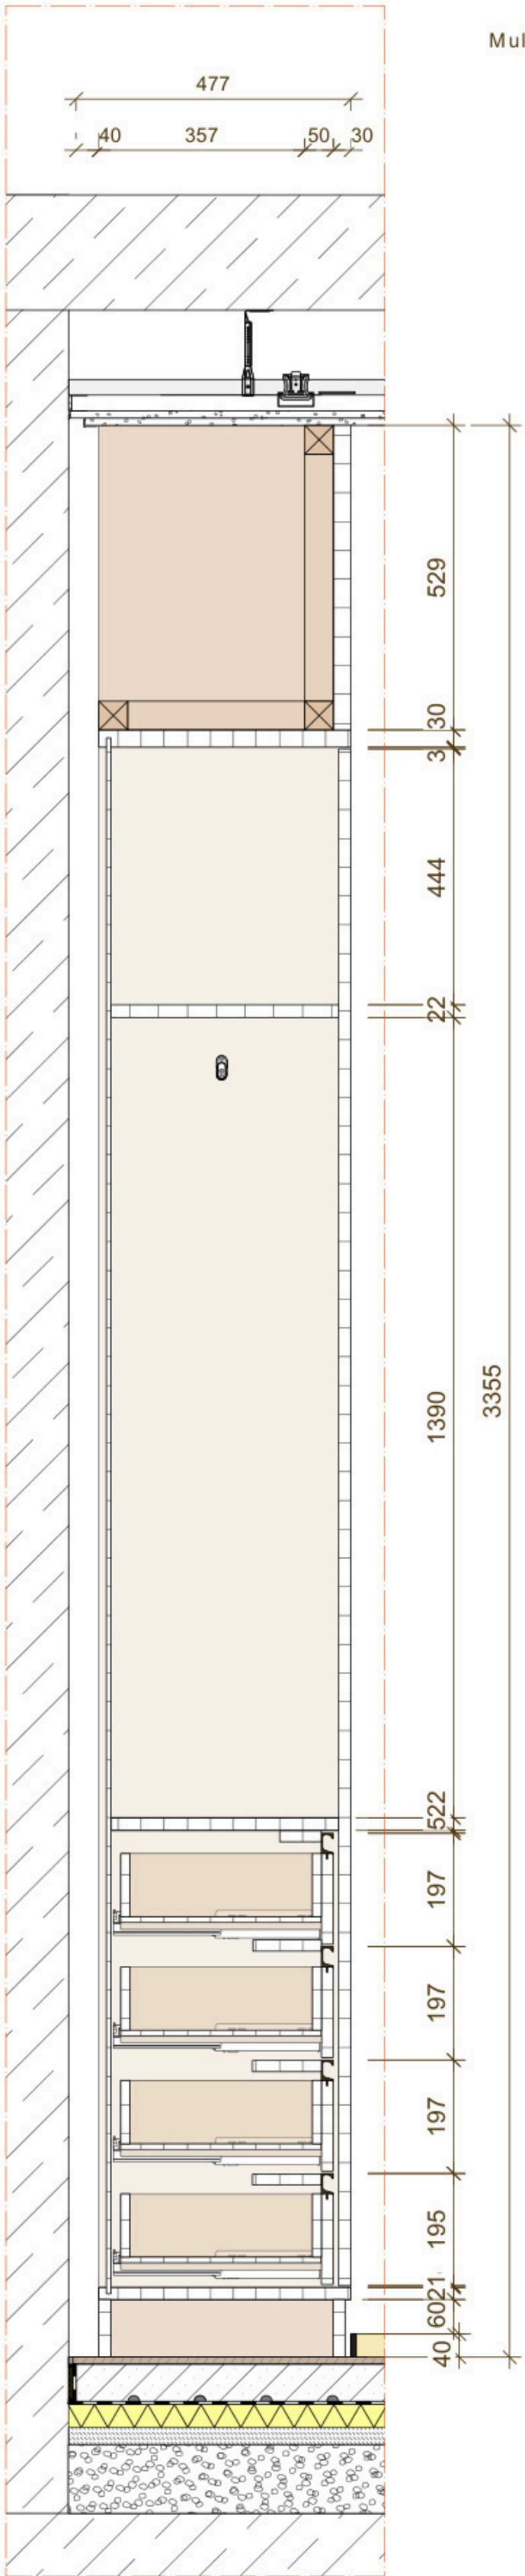


Einbauschränke Schnitt G-G' M 1:10

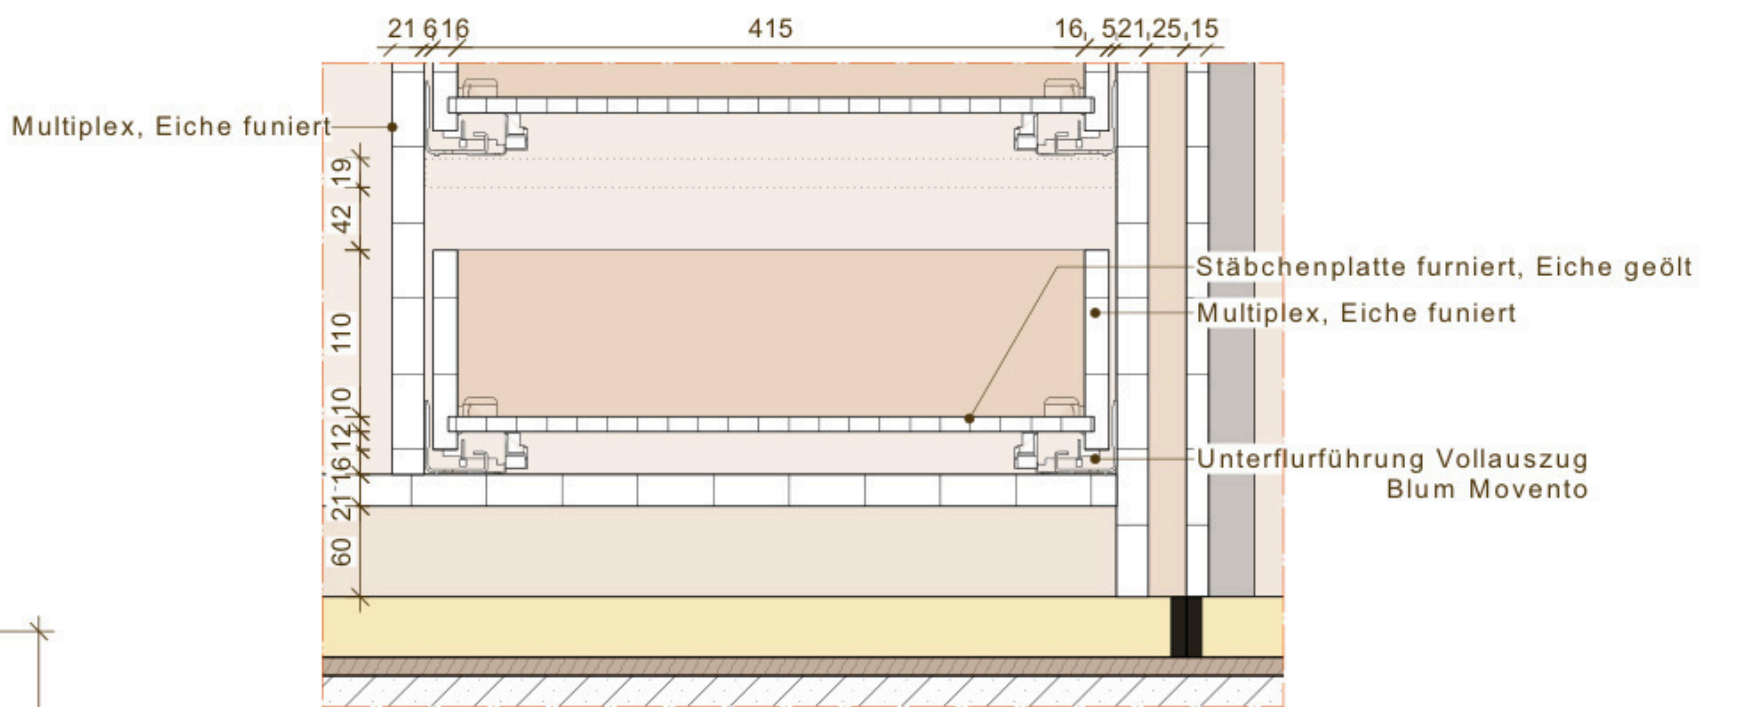


Schubladen Detail 6 M 1:5

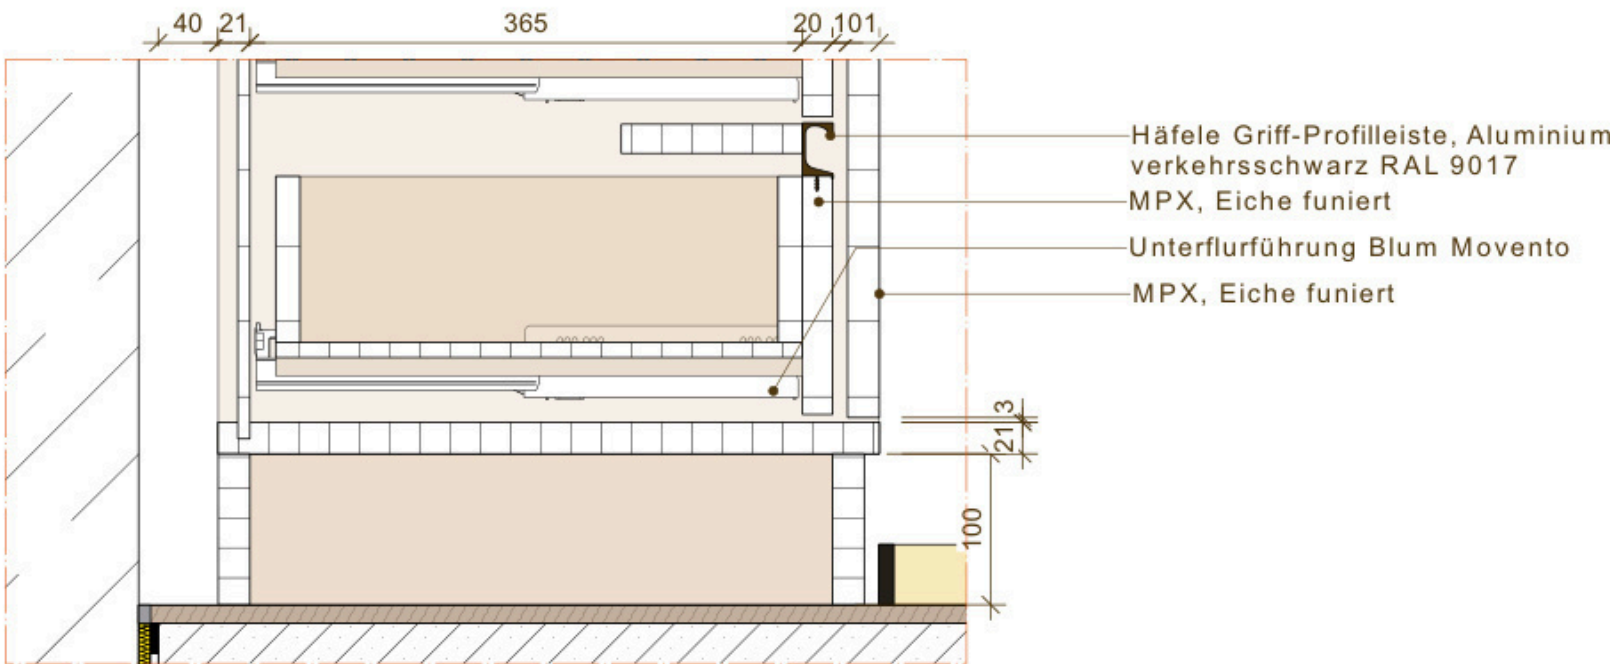

Sockel Detail 7 M 1:5

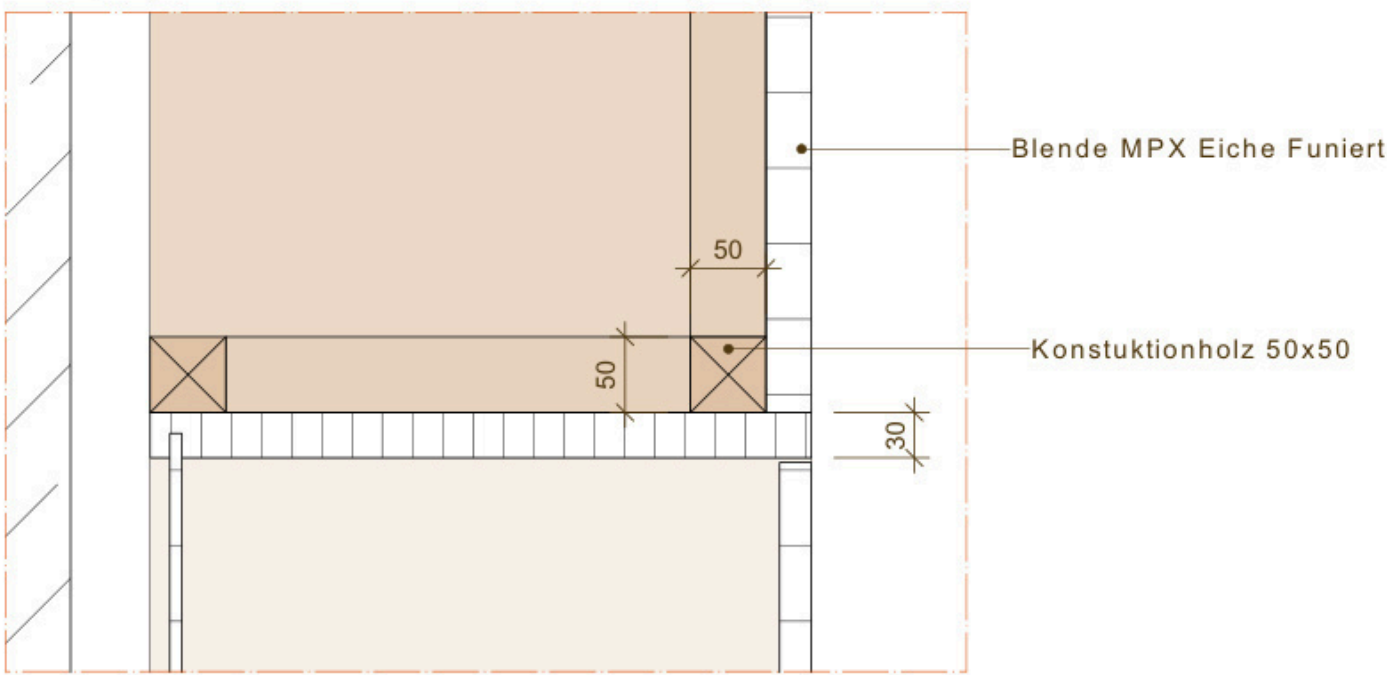

Blende Detail 8 M 1:5

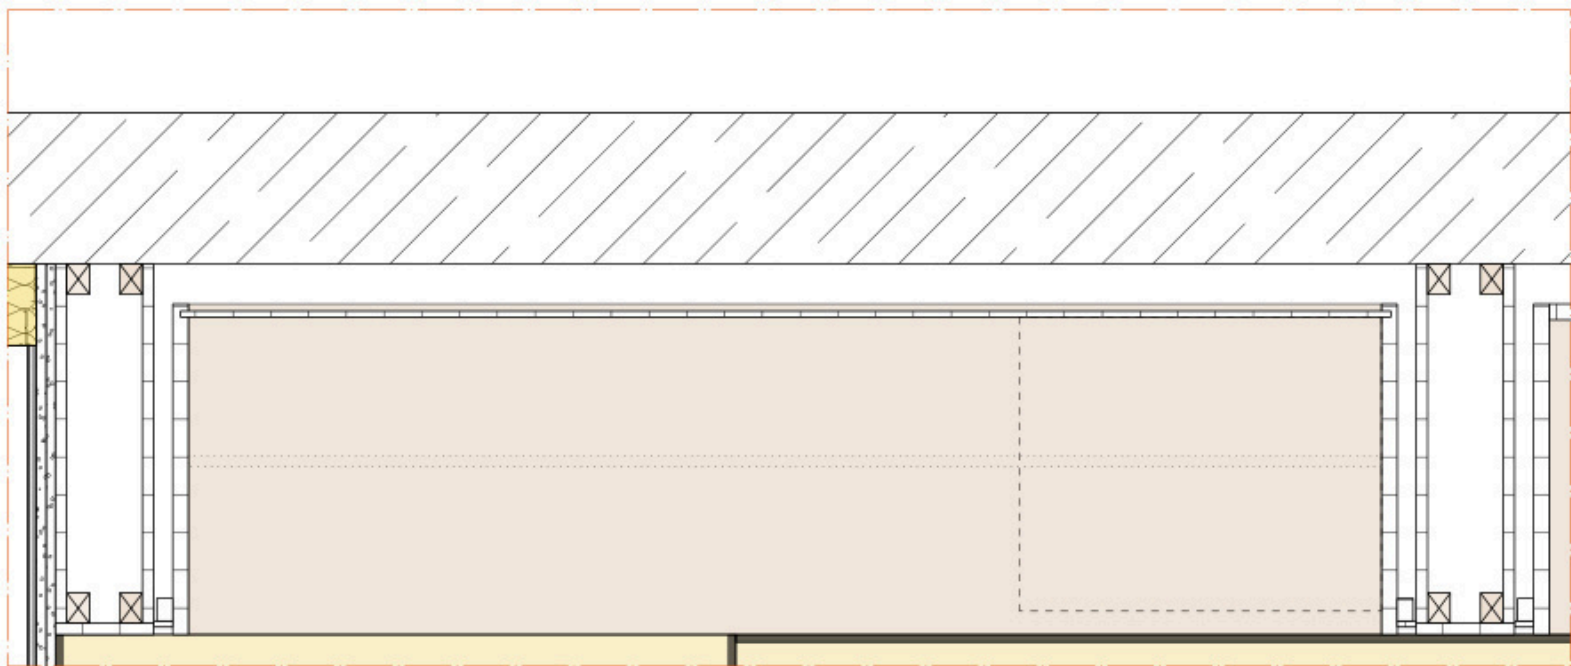

Einbauschränke Schnitt F-F' M 1:10

LEGENDE

BODENAUFBAU

Ohne Erhöhung		
Parkett, Eiche geölt	12	mm
Heizestrich	65	mm
Trennlage PE-Folie	5	mm
Trittschalldämmung	40	mm
Stahlbeton Bodenplatte	200	mm
Bitumen Andichtung	5	mm
Perimeterdämmung XPS	250	mm
Sauberkeitsschicht	50	mm
Erdreich		

Mit Erhöhung		
Tatami Matten	40	mm
Parkett, Eiche geölt	12	mm
Heizestrich	65	mm
Trennlage PE-Folie	5	mm
Trittschalldämmung	40	mm
fermacell Hartschaum	30	mm
fermacell gebundene Schüttung	159	mm
Stahlbeton Bodenplatte	200	mm
Bitumenabdichtung	5	mm
Perimeterdämmung XPS	250	mm
Sauberkeitsschicht	50	mm
Erdreich		

WANDAUFBAU

Tragende Wände		
Stahlbeton	20	mm
Innenputz Gipsputz	13	mm

Trockenbauwand		
Gipskarton	2 x 12,5	mm
Dämmung	75	mm
CW-Profil		
Gipskarton	2 x 12,5	mm
Schiebetürsystem von Knauf Pocket Kit Standard		

Zwischenwände zwischen den Einbauschränken		
Holzbaukonstruktion 50x50 mit OSB-Platten		

DECKENAUFBAU		200 mm
Stahlbetondecke		
Nonius-Abhänger von Knauf		
CD-Profile	2 x 12,5	mm
2 x Gipskarton		

POS 1 TATAMIMATTEN		
Konstruktion		900x1800 mm
Kern aus Reisstroh, mit daraufliegender Binsenmatte mit seitlich angenähten Baumwollbändern		

POS 2 TEEKÜCHE		
Konstruktion		
Multiplex, Eiche funiert, Messerdeckfunier Eiche geölt		
Beschläge		
Blum Blumotion Clip Top		
Häfele Schleppschanier		
Kühlschrank		
Kühlschrank Minibar Eco 32 Hartmann		

POS 3 EINBAUSCHRÄNKE		
Konstruktion		
Multiplex, Eiche funiert, Messerdeckfunier Eiche geölt		
Schubkästen MPX Eiche funiert, Messerdeckfunier Eiche geölt		
Beschläge		
Schubladen im Kleiderschrank Unterflurführung Blum Tandem NL 480		
Frontschubladen Unterflurführung Blum Movento		
Blum Blumotion Clip top		

POS 4 BADEWANNE		
Konstruktion		
Eingelassene Badewanne im Wagenträger von Reuter		

AUS 2	Innenausbau 2	
Projekt	Hotelzimmer	
Planverfasser	Schabnam Shor - 883436	Inhalt
Prüfer	Prof. Dipl. Ing. W. Glas	Maßstab
Assistent	M. A. Jonas Wilhelm	
Semester	Sommersemester 2024	Plannummer
		08 // 08
		Präsentation
		17.07.2024