



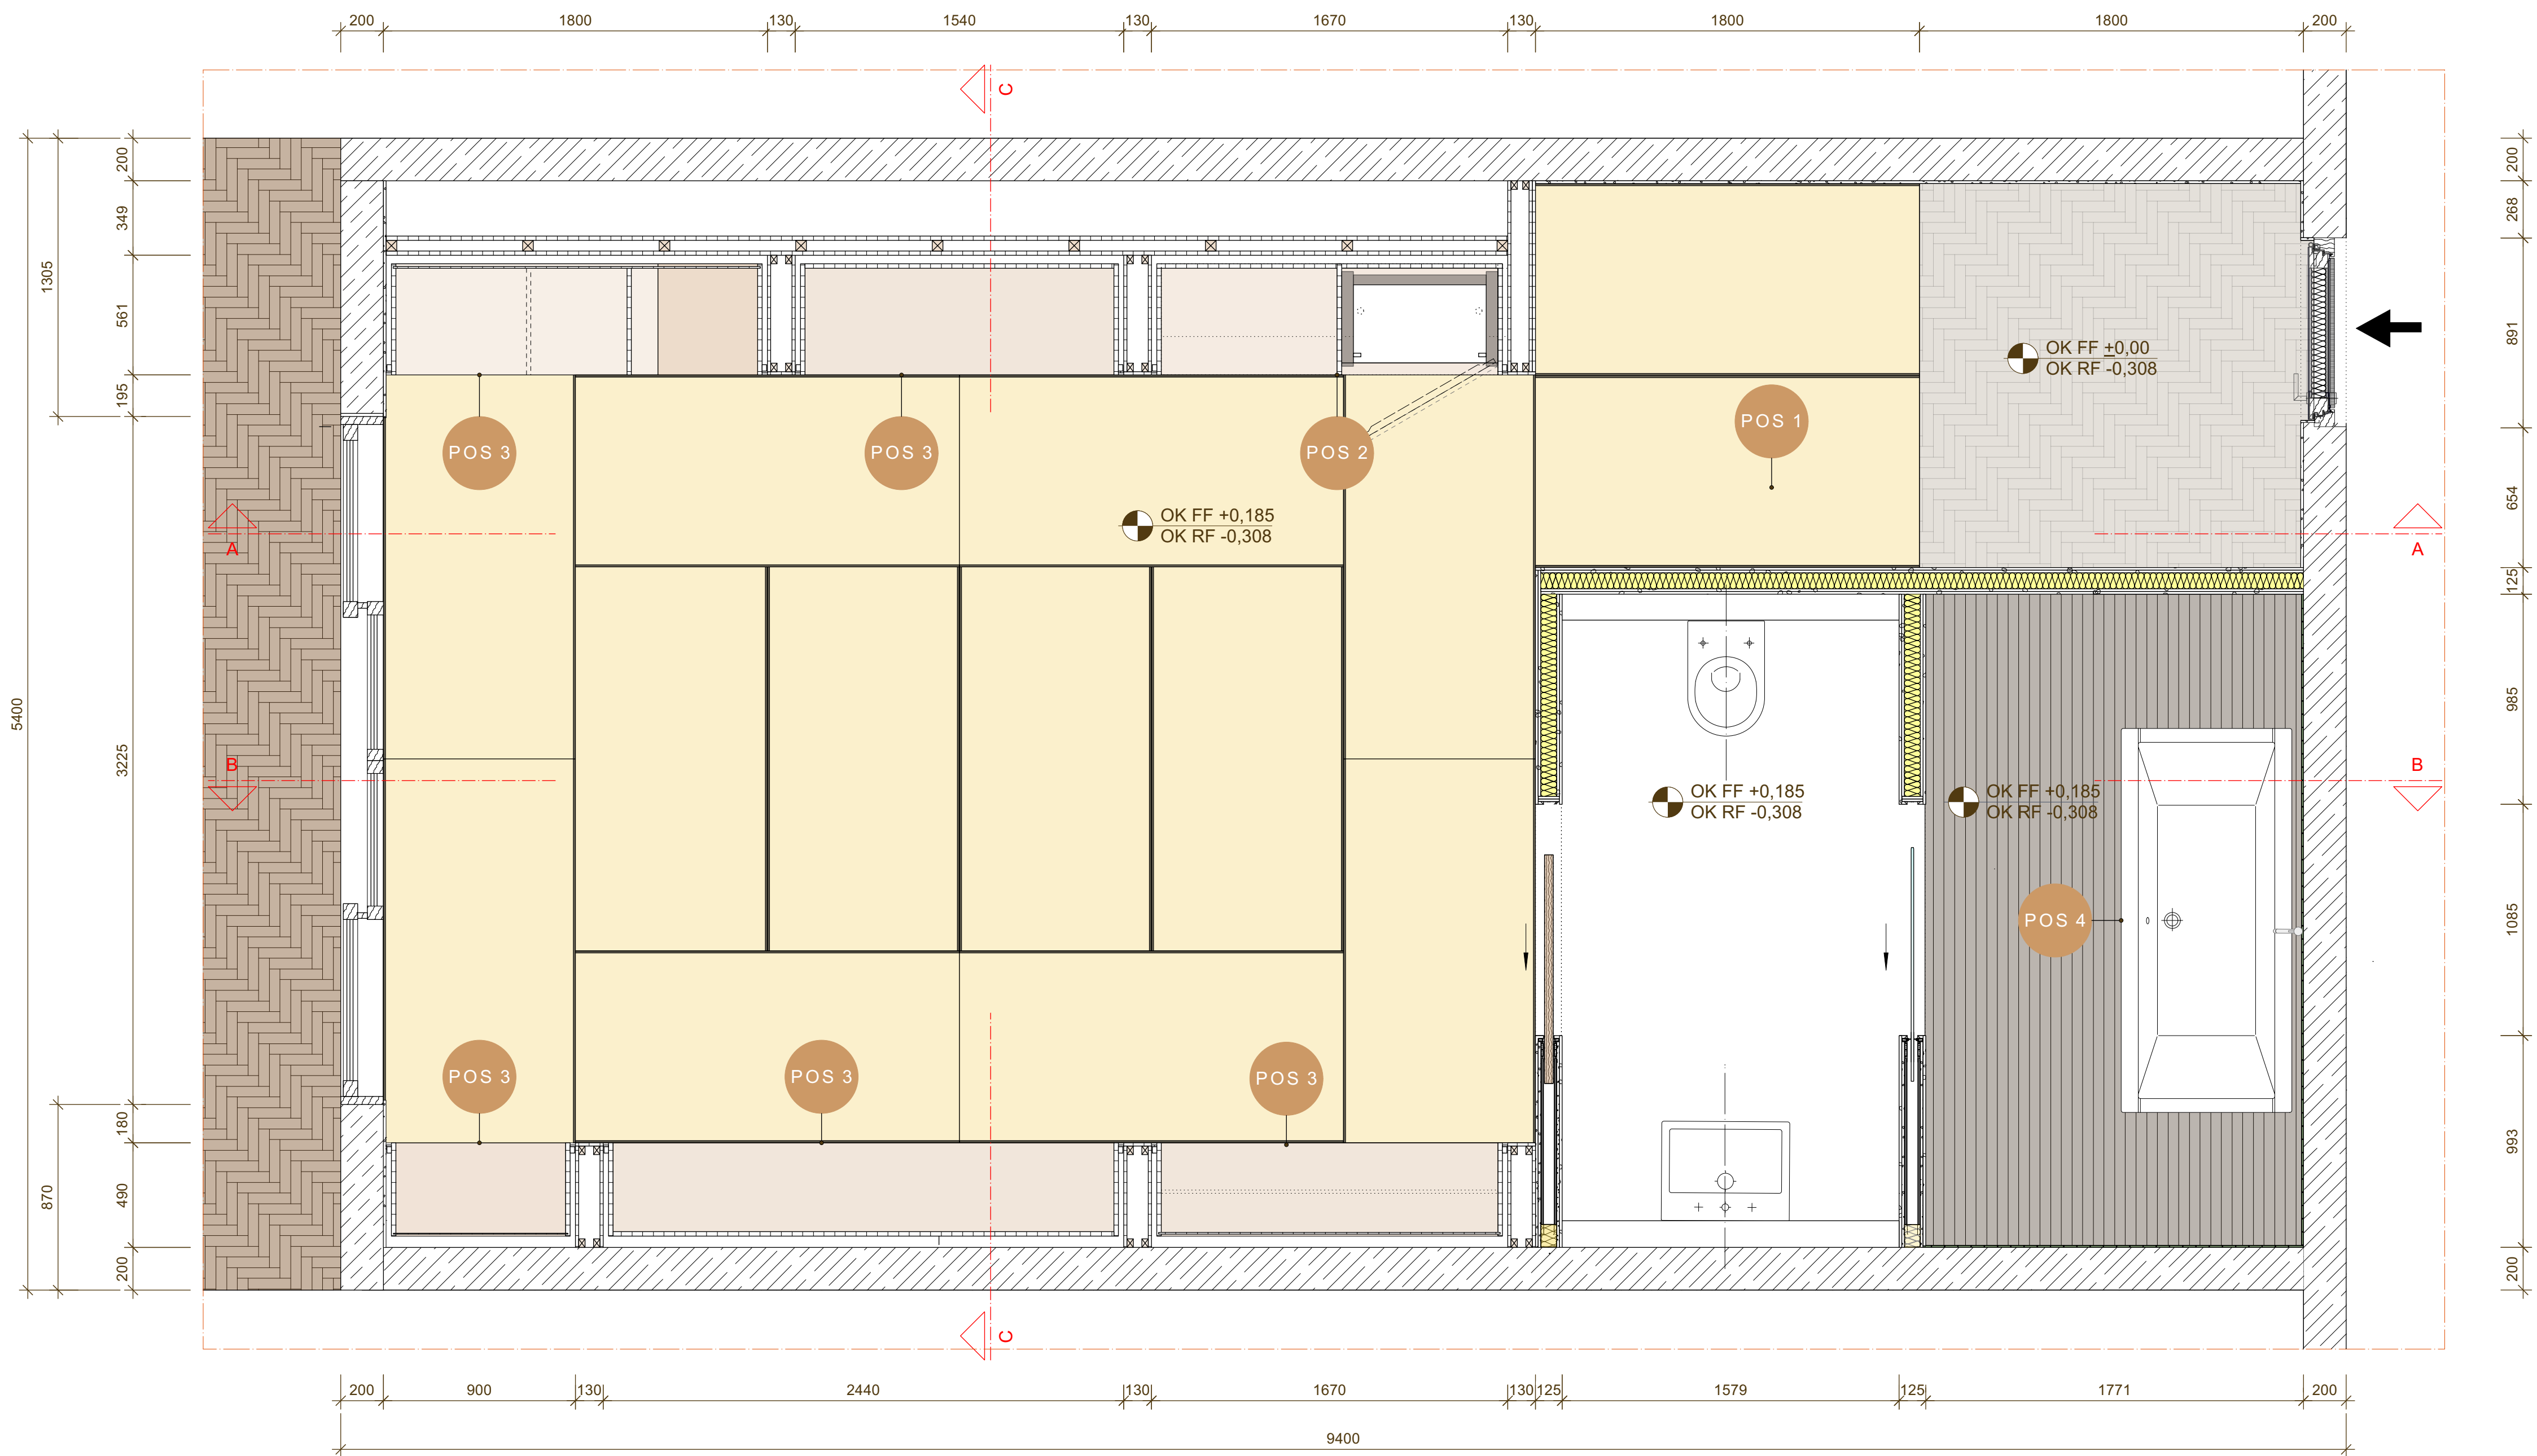

Grundriss M 1:20

Ebene 1	± 0,00 m	
Ebene 2	+ 0,185 m	
Ebene 3	+ 0,185 m	
Ebene 4	+ 0,185 m	

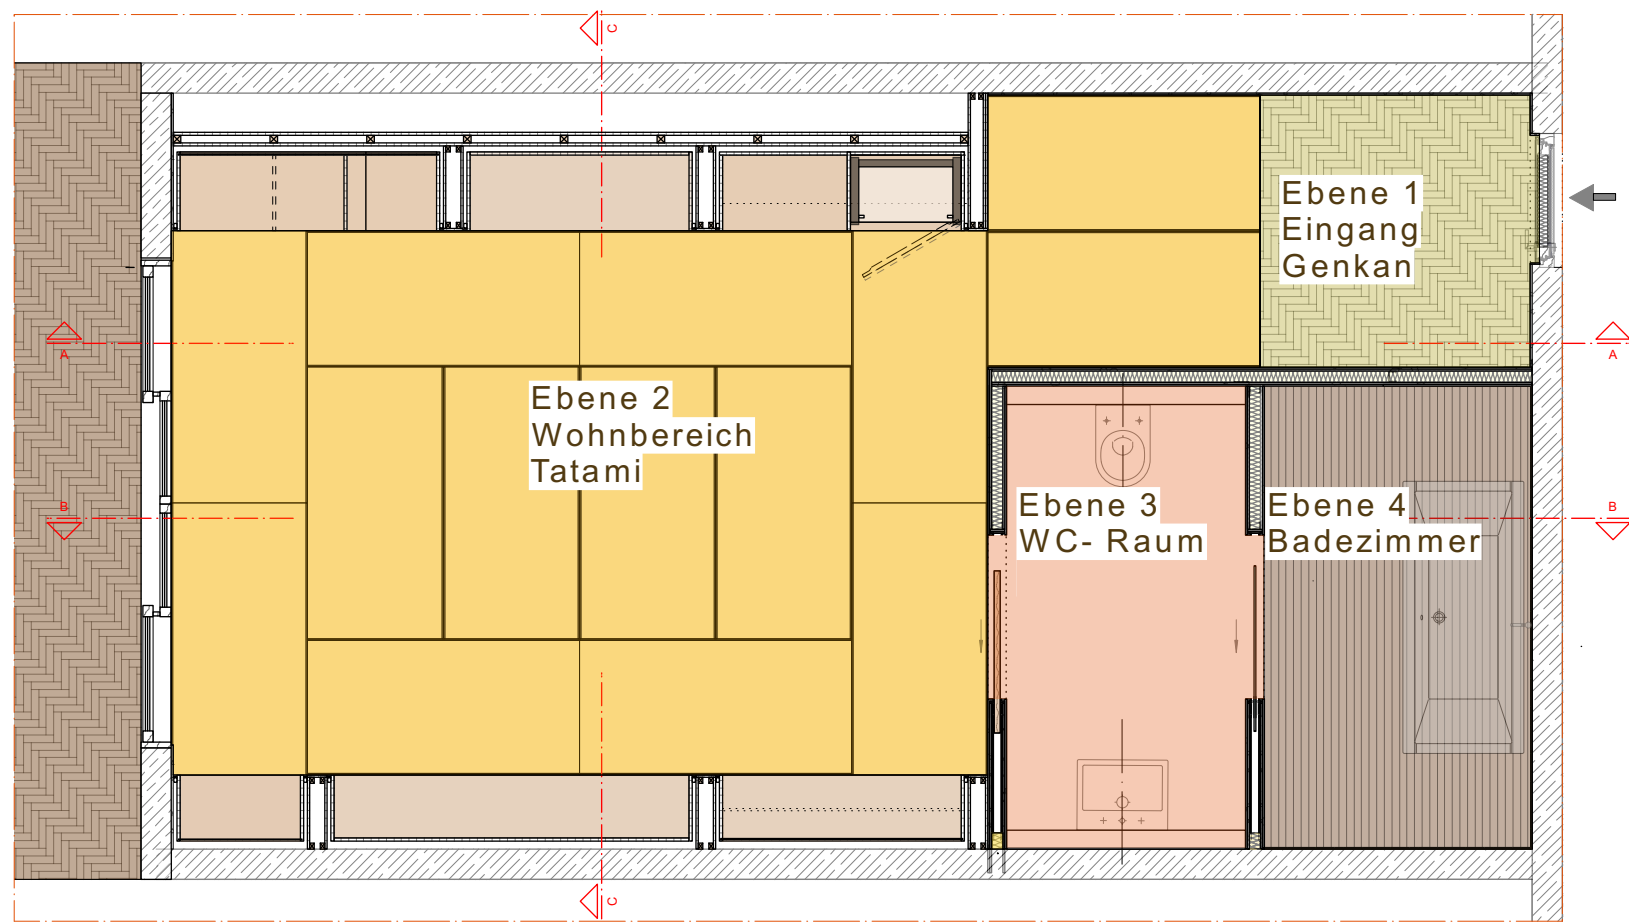

Bodenbelag Schema M 1:50

LEGENDE

BODENAUFBAU

Ohne Erhöhung

Parkett, Eiche geölt		
Heizestrich	12	mm
Trennlage PE-Folie	65	mm
Trittschalldämmung	5	mm
Stahlbeton Bodenplatte	40	mm
Bitumen Andichtung	200	mm
Perimeterdämmung XPS	5	mm
Sauberkeitsschicht	250	mm
Erdreich	50	mm

Mit Erhöhung

Tatami Matten		
Parkett, Eiche geölt		
Heizestrich		
Trennlage PE-Folie		
Trittschalldämmung	40	mm
fermacell Hartschaum	12	mm
fermacell gebundene Schüttung	65	mm
Stahlbeton Bodenplatte	5	mm
Bitumenabdichtung	40	mm
Perimeterdämmung XPS	30	mm
Sauberkeitsschicht	159	mm
Erdreich	200	mm
	5	mm
	250	mm
	50	mm

WANDAUFBAU

Tragende Wände

Stahlbeton	
Innenputz Gipsputz	

Trockenbauwand

Gipskarton		
Dämmung		
CW-Profil		
Gipskarton	20	mm
Schiebetürsystem von Knauf Pocket Kit Standard	13	mm

Zwischenwände zwischen den Einbauschränken

Holzbaukonstruktion 50x50 mit OSB-Platten	2 x 12,5	mm
	75	mm
	2 x 12,5	mm

DECKENAUFBAU

Stahlbetondecke	
Nonius-Abhänger von Knauf	
CD-Profile	
2 x Gipskarton	

POS 1 TATAMIMATTEN

Konstruktion

Kern aus Reisstroh, mit daraufliegender Binsenmatte mit seitlich angenähten Baumwollbändern

POS 2 TEEKÜCHE

Konstruktion	200	mm
Multiplex, Eiche furniert, Messerdeckfurnier Eiche geölt	2 x 12,5	mm

Beschläge

Blum Blumotion Clip Top
Häfele Schleppschanier
Kühlschrank
Kühlschrank Minibar Eco 32 Hartmann

POS 3 EINBAUSCHRÄNKE

Konstruktion	900x1800	mm
Multiplex, Eiche furniert, Messerdeckfurnier Eiche geölt		
Schubkästen MPX Eiche furniert, Messerdeckfurnier Eiche geölt		
Beschläge		
Schubläden im Kleiderschrank Unterflurführung Blum Tandem NL 480		
Frontschubläden Unterflurführung Blum Movento		
Blum Blumotion Clip top		

POS 4 BADEWANNE

Konstruktion	
Eingelassene Badewanne im Wagenträger von Reuter	

AUS 2 Innenausbau 2

Projekt Hotelzimmer

Planverfasser Schabnam Shor - 883436

Prüfer Prof. Dipl. Ing. W. Glas

Assistent M. A. Jonas Wilhelm

Semester Sommersemester 2024

Inhalt
Grundriss 1:20
Bodenbelag Schema 1:50

Plannummer 01 // 08
Präsentation 17.07.2024