



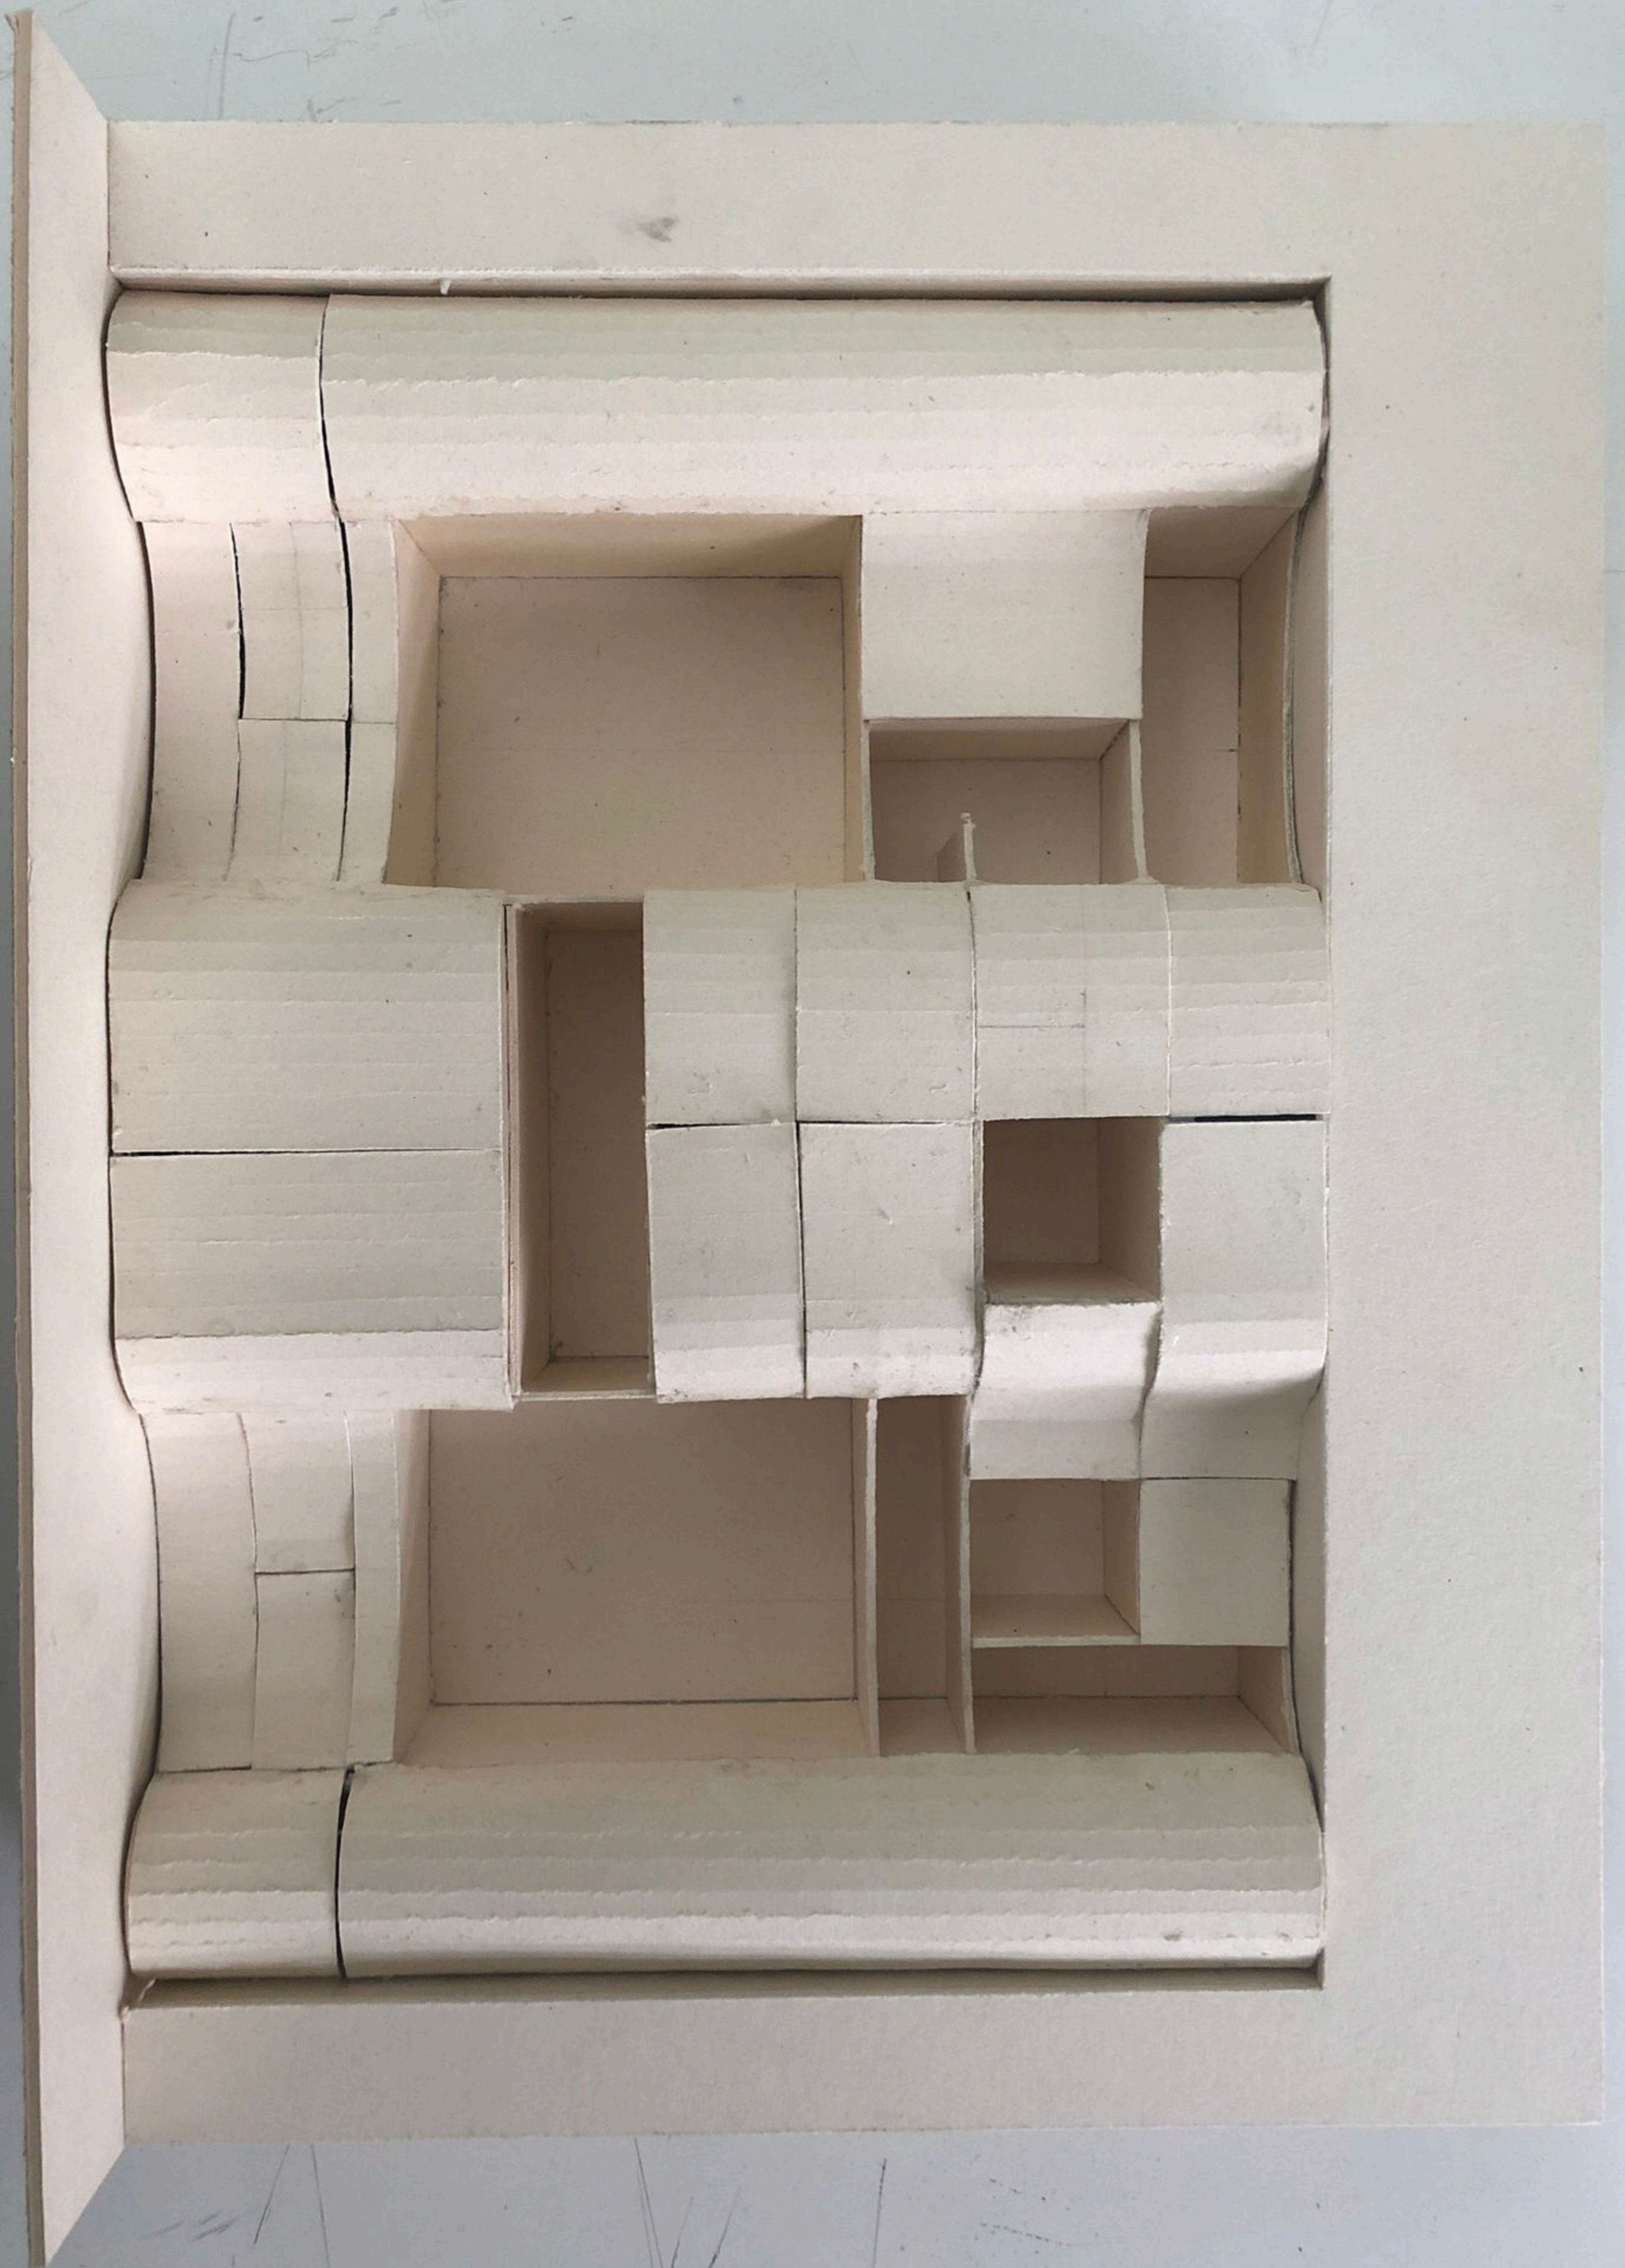




MDF, furniert und beidseitig lackiert
mit Vollholzleimer Verklebung
als Bodenführung eingesetzt

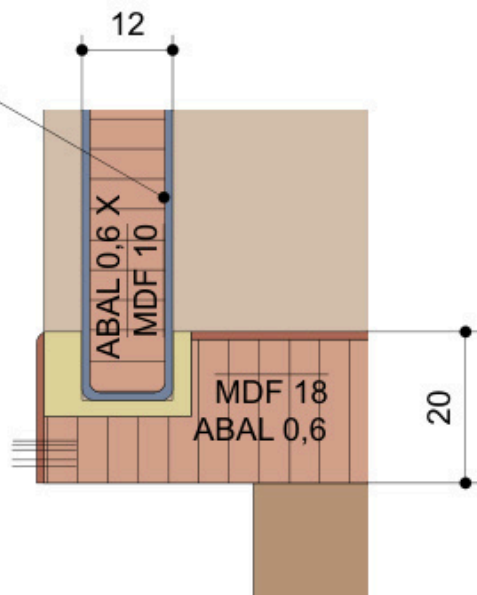

Detail Führungsschiene M1:1

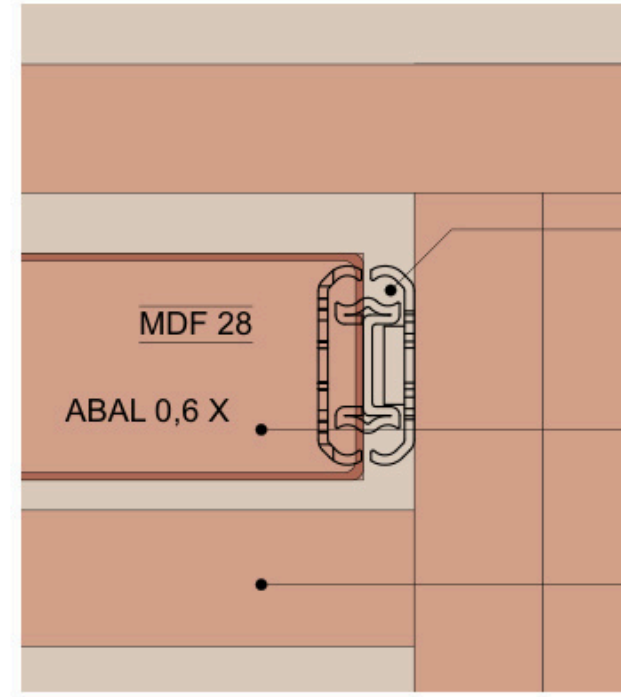


Detail Vollauszug Tischplatte M1:1

Vollauszug
400 mm Einbaulänge
406 mm Auszug
Kugelführung
Tragkraft bis 45 kg

Ansicht Tischplatte aus
MDF 28 mm, beschichtet,
furniert mit Tanne je 1 mm,
beidseitig

Ansicht MDF 18 mm, einseitig
beschichtet und furniert
Rahmenkonstruktion

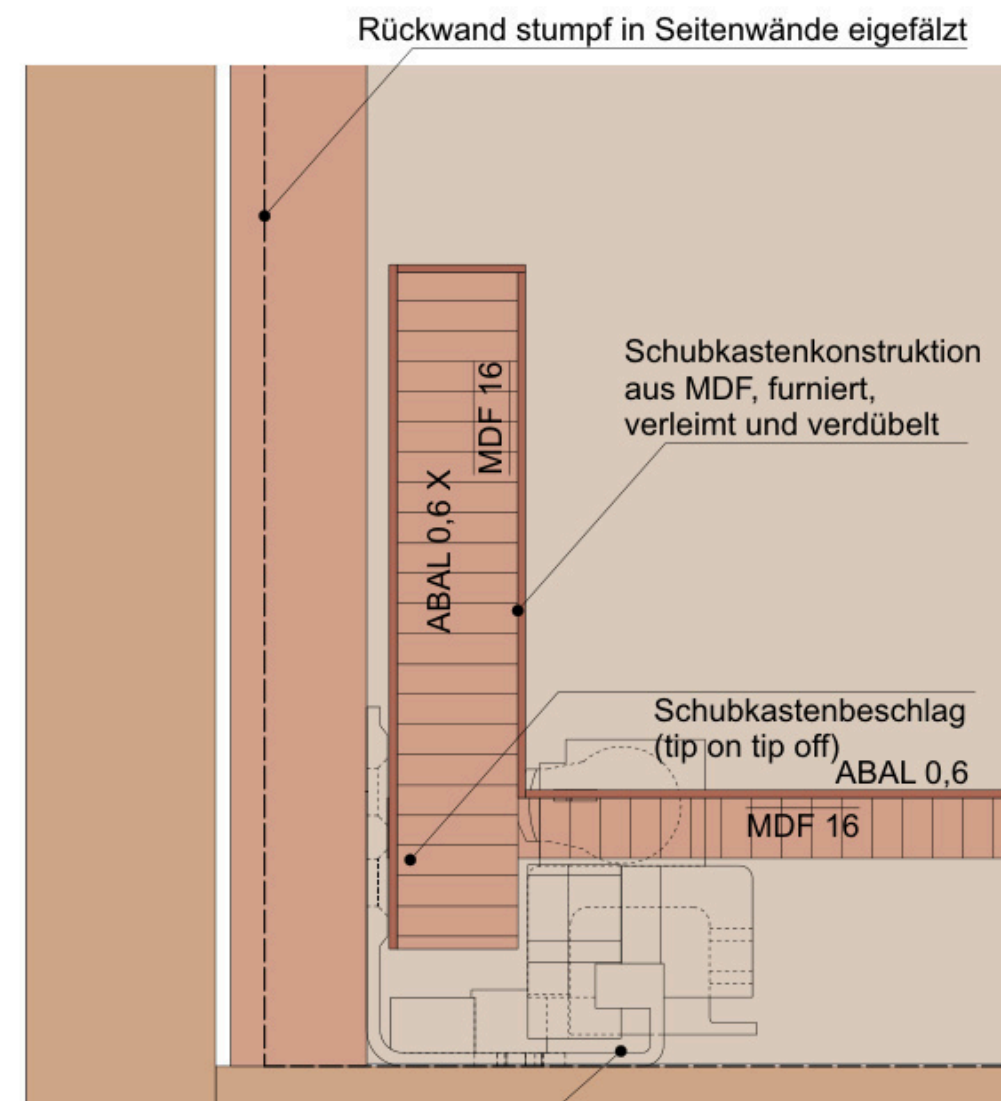


Schubkastenbeschlag
(tip on tip off)

Detail TIP ON TIP OFF M1:1


Schubkastenkonstruktion
aus MDF, furniert,
verleimt und verdübelt

Schubkastenbeschlag
(tip on tip off)
ABAL 0,6
MDF 16


MDF, furniert mit
geeigneter
Grundierung
farbig (Blautönen)
lackiert als
Holzrolladen in
Bodenführung

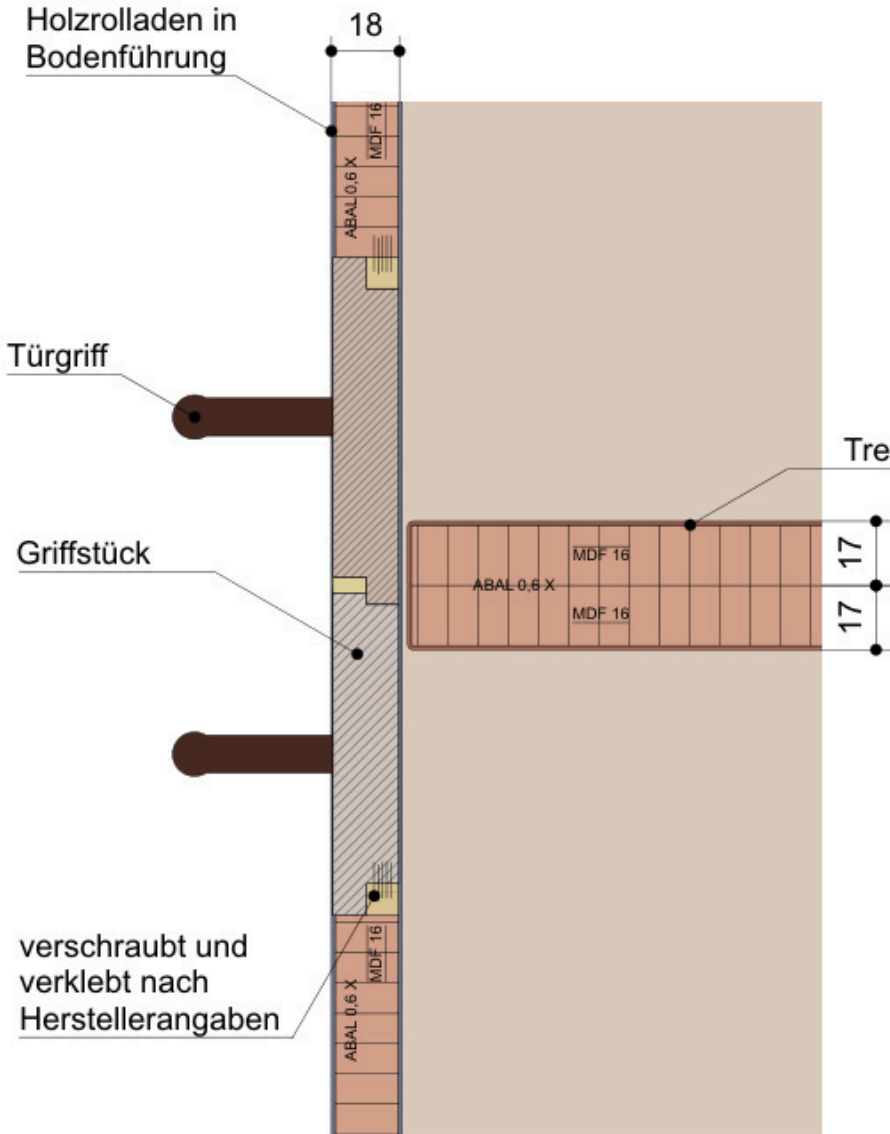

Detail Türgriff M1:2

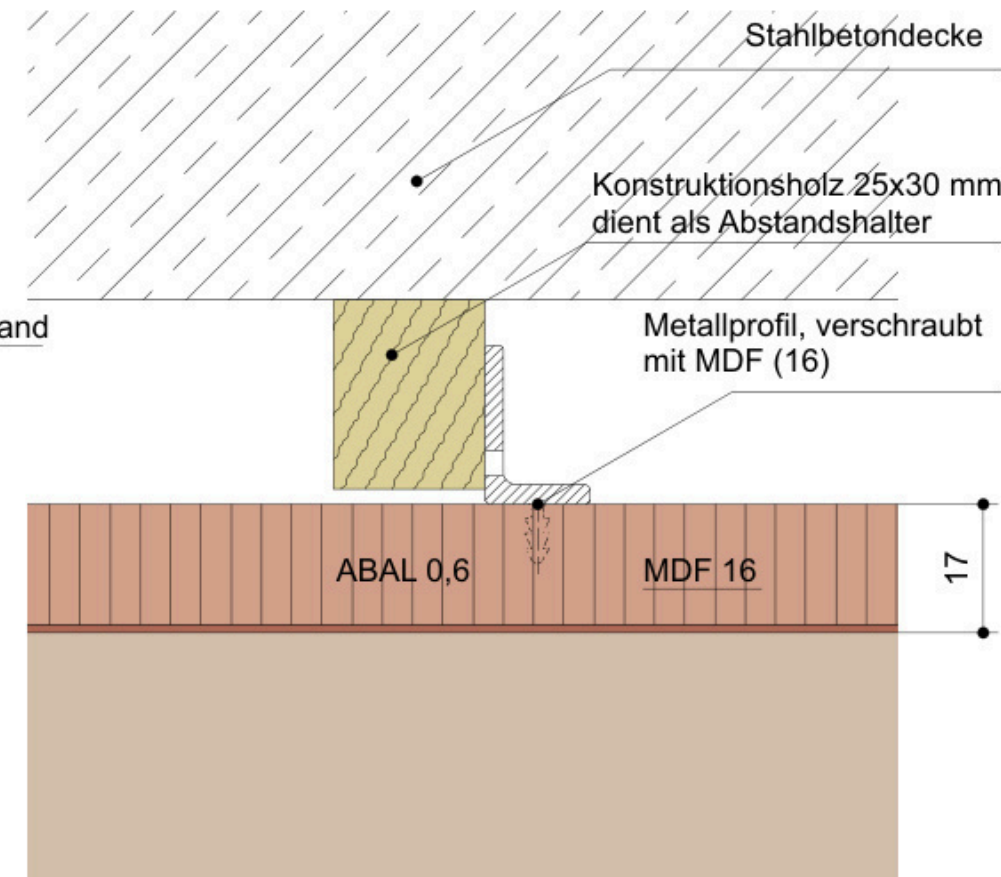


Detail Möbelrahmen M1:1

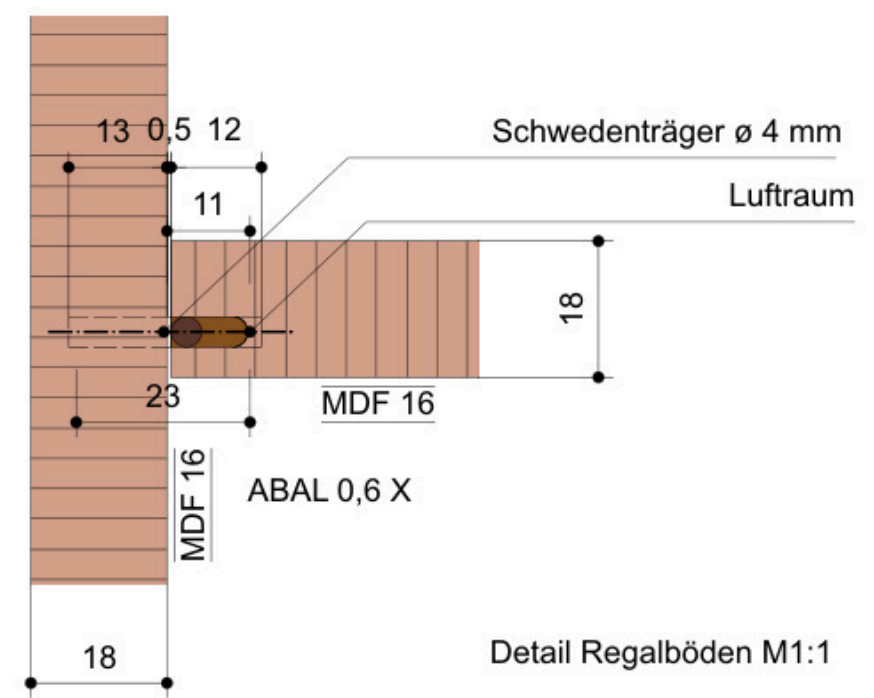


Detail Regalböden M1:1

Möbelentwurf	Prof. Y. Fehling	Jennifer Schmitt 882806	Details M1:1 / 1:2
Abgabe	26.07.2022	Schabnaml Shor 883436	
Aufgabe 3 - Krankenhausmöbel		FB Innenarchitektur SS 22	
Fertigungszeichnung	01/02		




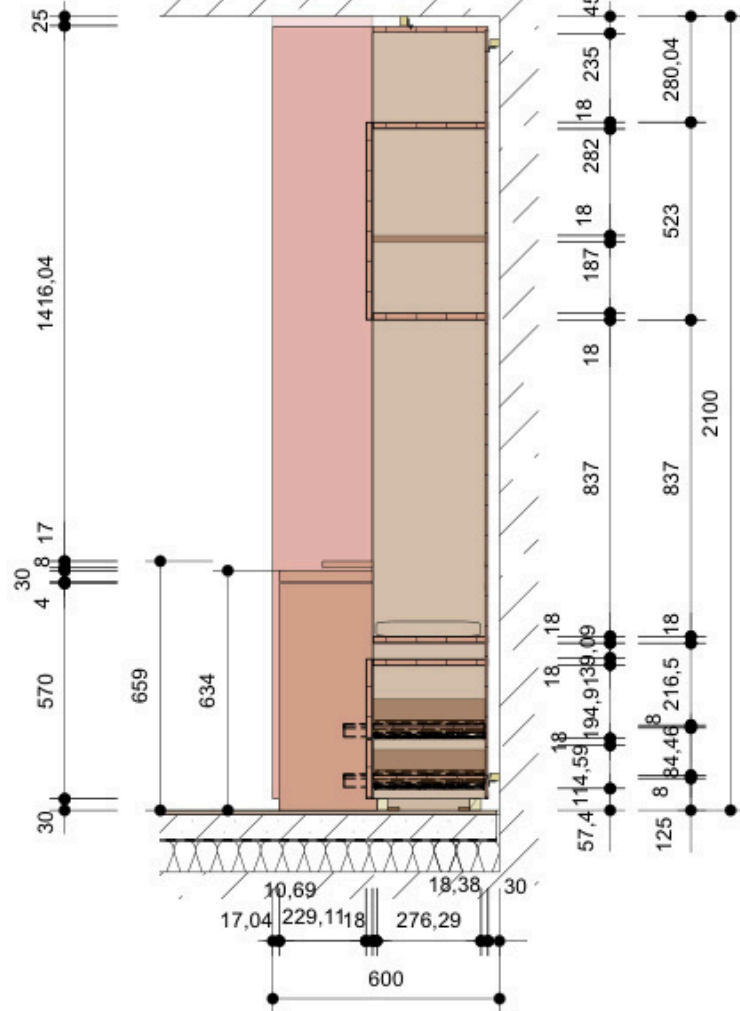


Schnitt AA M1:20

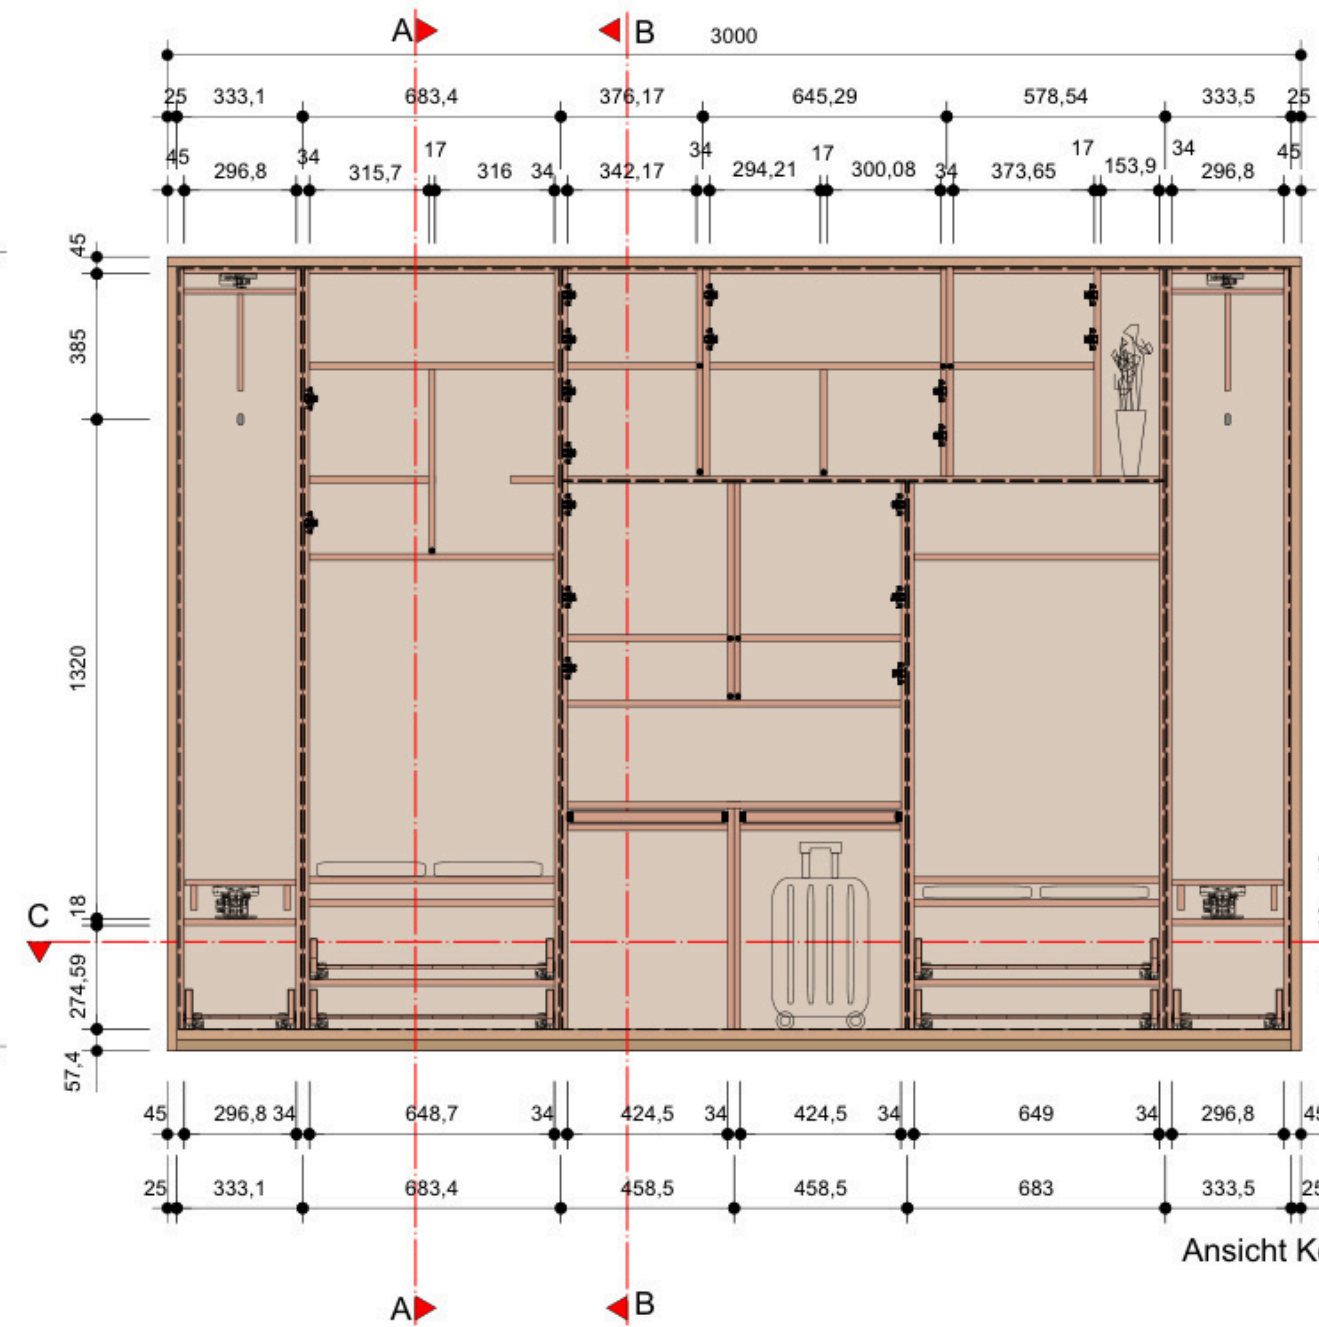


Ansicht Korpus M1:20

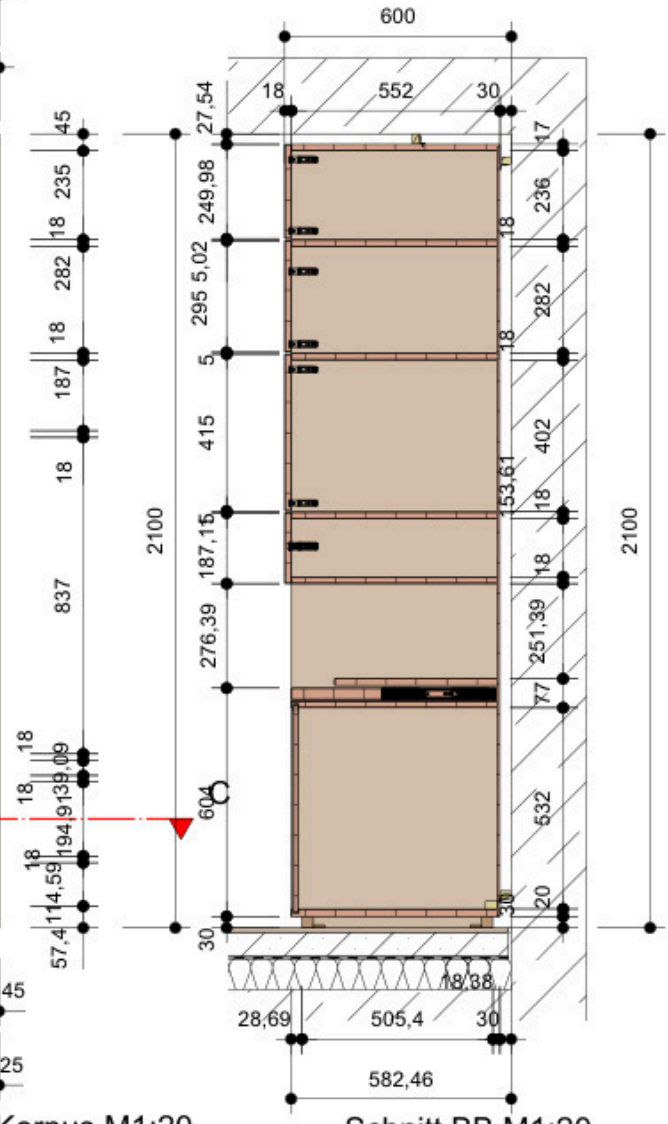


Schnitt BB M1:20

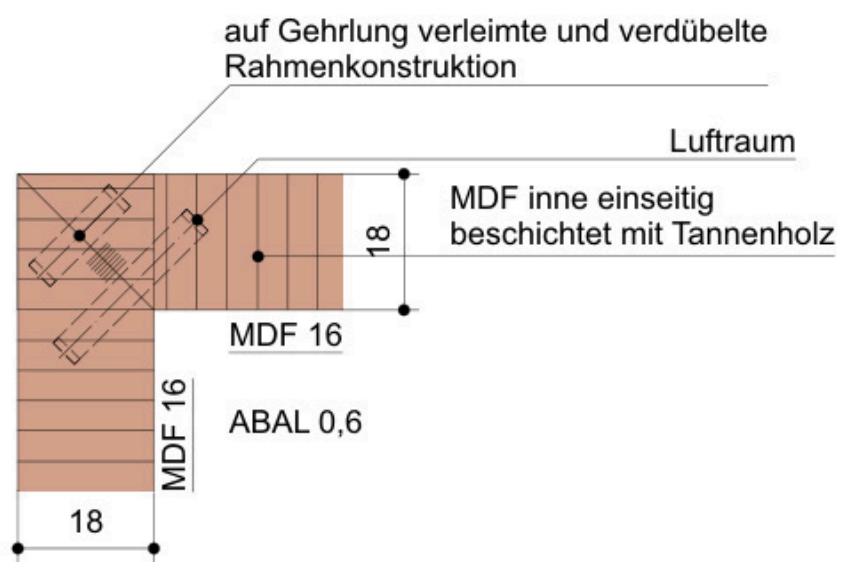

Detail Eckverbindung M1:1

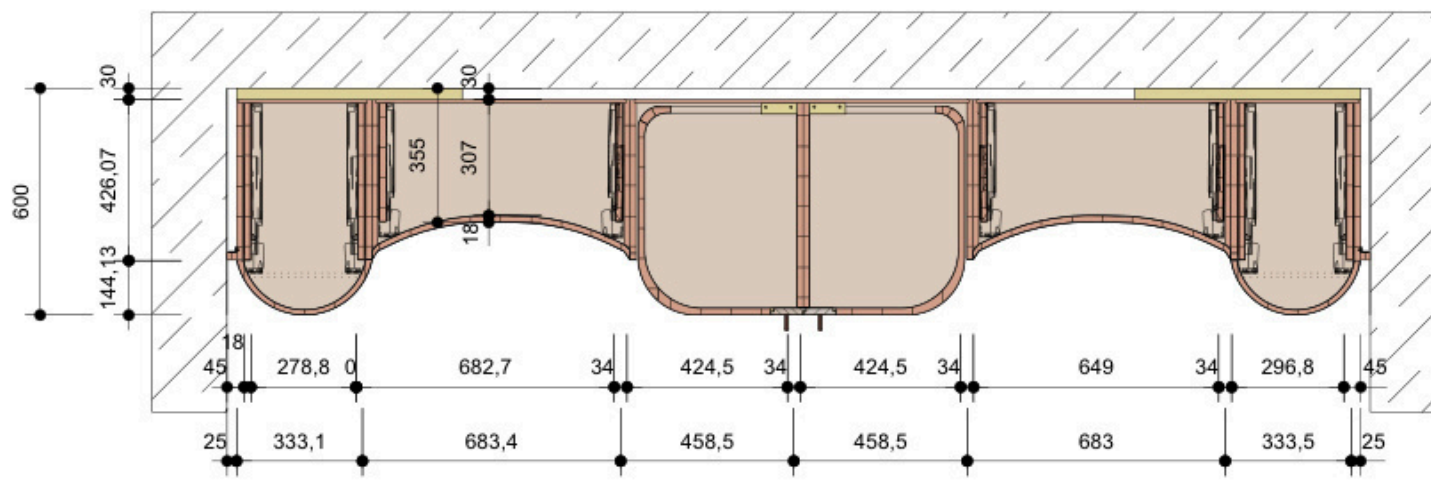


Schnitt CC M1:20

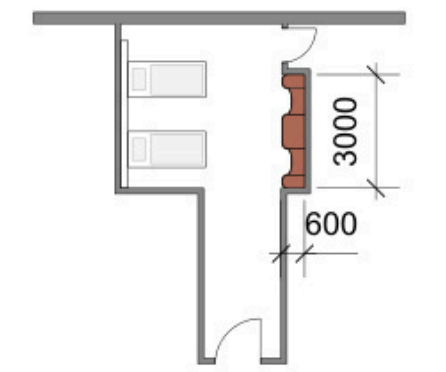


Grundriss M1:100


Möbelentwurf	Prof. Y. Fehling	Jennifer Schmitt 882806	Grundriss M1:100
Abgabe	26.07.2022	Schabnamli Shor 883436	Ansicht Korpus M1:20
Aufgabe 3 - Krankenhausmöbel		FB Innenarchitektur SS 22	Schnitte A/B/C M1:20
Fertigungszeichnung	01/02		Draufsicht M1:20

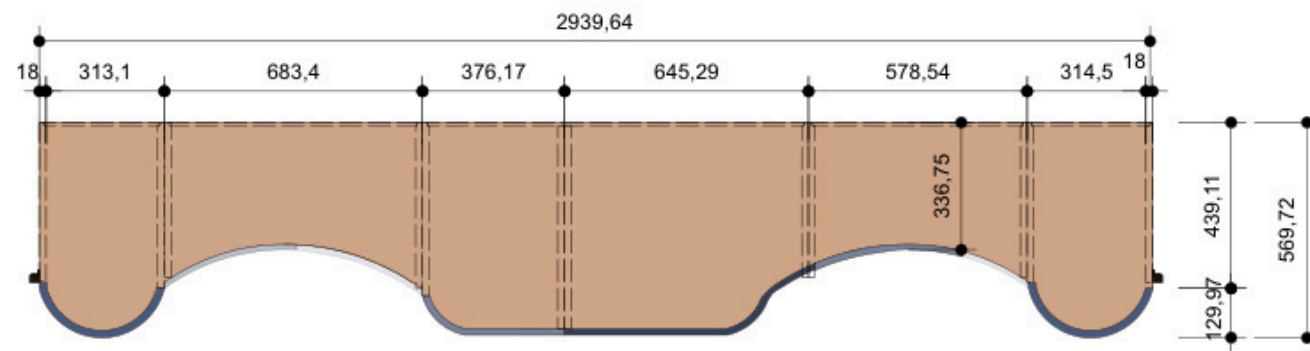

Draufsicht M1:20

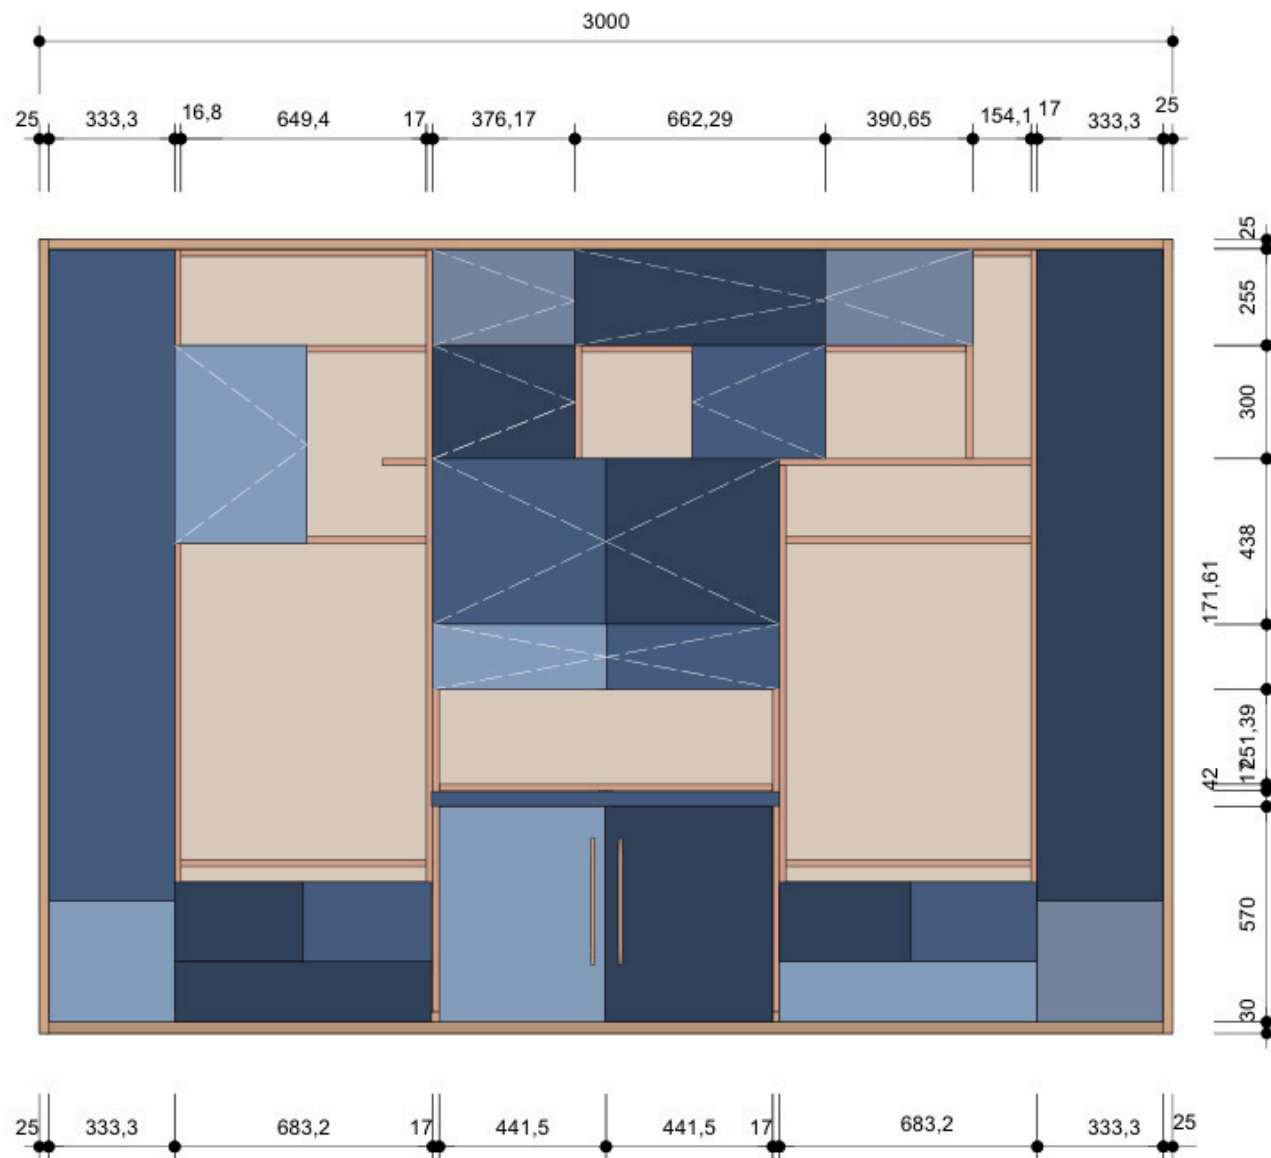

Ansicht M1:20

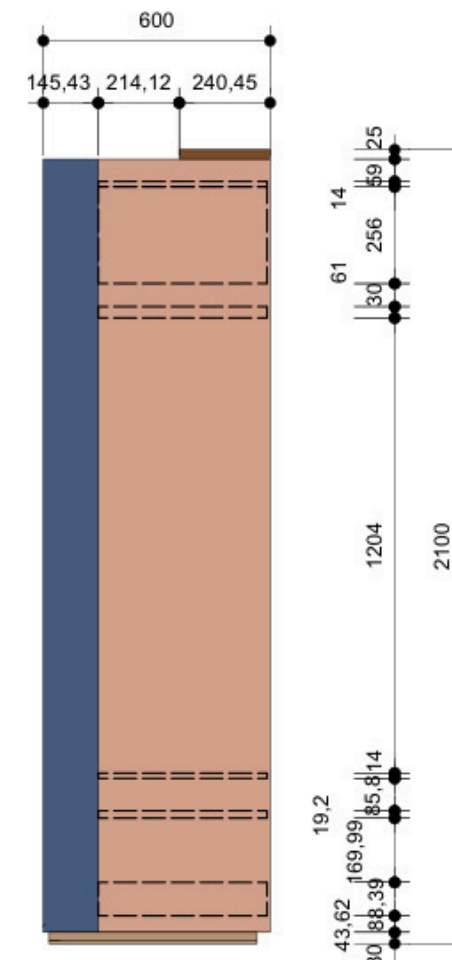

Seitenansicht M1:20



Hejm(Dänisch für Zuhause)

Ein Möbel wie es zu Hause steht

Wer kennt es nicht ? Die typischen Krankenhausmöbell, die sich alles andere als nach Wohlfühlen und zu Hause anfühlen ? Die sich karg und leblos anfühlen ? Das soll unseren Schrank ändern. Er soll den Patienten bei dem Genesungsweg, mit Komfort, Geräumigkeit und Ästhetik begleiten. Die vielen verschiedenen Aufbewahrungsmöglichkeiten, soll dem Patienten die Möglichkeit geben ihre Privatsachen so zu verstauen, wie er es braucht. Die freien Flächen dienen dazu die mitgebrachten Blumen in eine Vase zu stellen oder sein Lieblingsbild hinzustellen oder gar den aktuellsten Krimi den man liest. Selbst ein integrierter Schreibtisch ist vorhanden, der sich bei Bedarf herausziehen lässt und beim Notfall sich schnell wieder mit einem Schubser reinschieben lässt ,um Notfall Situation genug Platz zu bieten. Die Sitzmöglichkeit ist ausgepolstert und ahmt in ihren Rundungen eine Umarmung nach. Sie bietet nicht nur den Patienten eine Alternative zum Tisch und Stuhl, auch für Besucher kann die Sitzmöglichkeit genutzt werden, um Komfort bei längeren Besuchszeiten zu gewährleisten ohne sich aufzudrängen oder zu ewigen Verweilen einzuladen. Platz für den ganzen Koffer hat der Schrank auch, so dass dieser nicht irgendwo im Raum stört. Um raus aus der gewohnten rechteckigen Schrankvariante zu kommen, haben die Fronten eine Rundungen bekommen, um so das Auge was neues zu geben. Sollten man Angst um seine Privatsachen haben, so kann man Diese in dem abschließbaren Fach unterbringen.

Im allgemeinen kann man sagen dass das Möbel ein hervorragender Allrounder ist der dem Patienten genug Platz gibt ... Zum ausbreiten und verstauen seiner Sachen. Dabei soll ihm das Gefühl vermittelt werden er befinde sich nicht in einem Krankenzimmer, sondern kann s auch ‚Zuhause‘ gesund werden.

Möbelentwurf	Prof. Y. Fehling	Jennifer Schmitt 882806	Perspektive
Abgabe	26.07.2022	Schabnam Shor 883436	Draufsicht M1:20
Aufgabe 3 - Krankenhausmöbel		FB Innenarchitektur SS 22	Ansicht M1:20
Fertigungszeichnung	01/02		Seitenansicht M1:20