


GLP SS22

SPARKASSE

ALEXANDER KLEIN

GRUNDRISS

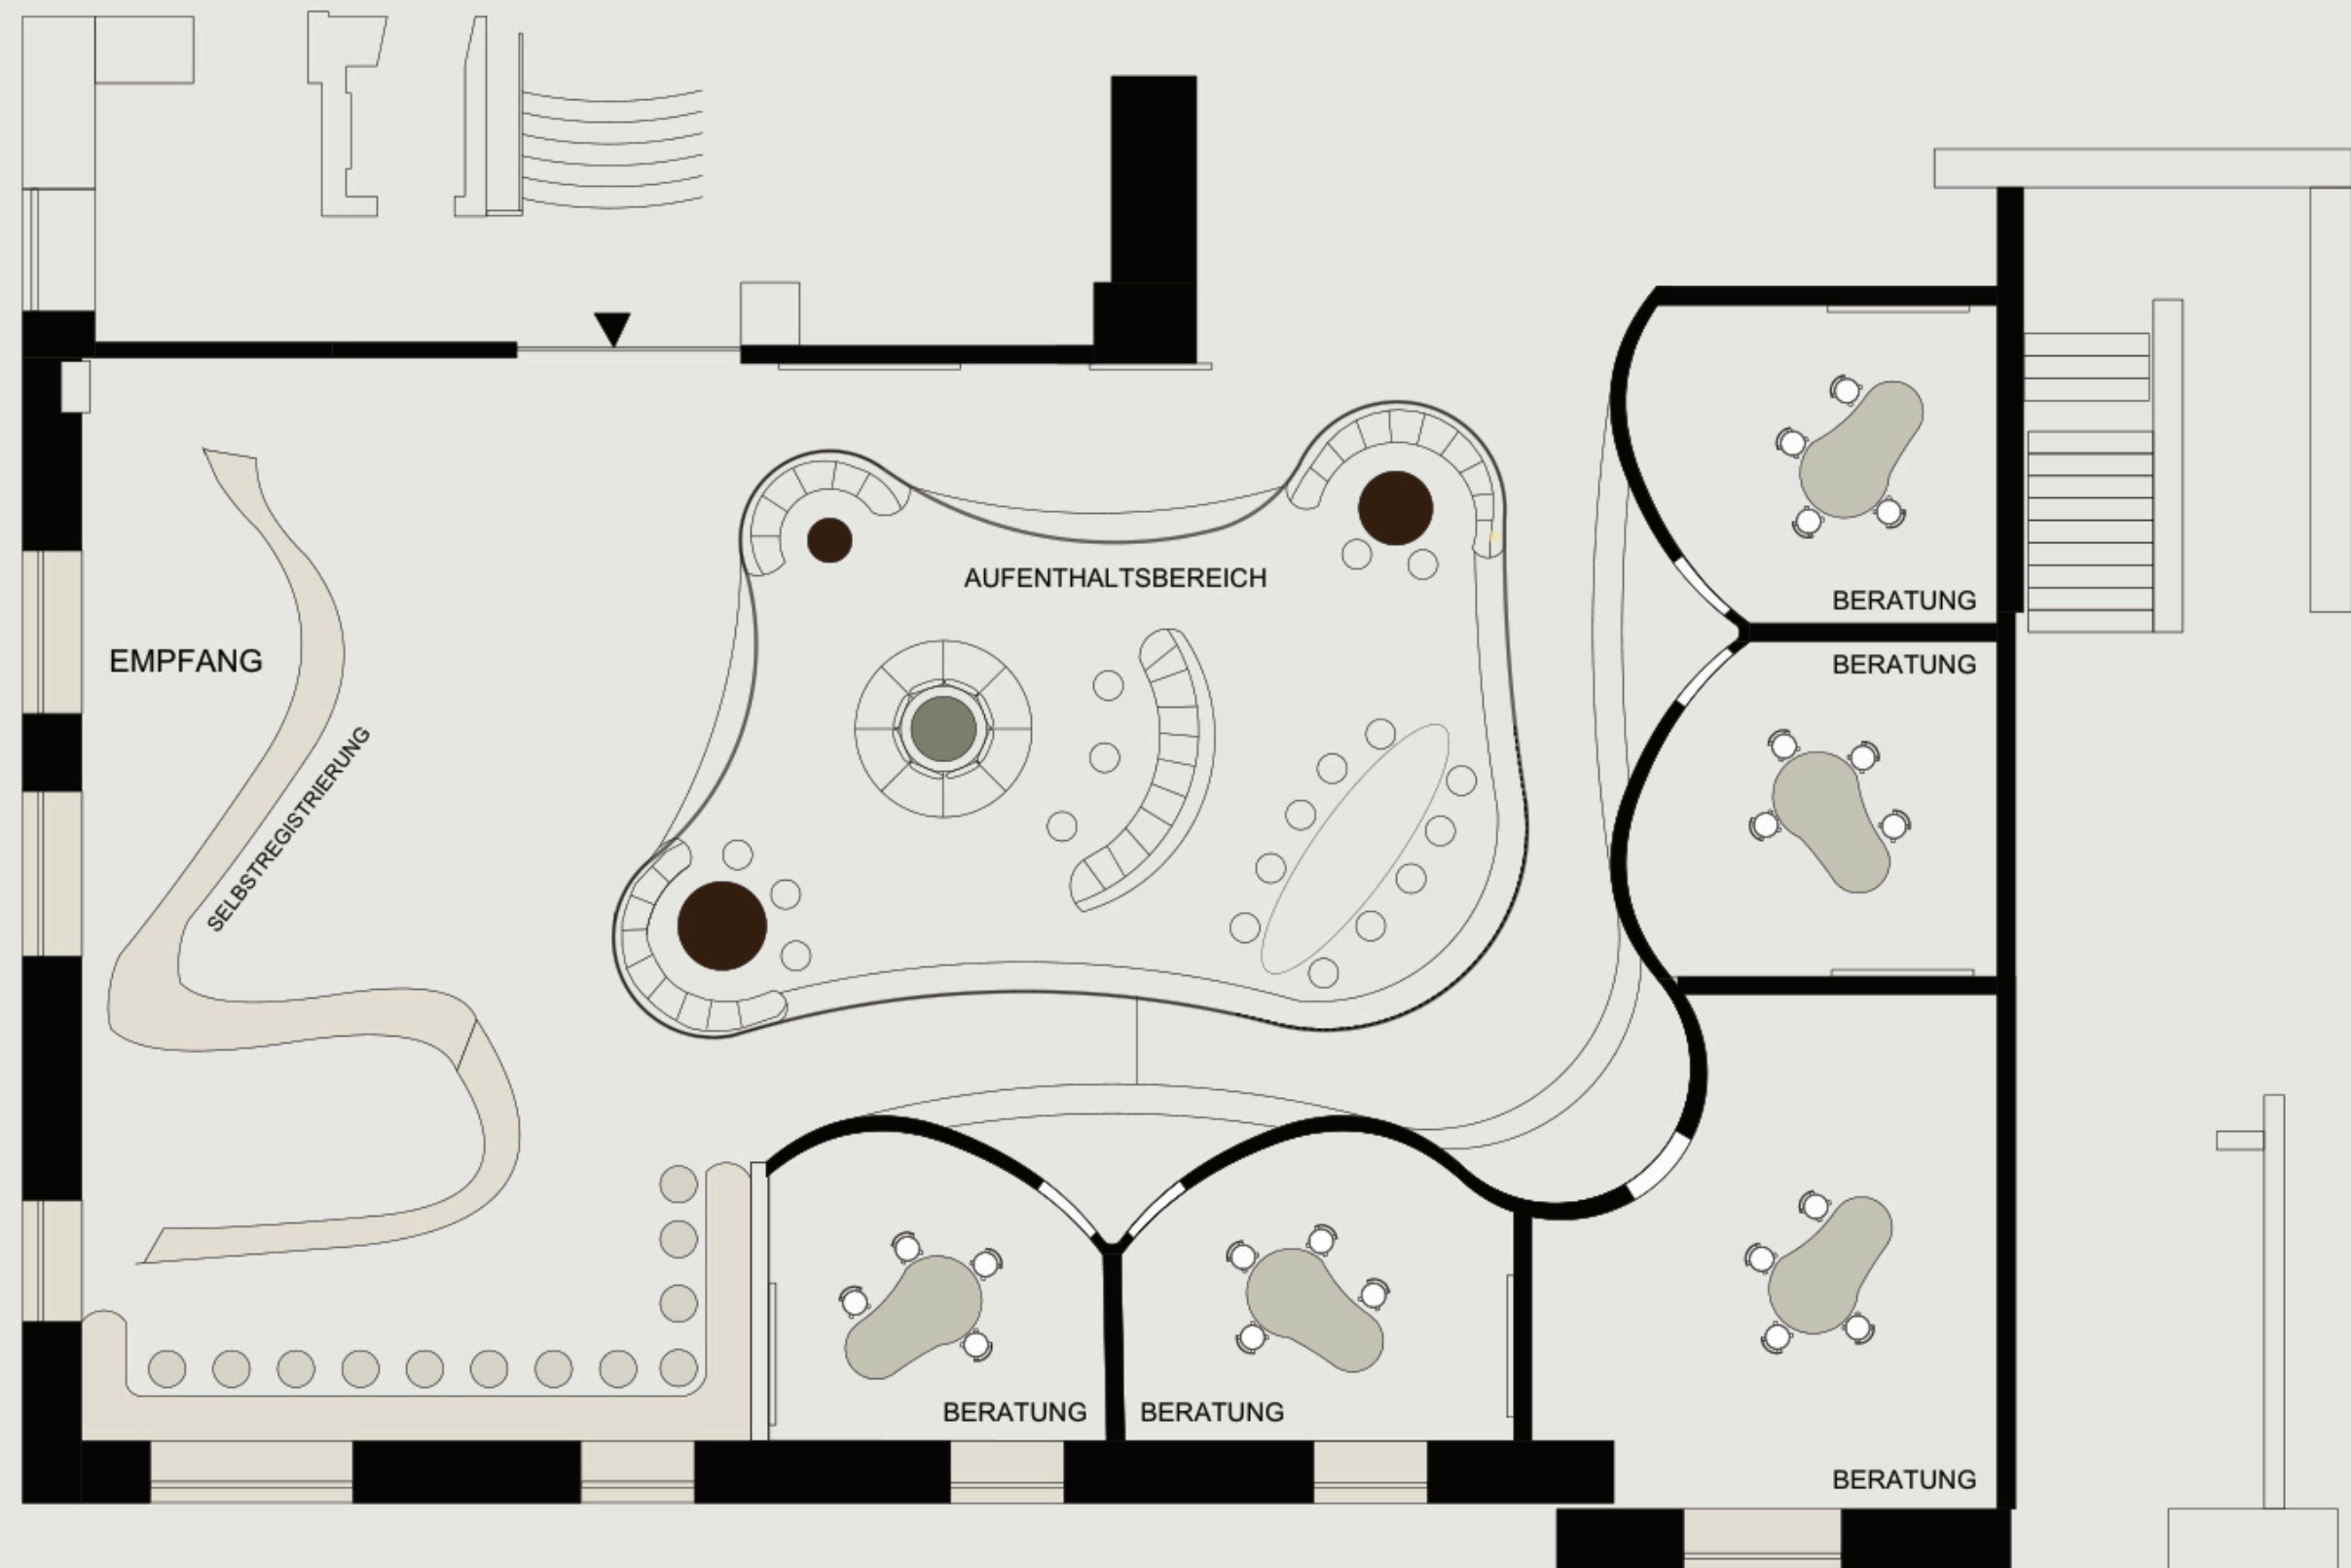


SCHNITT





GRUNDBELEUCHTUNG

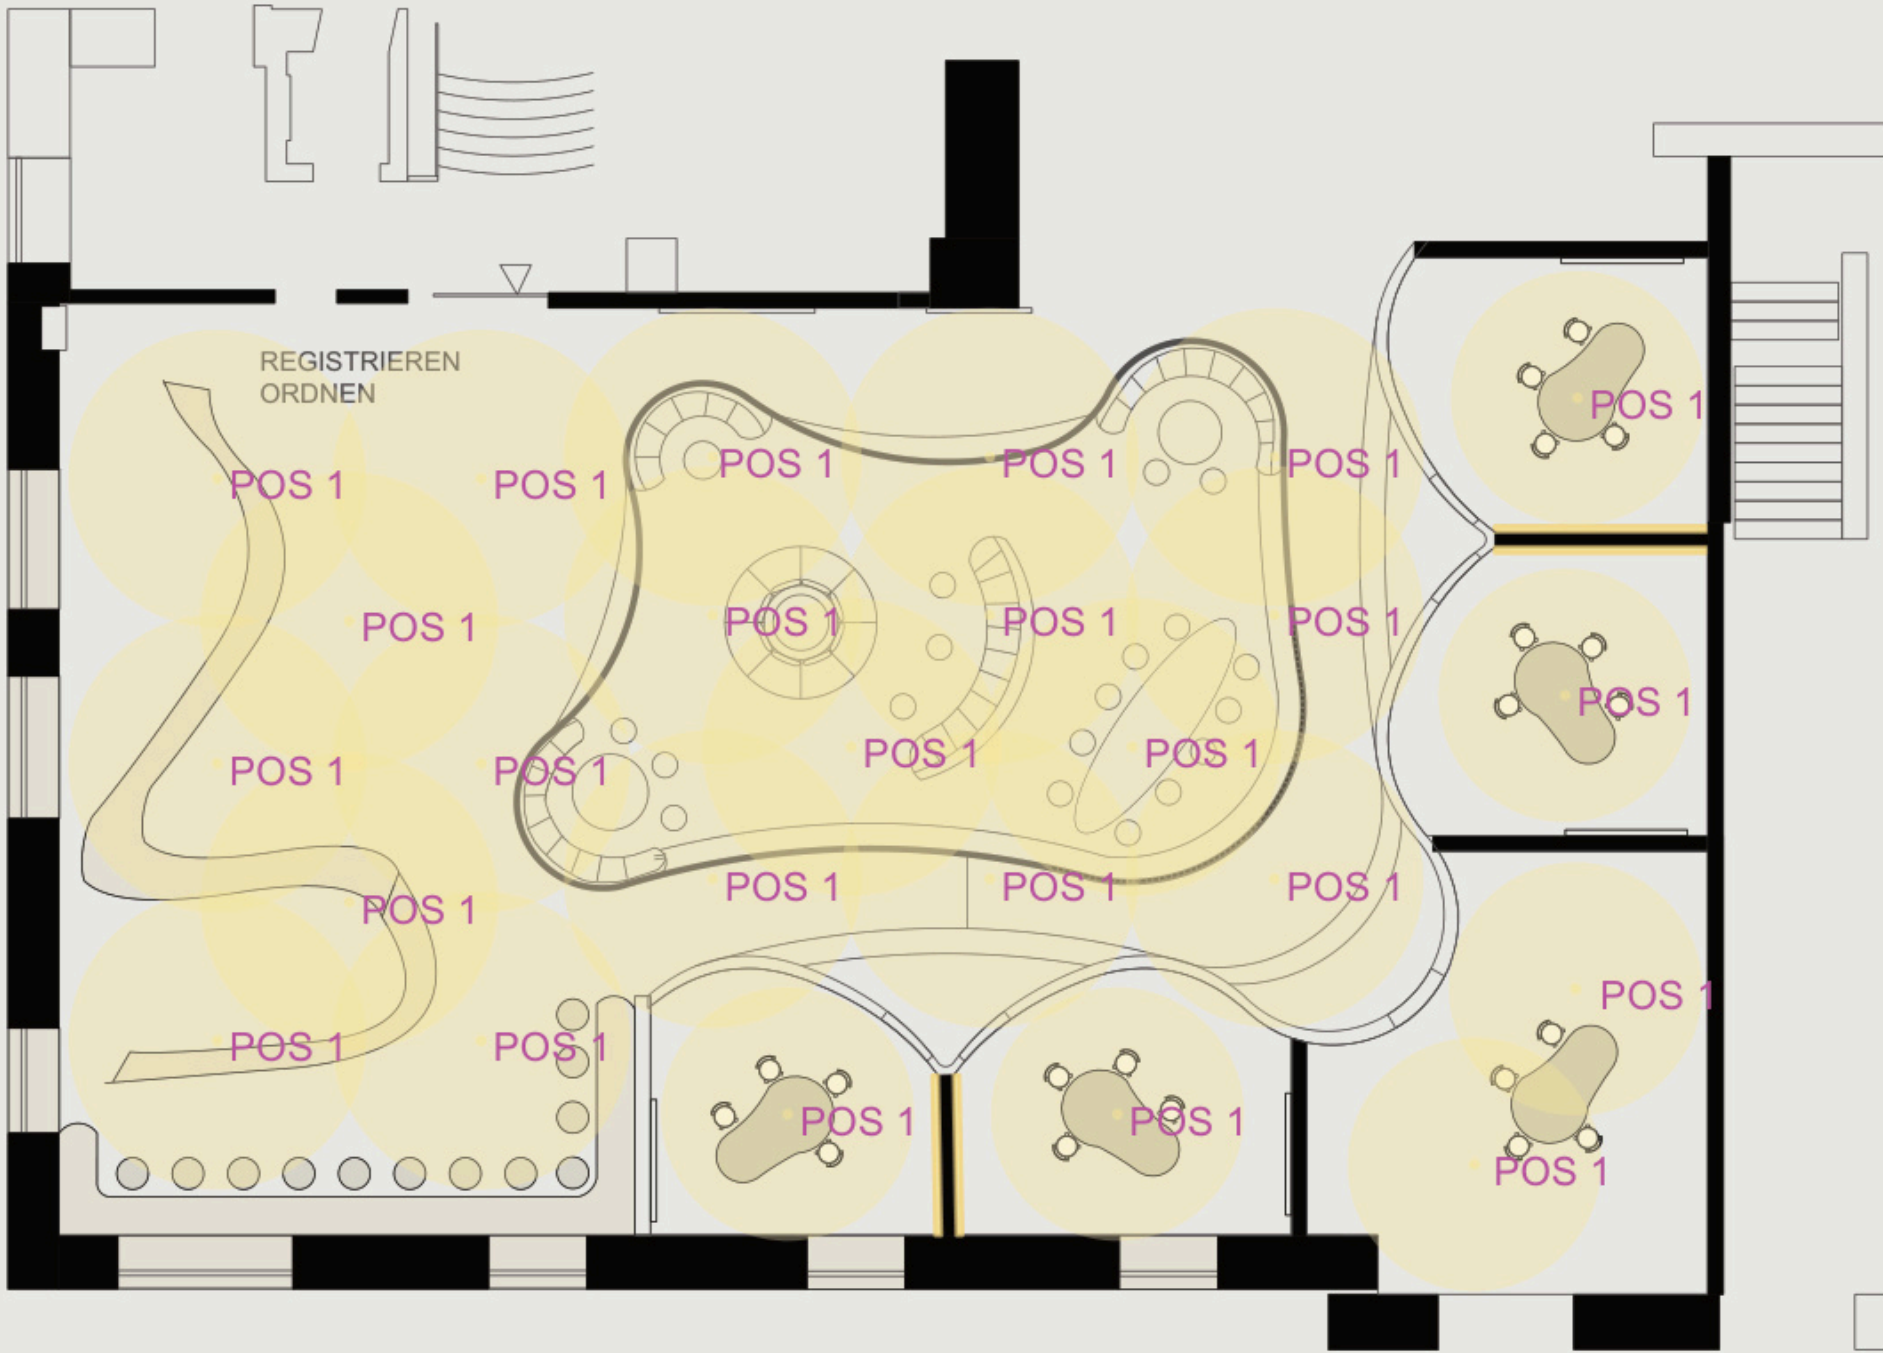

Grundbeleuchtung im Grundriss M 1:200

Leuchtlegende



POS
Leuchtentyp: Wide Flood Beam
Hersteller: Fa. Igguzini
Art.Nr.: QS40
Leuchtmittel: LED: 36W 4350lm
Lichtfarbe: 4000K CRI 80
Lichtverteilung: Wide Flood 58°
Vorschaltgerät: extern in Zwischendecke
Dimmung: DALI
Abmessung: ø180x44
Ausschnittsmaß: ø180
Einbauort: Grundlichtaustattung, überall
Zubehör: Abdeckung PA91
Stückzahl: 24



POS
Leuchtentyp: Pendelleuchte
Hersteller: Milan
Art.Nr.: Hilan 505415
Leuchtmittel: LED Modul
Lichtfarbe: Warmweiß Extra 2700 K
Lichtverteilung: 43°
Vorschaltgerät: Trockenbaukasten extern in Zwischendecke
Dimmung: Dimmbar
Abmessung: ø210x55mm
Einbauort: Theke
Zubehör: externem Phasenanschnittsdimmer Georg Bechter Licht Kabelauslass Trockenbaukapsel
Stückzahl: 17



POS
Leuchtentyp: Wandleuchte
Hersteller: Lindby
Art.Nr.: Tjada 9626347
Leuchtmittel: 1x 5 W LED
Lichtfarbe: Warmweiß 3.000 K
Lichtverteilung: Hinter der Lampe
Vorschaltgerät: dimmbar
Dimmung: dimmbar
Abmessung: 218x75x75mm
Ausladung: 75 mm
Einbauort: Beratungsräume
Lichtstrom: 720 lm
Anschlussspannung: 230 VL
Schutzart: IP20
Stückzahl: 6




POS
Leuchtentyp: Effizienzleuchte
Hersteller: Fa. Igguzini
Art.Nr.: EA08
Leuchtmittel: LED: 1,7W 113 lm
Lichtfarbe: 2600K CRI 80
Lichtverteilung: 140°/109°
Vorschaltgerät: extern in Zwischendecke
Dimmung: PWM
Abmessung: 7004x100x2200
Einbauort: abgehängte Decke über der Lounge und den festen Möbeln, um die Beratungsräume
Zubehör: Befestigungsklammer X156 Konstantspannungsdimmer MPW3
Stückzahl: 22



POS
Leuchtentyp: Effizienzleuchte
Hersteller: Fa. Igguzini
Art.Nr.: P310
Leuchtmittel: LED: 2W 121 lm
Lichtfarbe: 2700K CRI 90
Lichtverteilung: 25°
Vorschaltgerät: extern in Zwischendecke
Abmessung: ø31x58
Ausschnittsmaß: ø31
Einbauort: über den Lamellen
Stückzahl: 68



POS
Leuchtentyp: Pendelleuchte
Hersteller: Vencha OVAL
Art.Nr.: VE-5510133-GD-3K
Leuchtmittel: LED: 25W Max
Lichtfarbe: 3000K /5000K
Lichtverteilung: 25°
Vorschaltgerät: extern in Zwischendecke
Abmessung: 90mm x 405mm
Einbauort: in den Beratungsräumen
Stückzahl: 5

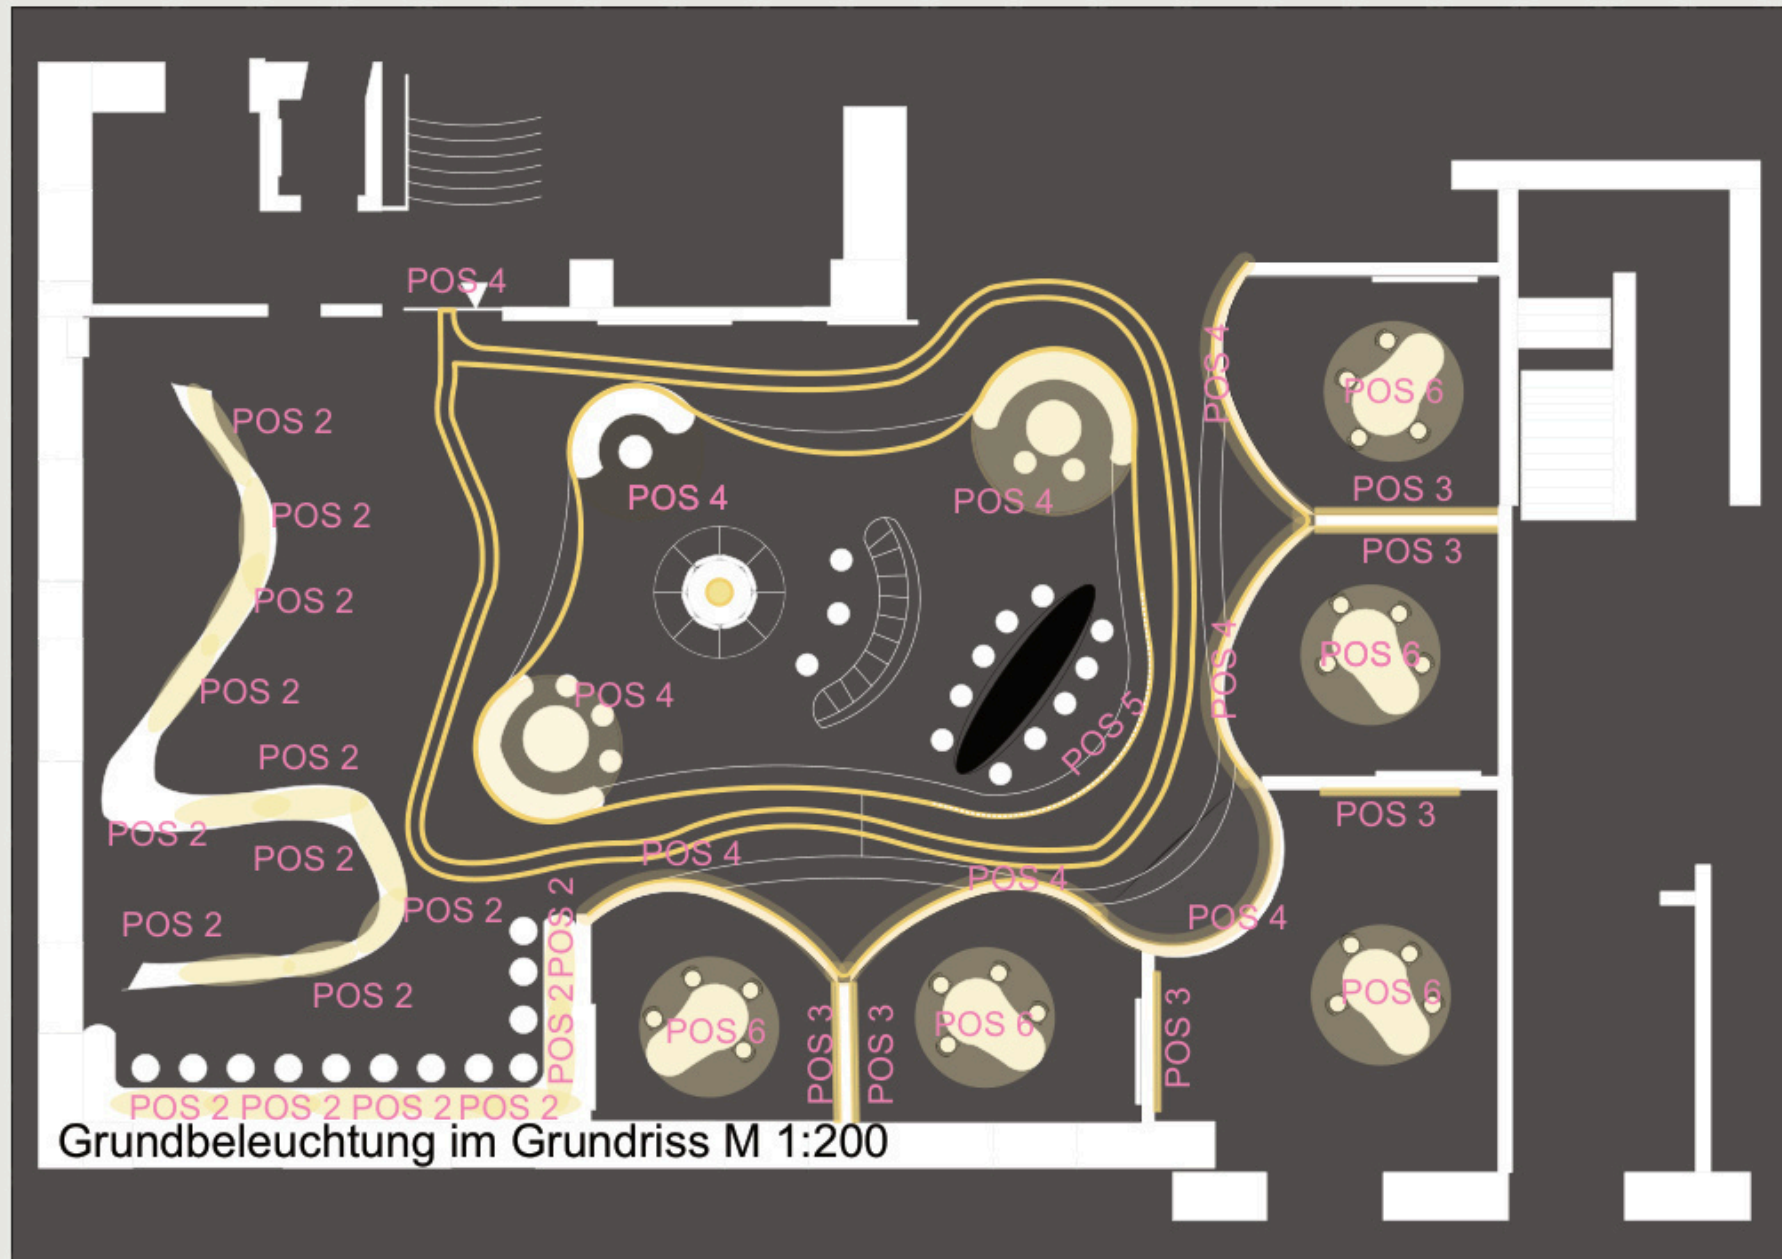

Zusatzbeleuchtung im Grundriss M 1:200

Leuchtlegende



POS
Leuchtentyp: Wide Flood Beam
Hersteller: Fa. Igguzini
Art.Nr.: QS40
Leuchtmittel: LED: 36W 4350lm
Lichtfarbe: 4000K CRI 80
Lichtverteilung: Wide Flood 58°
Vorschaltgerät: extern in Zwischendecke
Dimmung: DALI
Abmessung: ø180x44
Ausschnittsmaß: ø180
Einbauort: Grundlichtaustattung, überall
Zubehör: Abdeckung PA91
Stückzahl: 24




POS
Leuchtentyp: Pendelleuchte
Hersteller: Milan
Art.Nr.: Milan 505415
Leuchtmittel: LED Modul
Lichtfarbe: Warmweiß Extra 2700 K
Lichtverteilung: 43°
Vorschaltgerät: Trockenbaukasten extern in Zwischendecke
Dimmung: Dimmbar
Abmessung: ø210x55mm
Einbauort: Theke
Zubehör: externem Phasenanschnittsdimmer Georg Bechter Licht Kabelauslass Trockenbaukapsel
Stückzahl: 17



POS
Leuchtentyp: Wandleuchte
Hersteller: Lindby
Art.Nr.: Tjada 9626347
Leuchtmittel: 1x 5 W LED
Lichtfarbe: Warmweiß 3.000 K
Vorschaltgerät: Hinter der Lampe dimmbar
Dimmung: dimmbar
Abmessung: 218x75x75mm
Ausladung: 75 mm
Einbauort: Beratungsräume
Lichtstrom: 720 lm
Anschlussspannung: 230 VL
Schutzart: IP20
Stückzahl: 6



POS
Leuchtentyp: Effizienzleuchte
Hersteller: Fa. Igguzini
Art.Nr.: EA08
Leuchtmittel: LED: 1,7W 113 lm
Lichtfarbe: 2600K CRI 80
Lichtverteilung: 140°/109°
Vorschaltgerät: extern in Zwischendecke
Dimmung: PWM
Abmessung: 7004x100x2200
Einbauort: abgehängte Decke über der Lounge und den festen Möbeln, um die Beratungsräume
Zubehör: Befestigungsklammer X156 Konstantspannungsdimmer MPW3
Stückzahl: 22

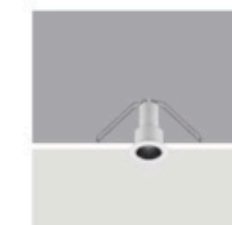


POS
Leuchtentyp: Effizienzleuchte
Hersteller: Fa. Igguzini
Art.Nr.: P310
Leuchtmittel: LED: 2W 121 lm
Lichtfarbe: 2700K CRI 90
Lichtverteilung: 25°
Vorschaltgerät: extern in Zwischendecke
Abmessung: ø31x58
Ausschnittsmaß: ø31
Einbauort: über den Lamellen
Stückzahl: 68




POS
Leuchtentyp: Pendelleuchte
Hersteller: Vencha OVAL
Art.Nr.: VE-5510133-GD-3K
Leuchtmittel: LED: 25W Max
Lichtfarbe: 3000K /5000K
Lichtverteilung: 25°
Vorschaltgerät: extern in Zwischendecke
Abmessung: 90mm x 405mm
Einbauort: in den Beratungsräumen
Stückzahl: 5



Deckenspiegel

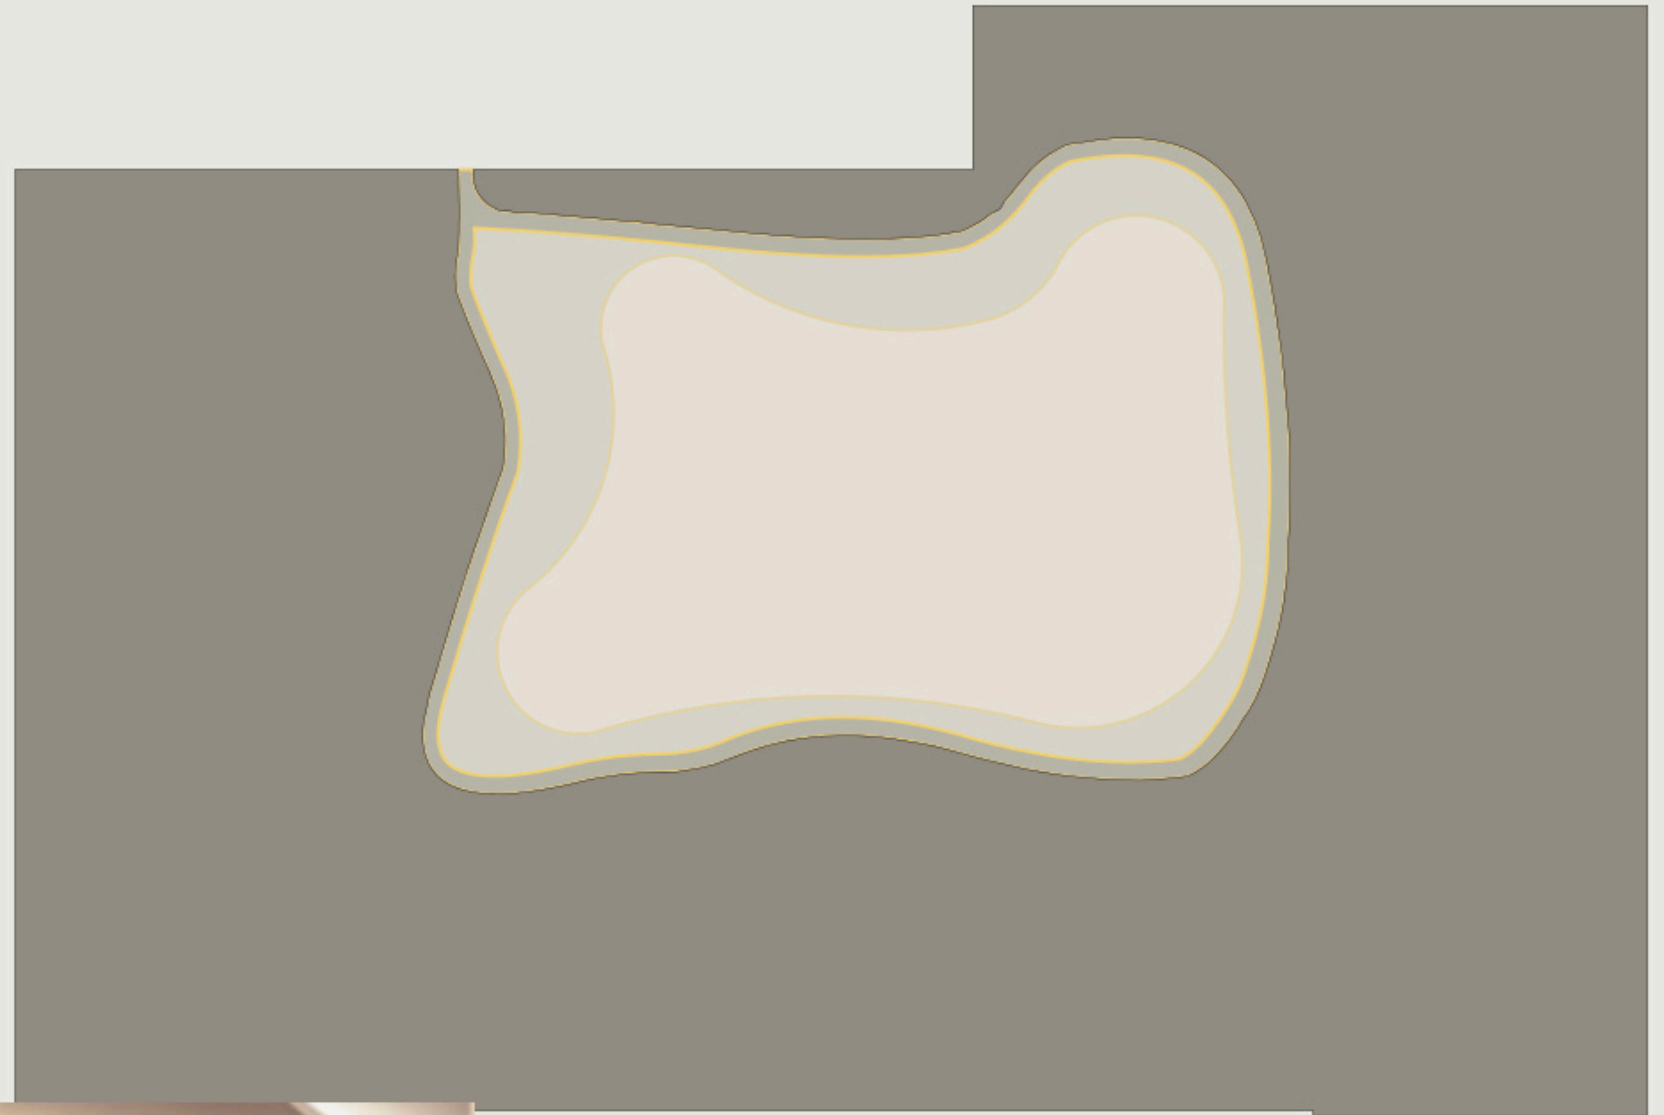


08

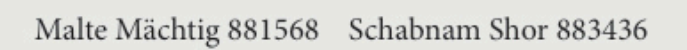

Detail-Beleuchtung_Trockenbaukapseln

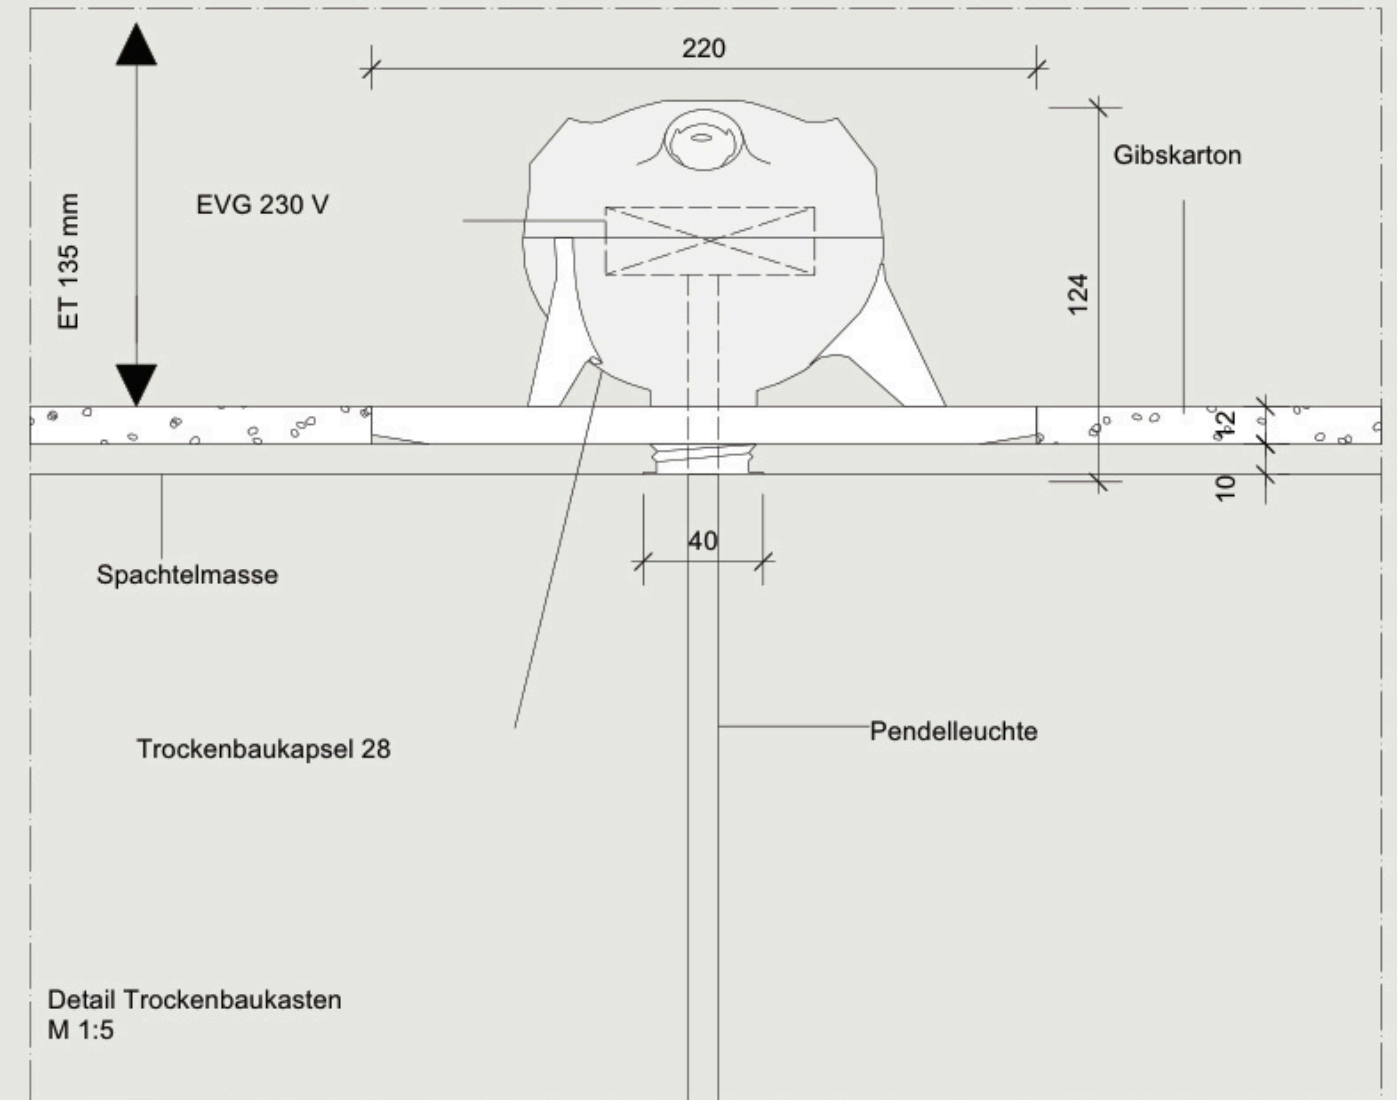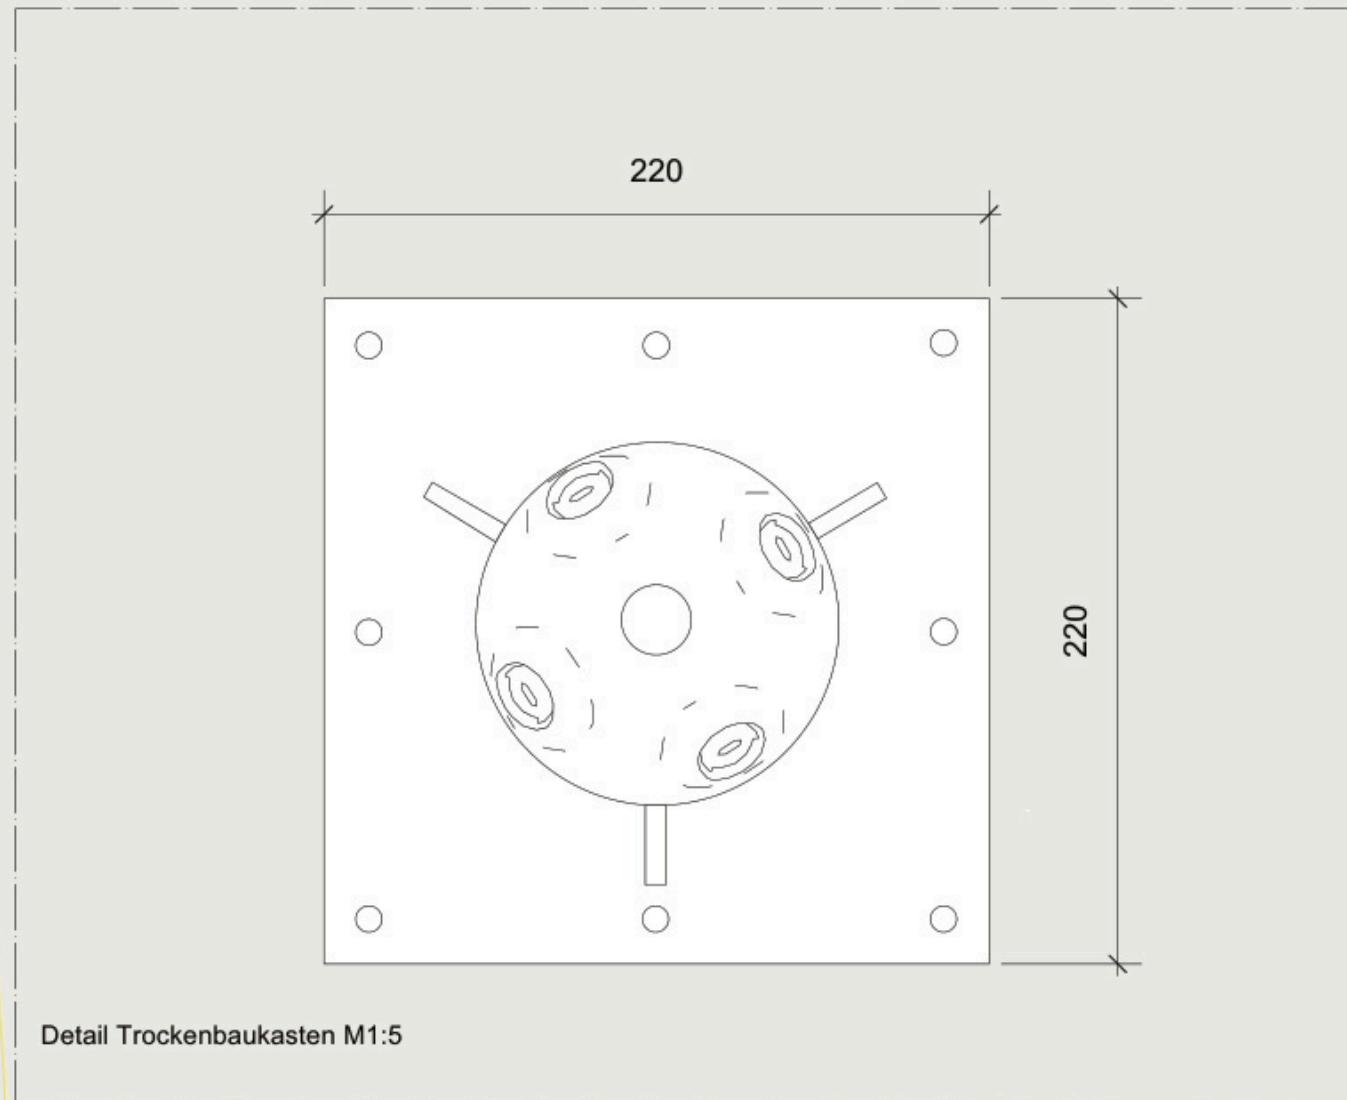

Detail-Beleuchtung_Lamellen

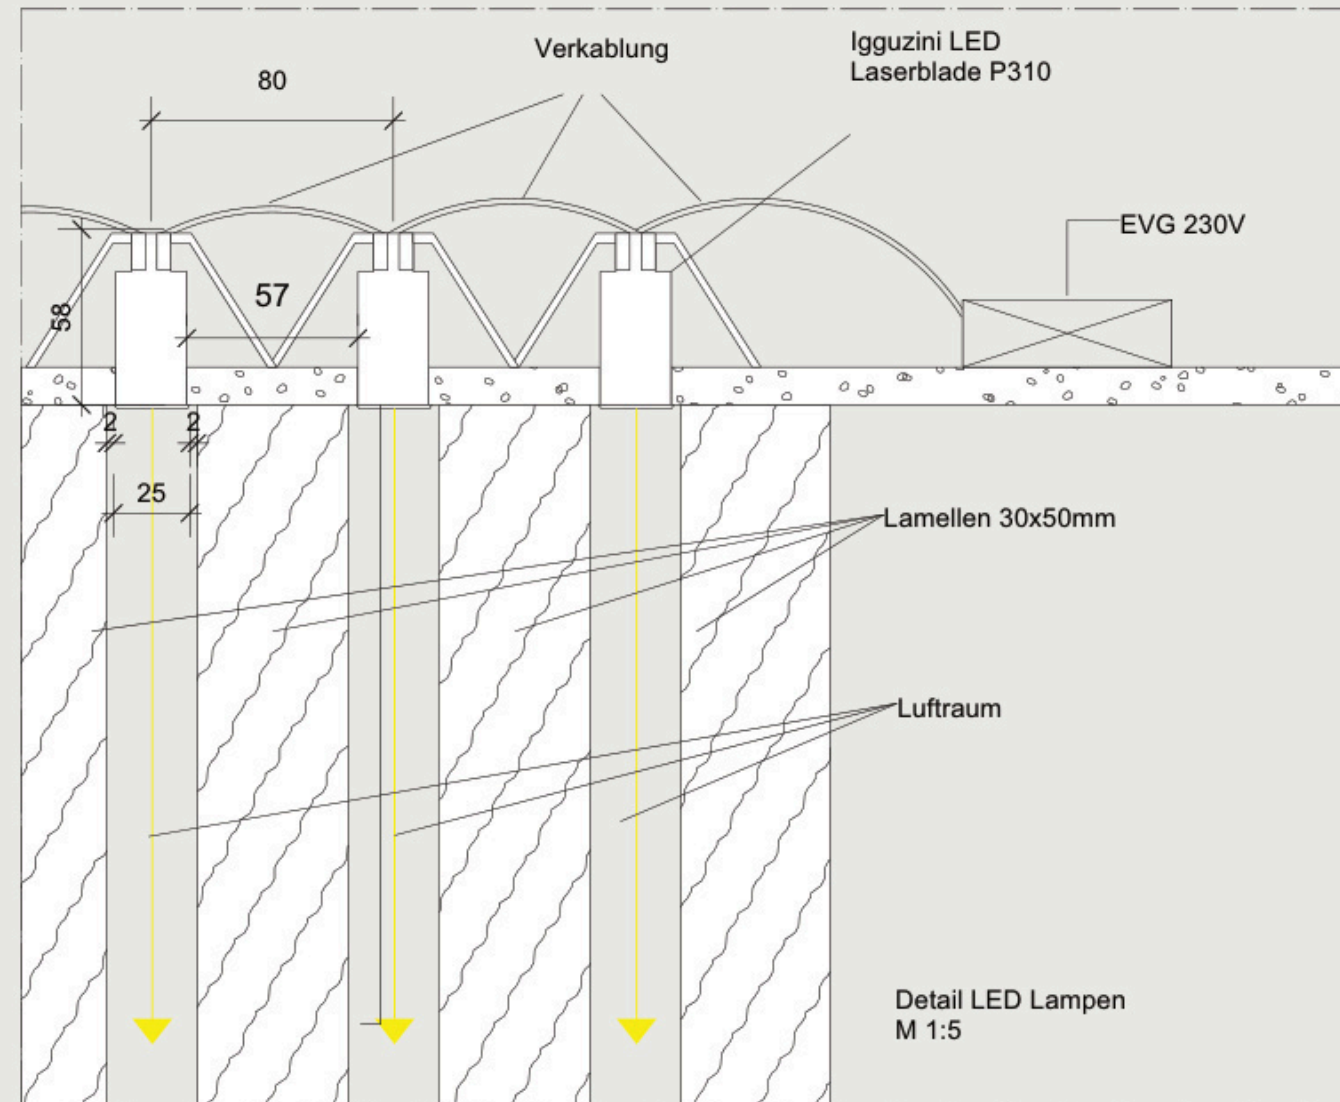



DANKE FÜR EURE AUFMERKSAMKEIT

